
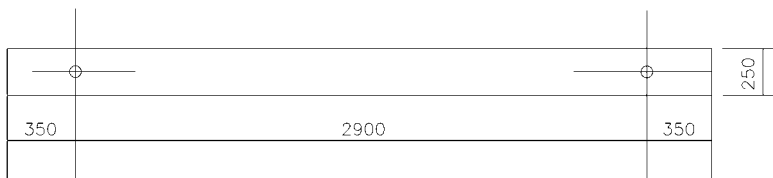



ITEM	CATALOGUE No
8	234507
9	240315
10	244208

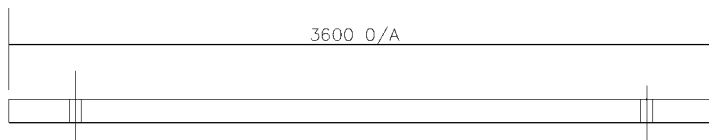

ITEM 8 3600 x 250 x 125 WOOD BAULK
SCALE :- 1:20



NOTES

1. TIMBER TO BE BALTIC REDWOOD, SCOTS PINE (PINUS SYLVESTRIS) OR FRENCH MARITIME PINE GENERALLY IN ACCORDANCE WITH BS1990 PART 1
2. BAULKS TO BE CUT FROM SAWN TIMBER TO PRODUCE RECTANGULAR SECTIONS
3. THE LONGITUDINALLY CUT SURFACES OF BAULKS SHALL BE STRAIGHT AND CLEAN CUT AND THE ANNULAR RINGS SHALL BE APPROX. PARALLEL TO WIDE FACE. PLANNING IS NOT REQUIRED
4. BAULKS SHALL BE TREATED AFTER FABRICATION WITH CREOSOTE TO BS913 (RUEPING PROCESS) OR WATERBORNE SALTS (TANALITH) TO 4072
5. STEELWORK TO BS4360, GRADE 43A AND BS449
6. FLATS TO BS6722. ANGLES TO BS4848 PART 4
7. GALVANISING TO BS729 AFTER FABRICATION

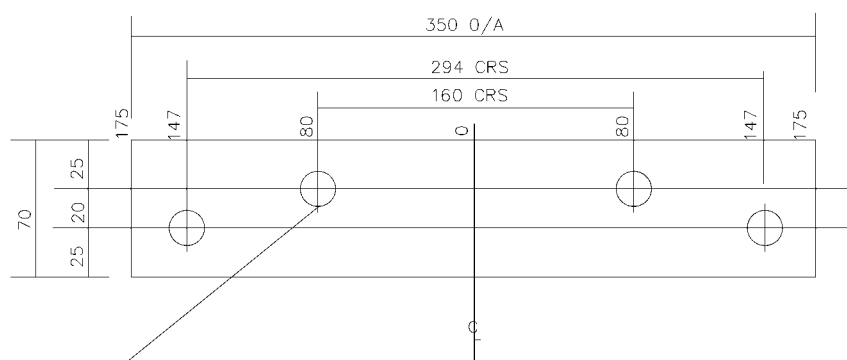


4 No. 18 DIA HOLES

ITEM 10 70 x 15 x 350 LONG - FLAT BAR
SCALE :- HALF FULL SIZE

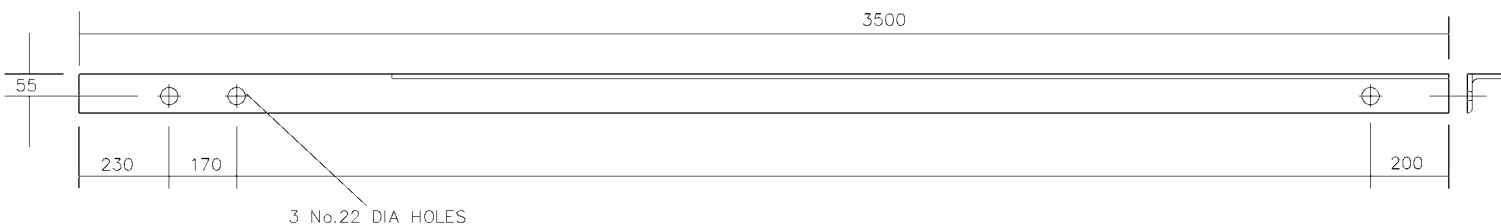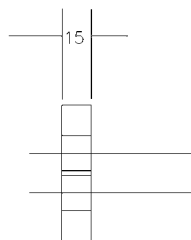

3 No.22 DIA HOLES

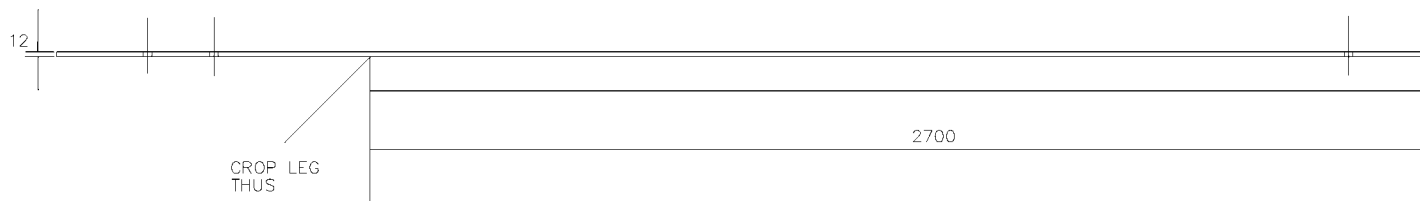

ITEM 9 100 x 100 x 12 ANGLE - 3500 LONG
SCALE :- 1:10

ALL DIMENSIONS SHOWN ARE IN MILLIMETRES UNLESS OTHERWISE STATED

		Lloyds Court, 78, Grey Street, Newcastle Upon Tyne NE1 6AF			
		66kV OVERHEAD LINES PORTAL TYPE CROSSARM AND SPECIAL FOUNDATION COMPONENTS			
Prepared by	J.L.W.	Drg.No.	1 09 101 0650	Sheet No	3
Checked	G.H.	Date Issued	OCT 85	Revised	6/12/04
Mod			A B C D E	Scale	AS SHOWN