

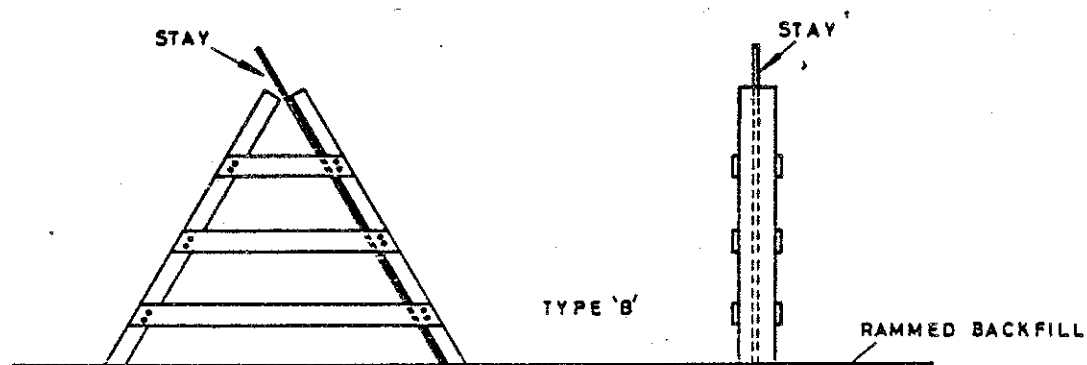


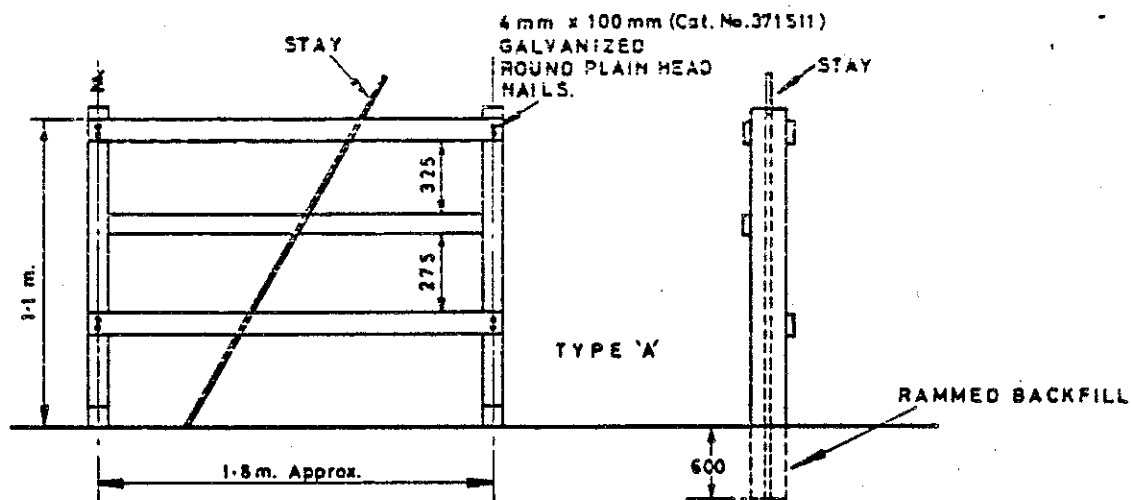

NOTES:- RAILS 87mm x 38mm x 4.0m Long (Cat. No. 345381)
POSTS 150mm x 75mm x 1.8m Long (Cat. No. 345220)
APPROX. HEIGHT OF FENCE 1.2m.

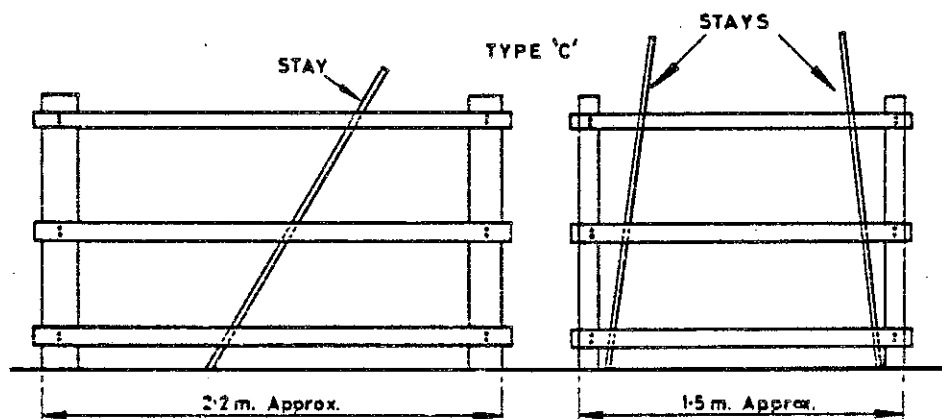

NOTES:-

1. FENCE DIMENSIONS AS B.S. 1722: PART 7: FENCE TYPE SP11/3 AS TABLE 1.
2. TIMBER SPECIES TO BE IMPORTED EUROPEAN REDWOOD (PINUS SYLVESTRIS) OR HOME GROWN SCOTS PINE.
3. TIMBER TO BE PRESERVED CATEGORY A IN ACCORDANCE WITH B.S. 5589, PRESSURE TREATED TO B.S. 913 OR B.S. 4072.
4. WIRE NAILS TO B.S. 1202: PART 1: TABLE 1, GALVANIZED FINISH.

WORKS SPEC. REF. No. 04/311.

		ENGINEERING DIRECTOR'S DEPT. CARLIOL HOUSE, NEWCASTLE-UPON-TYNE		
		FENCING STAYS		
Drawn		Drq No	1 09 101 0099	Sheet No. 1.
Traced P.L.				No. of Sheets
Checked R.M.D.				Scale: N.T.S.
Date issued DEC '85		Mod: A		