
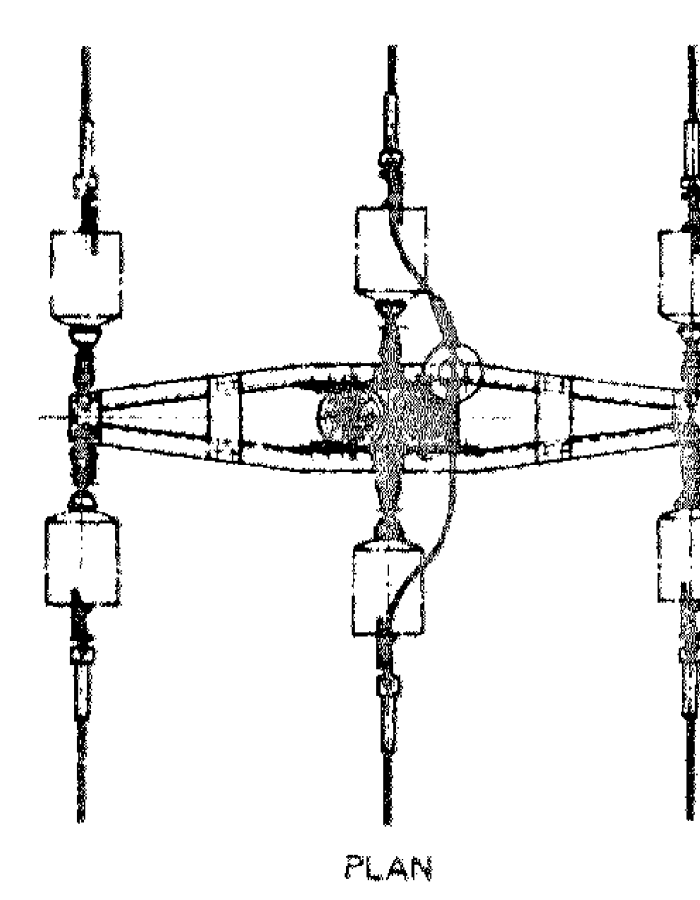
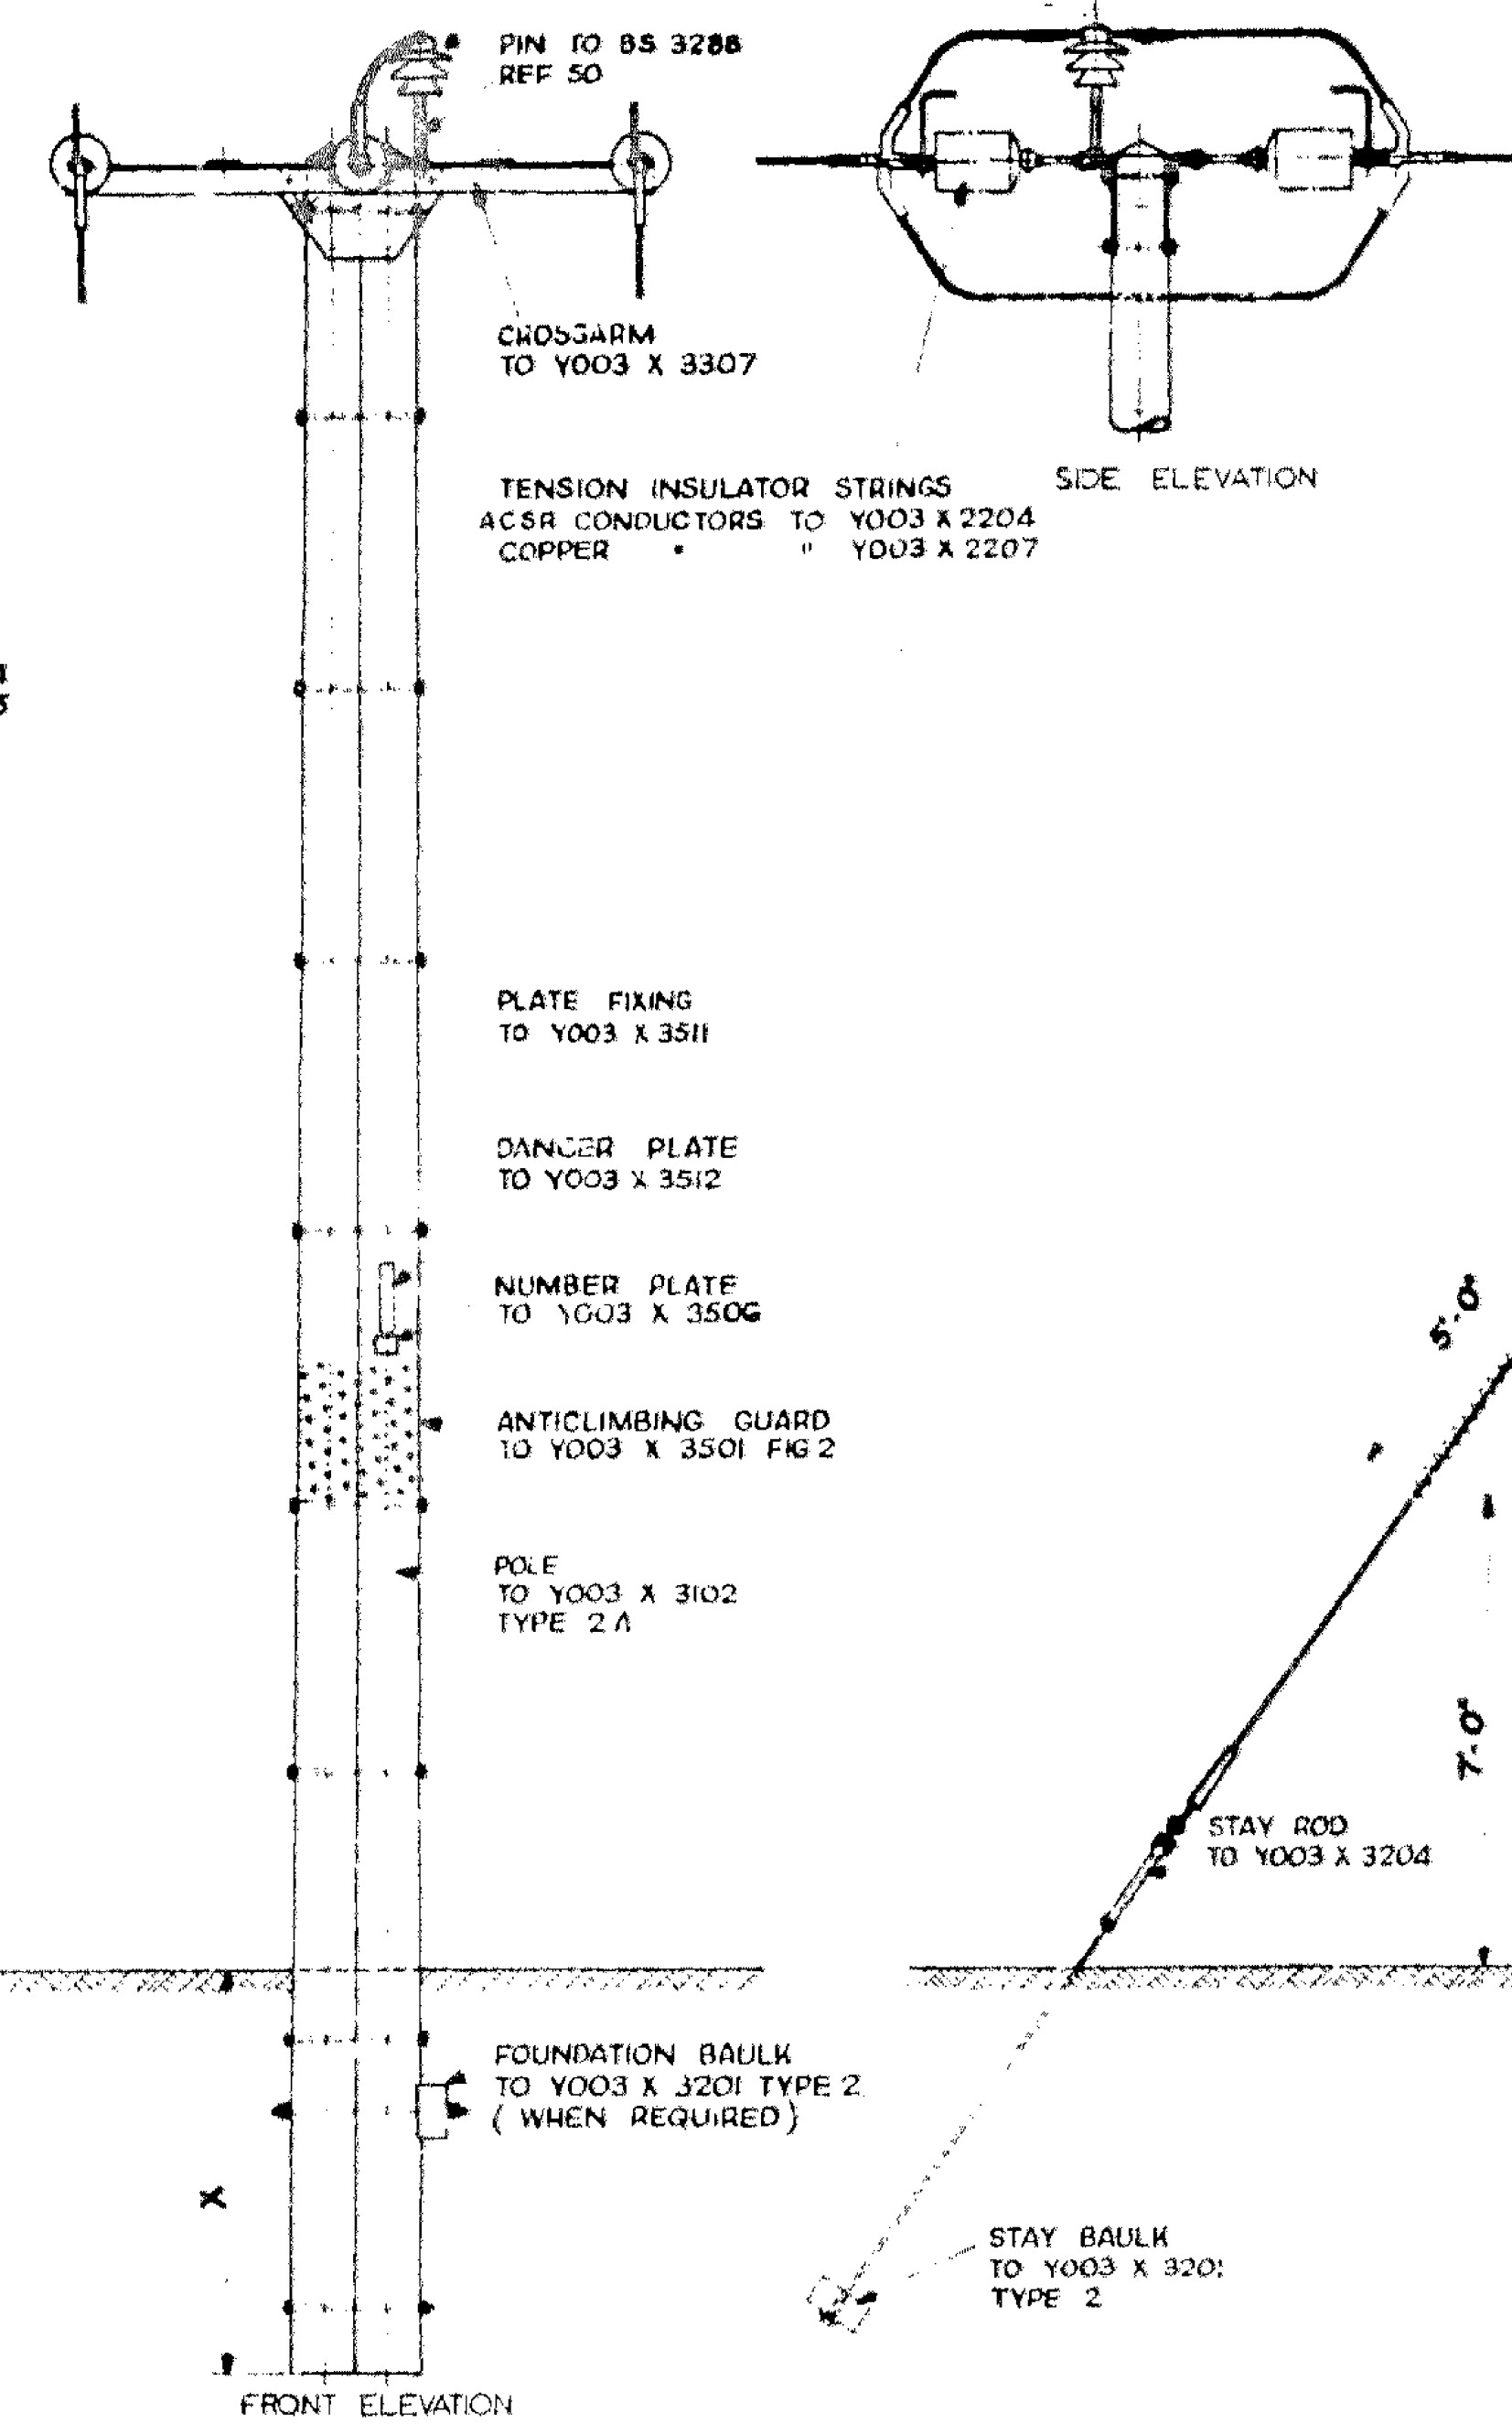
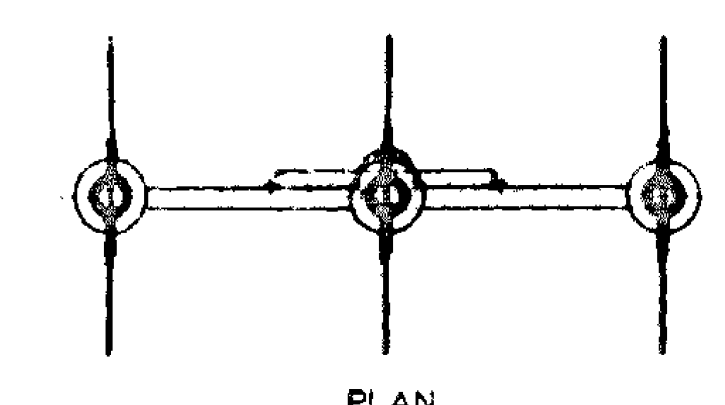
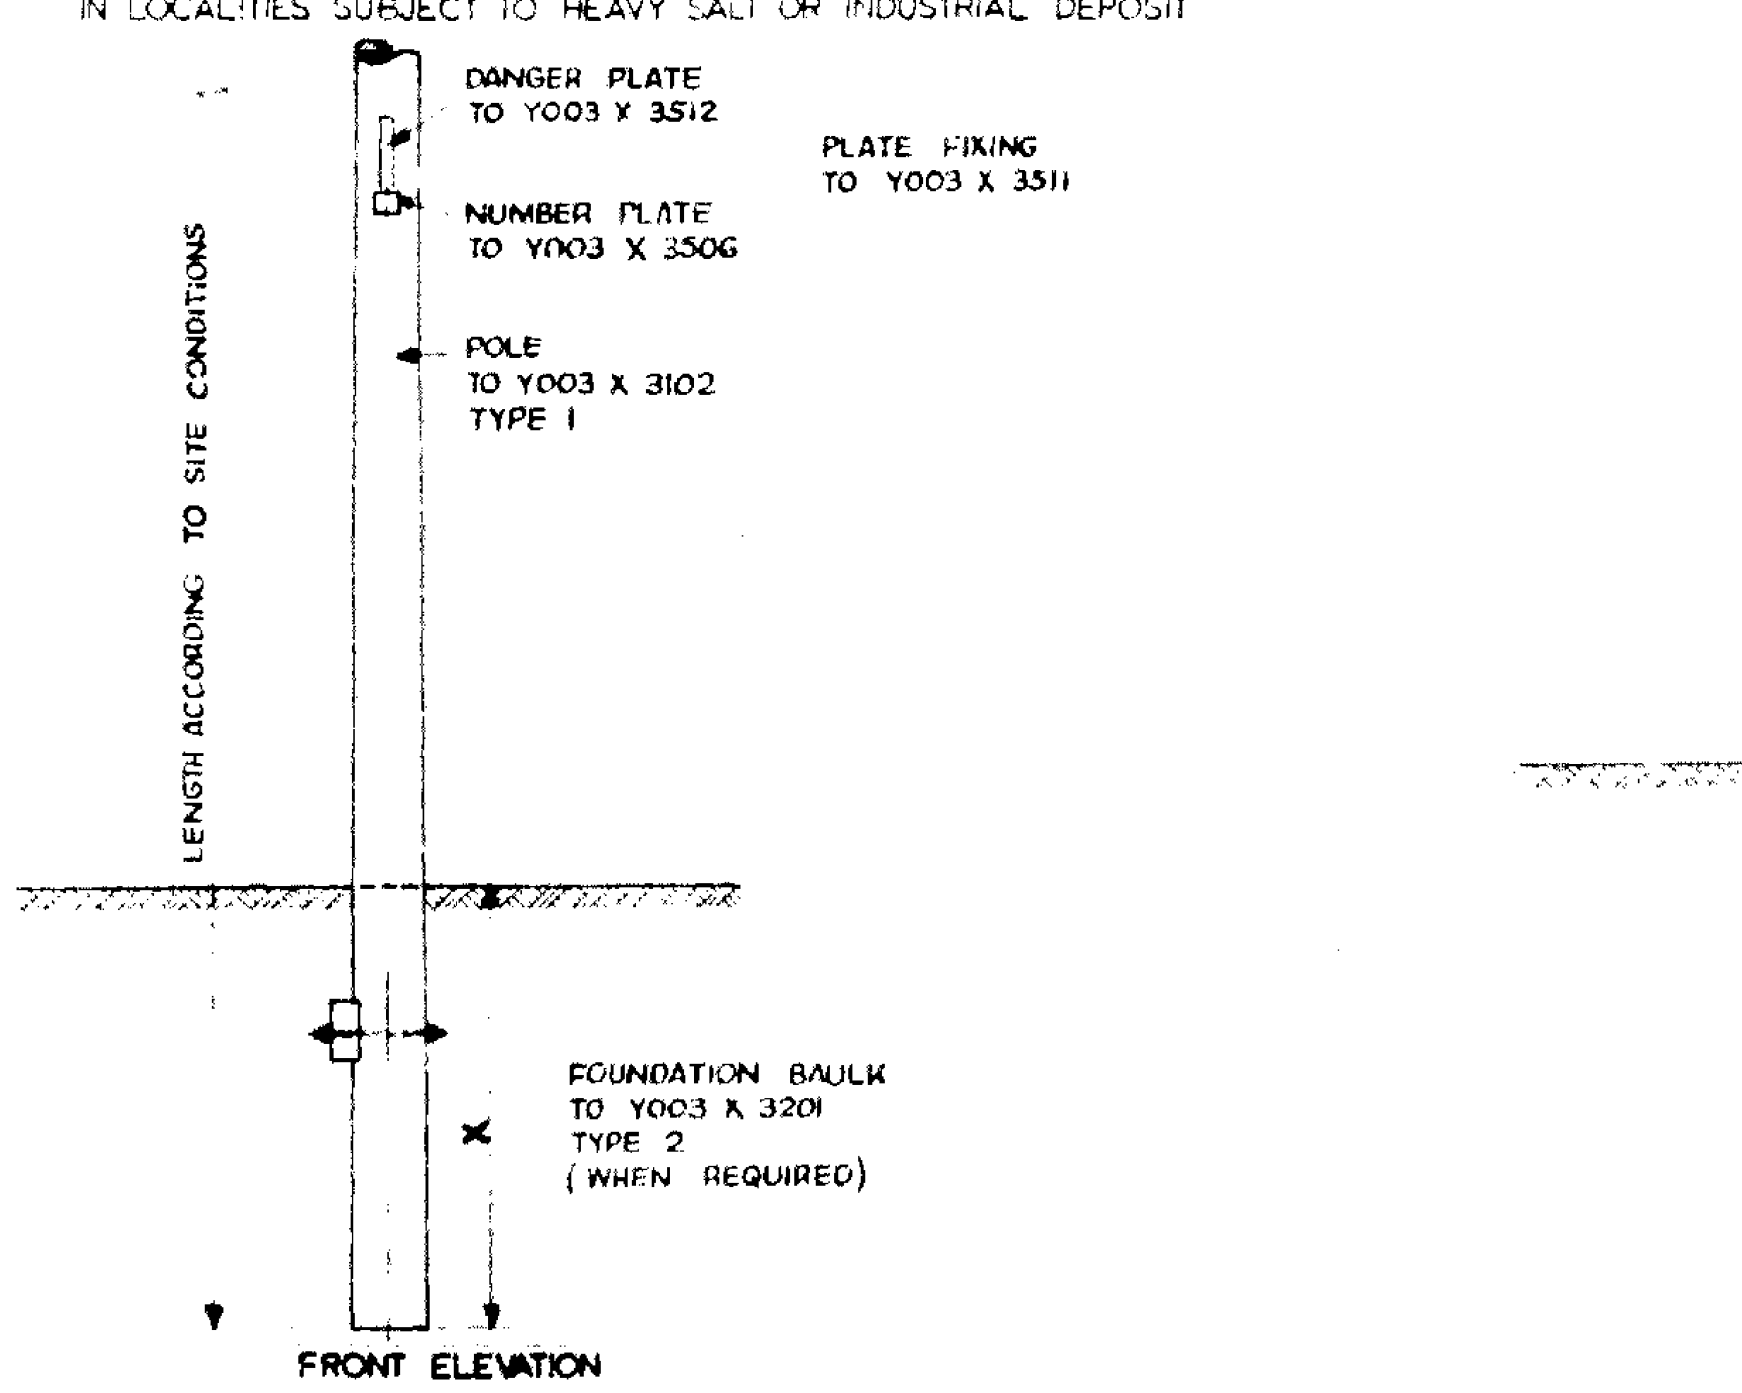
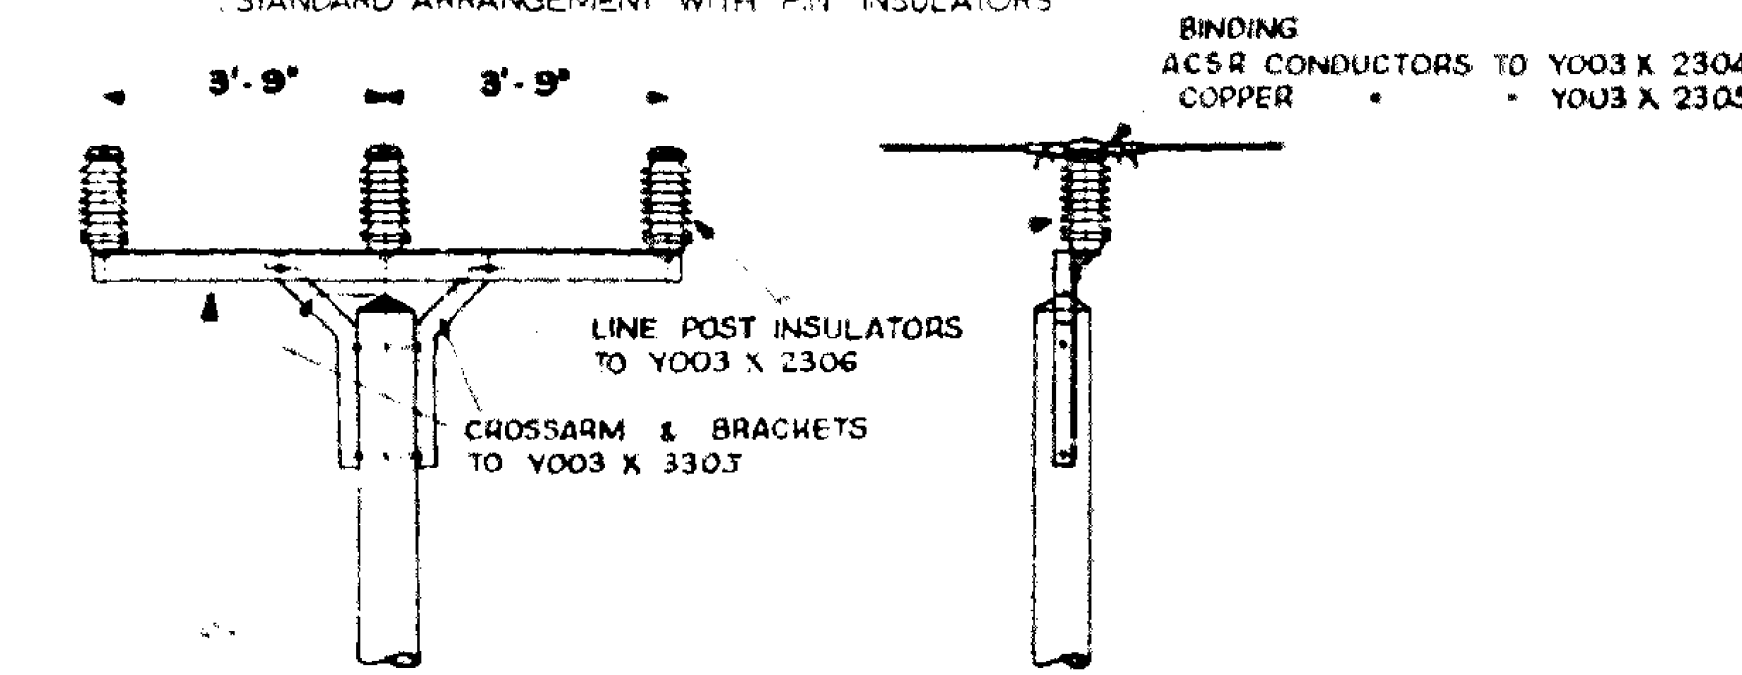




INTERMEDIATE POLE

SECTION POLE

ANGLE POLE

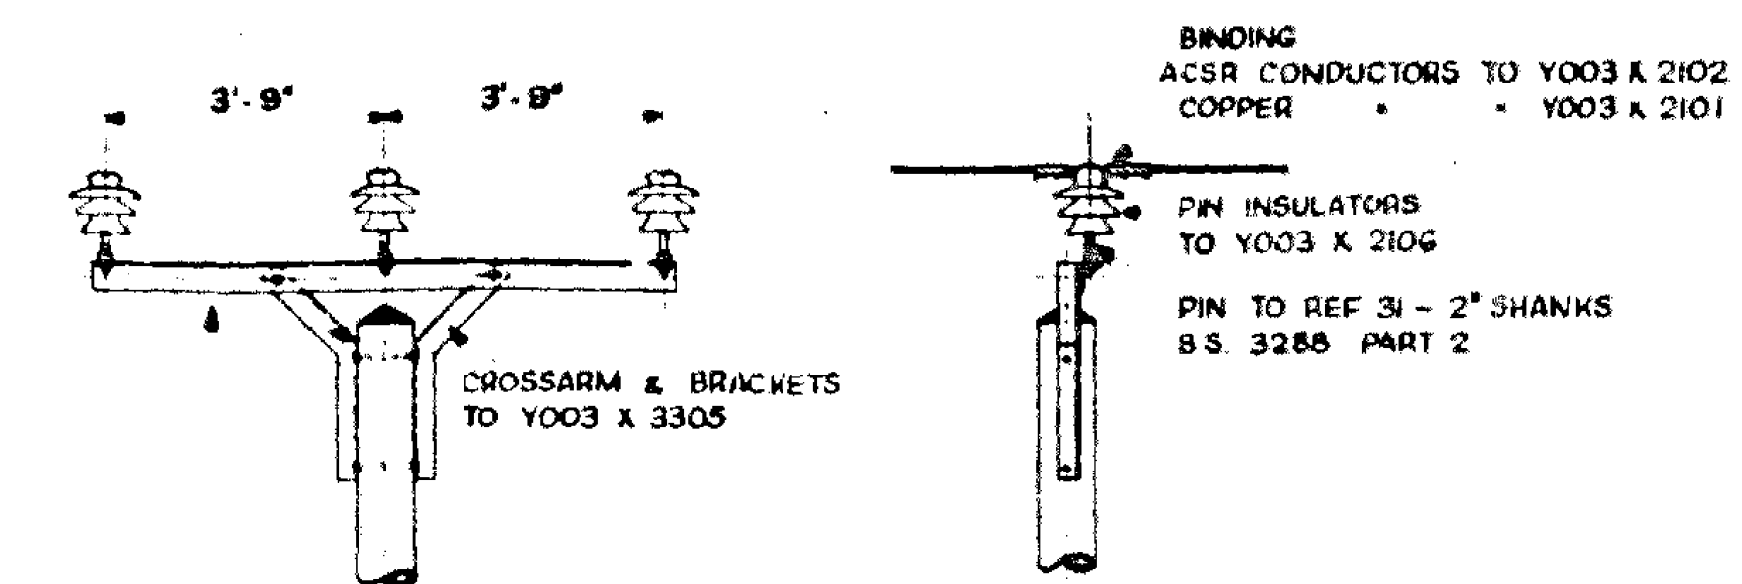

LENGTH OF POLE	DIMENSION X
UP TO 38'-0" OVERALL	6'-0"
39'-0" TO 42'-0" "	6'-6"
OVER 42'-0" "	7'-0"

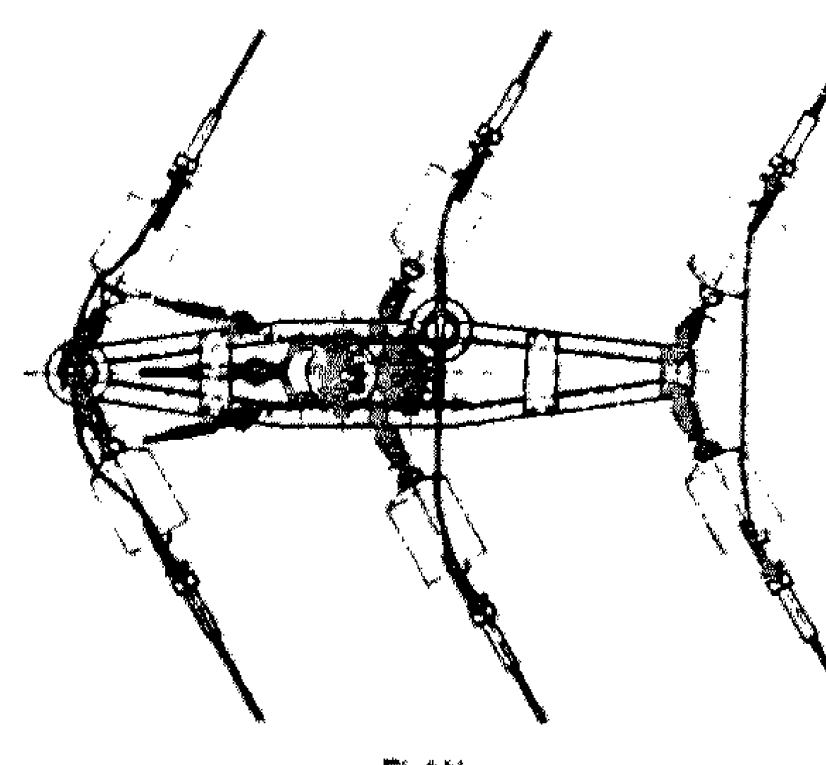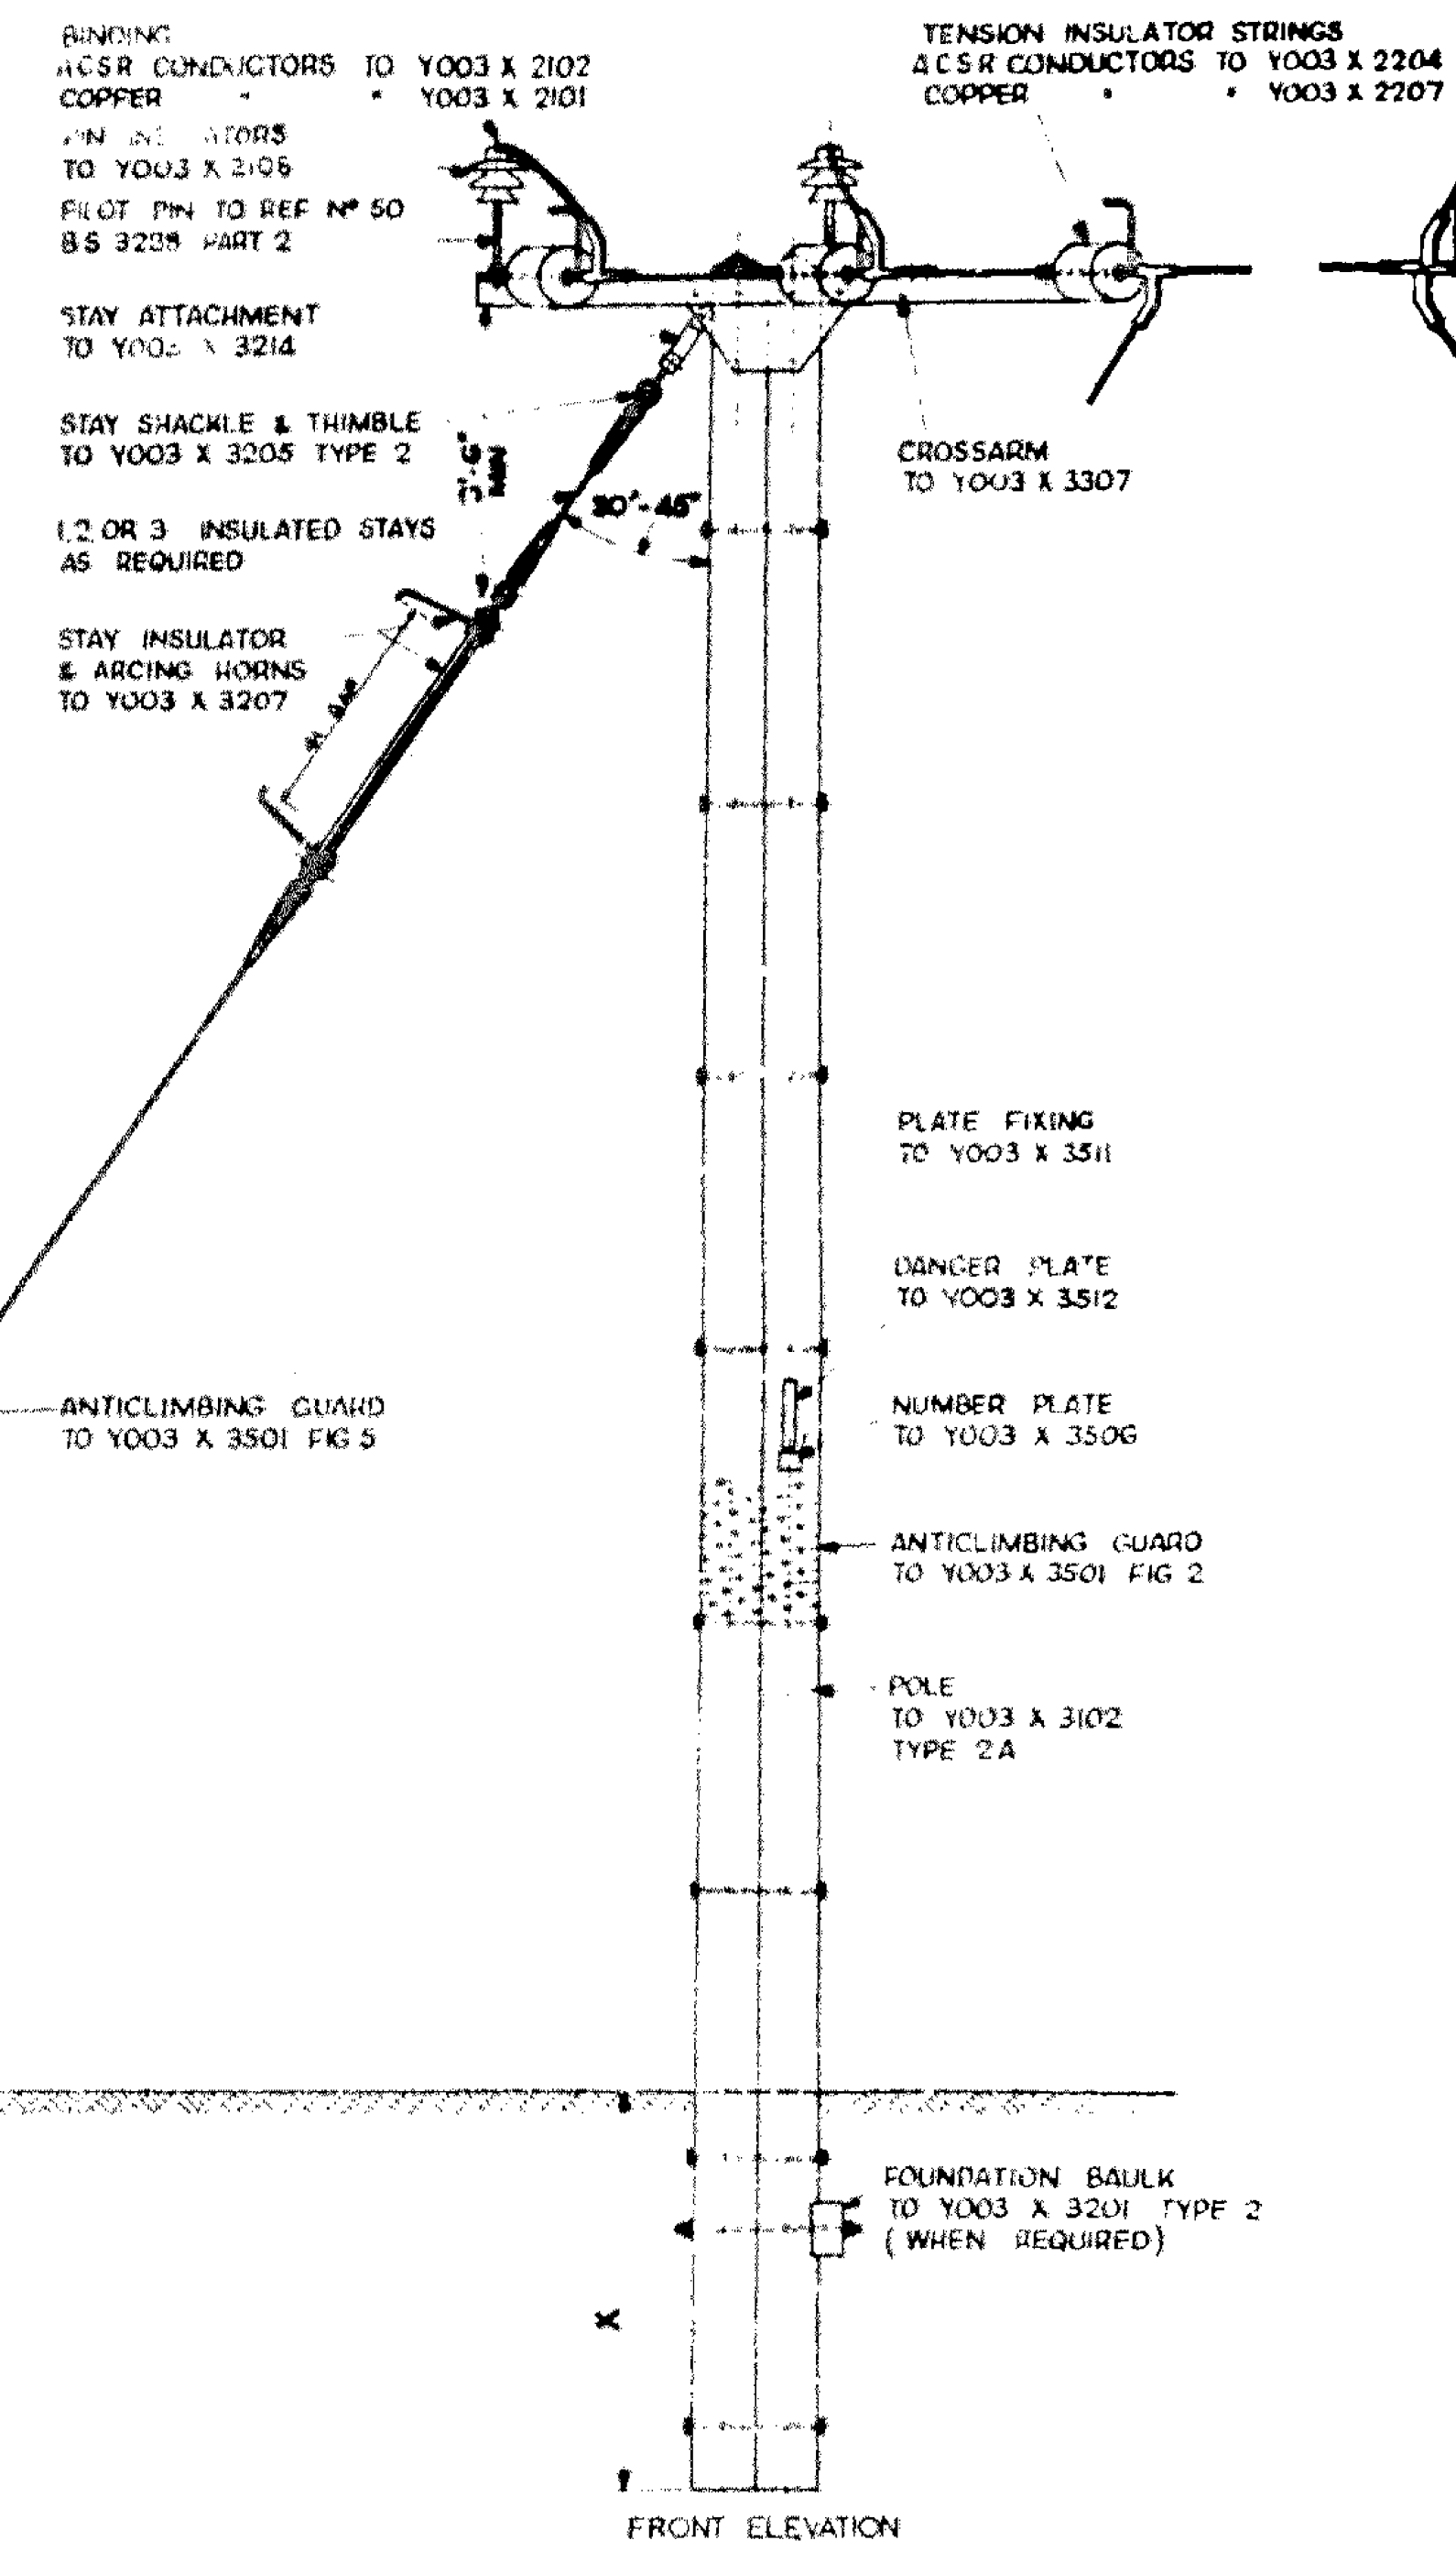

10-2-66																		
H	REDRAWN & REVISED	C.S.	26	J DANGER PLATE REFERENCE NUMBER AMENDED	J.M.W.	11	K SECTION & ANGLE POLE TOPS AMENDED	J.H.	15	L	M	N	P					
A	ORIGINAL ISSUE	R.T.P.	20	B ANGLE OF DEVIATION PERMANENT STAY INSULATOR & SURGE DIVERTER SUPPORTS MODIFIED	A.G.	12	C PLAN VIEW OF ELEVATION OF TERMINAL POLE ADDED	A.J.	1	D CROSSARM TERMINAL POLE & DRG REF N° MODIFIED	M.F.B.	2	F RETRACTED OMITTING TERMINAL POLE	J.L.B.	2	G REDRAWN & REVISED	J.L.S.	2
 Y003 X 1102																		

OVERHEAD LINES SPEC CE/C/36

GENERAL ARRANGEMENT OF INTERMEDIATE, SECTION & ANGLE POLES

Y003 X 1102