
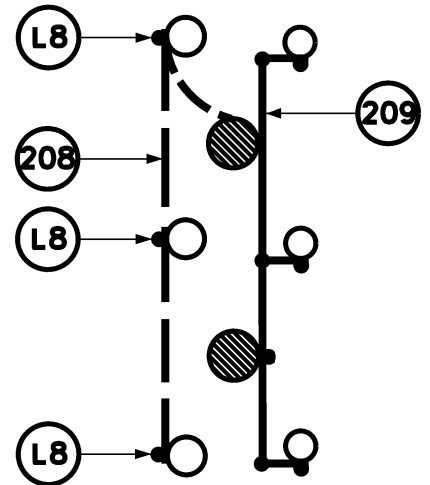
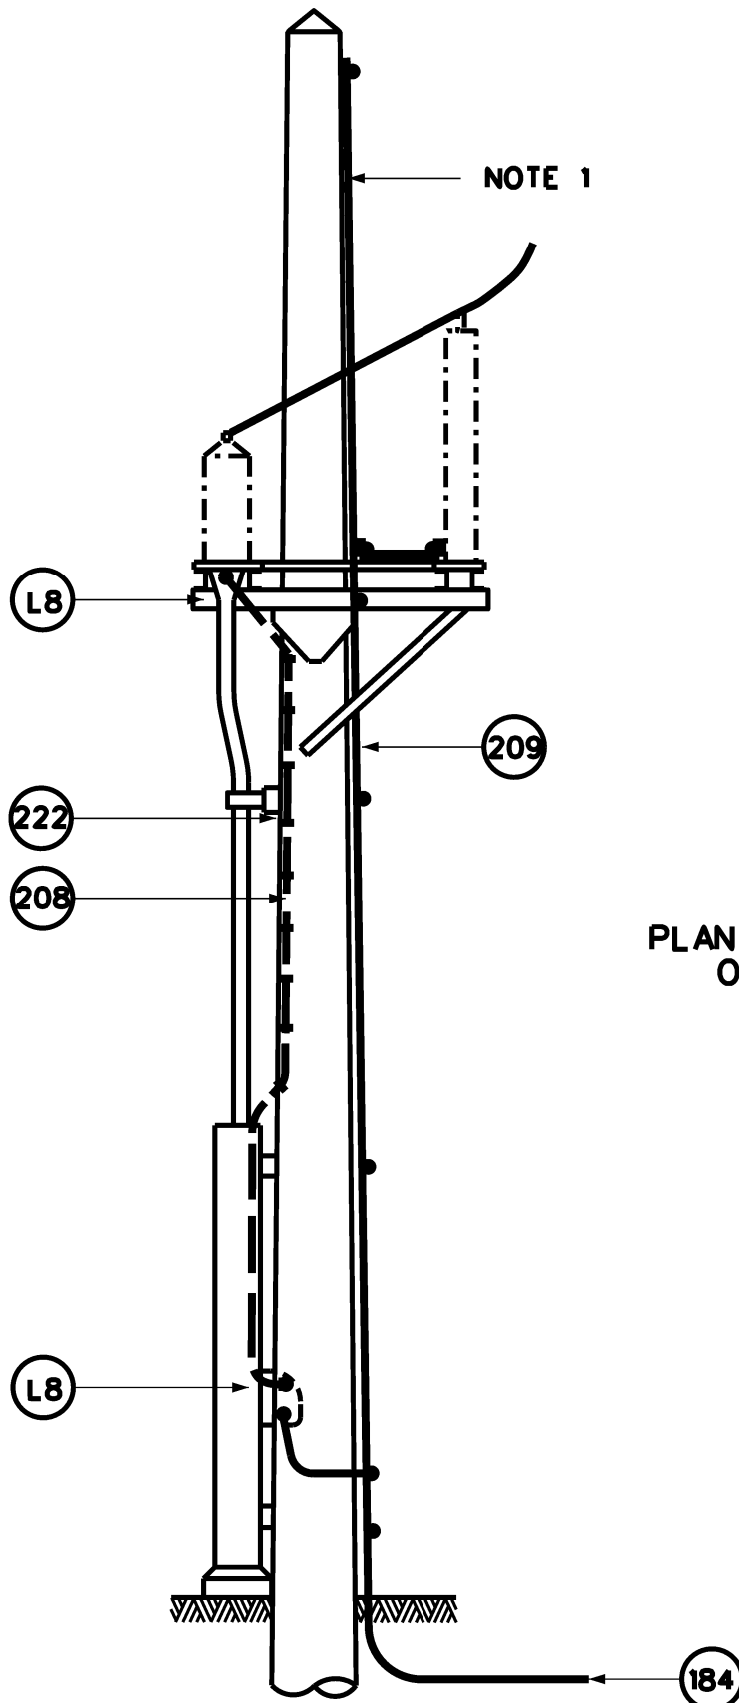


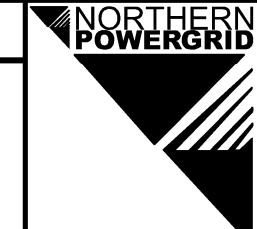

PLAN VIEW OF EARTH CONNECTION
ON SEALING END PLATFORM

• BOLTED CONNECTION - NOTE 2

drawn	BT	EARTHING DIAGRAM				
traced	JMP	66kV CABLE TERMINATION WITH SURGE DIVERTERS CE/C/37(M)				
checked	JMG					
approved	BT					
revision	B	date	7-6-90	original scale		Y204L0404