
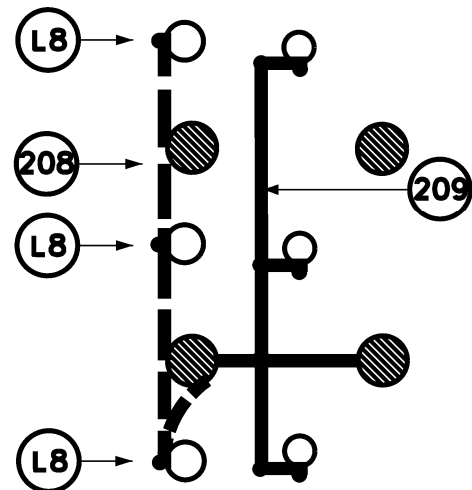


Copyright of Northern Powergrid Holdings Company. No part of this drawing to be reproduced without prior permission.

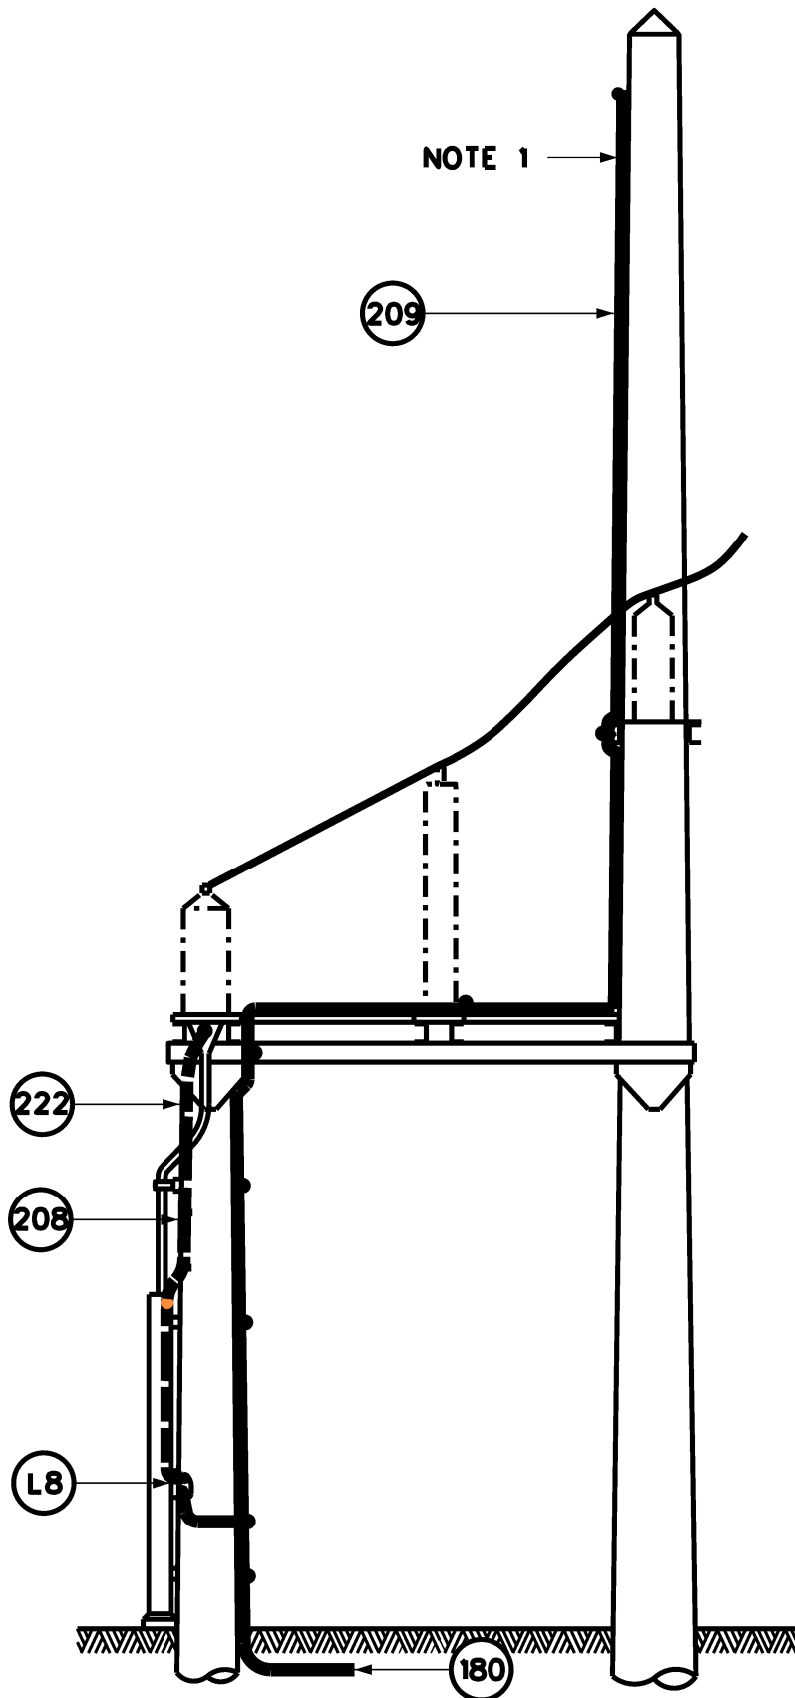

PLAN VIEW OF EARTH
CONNECTIONS ON
SEALING END PLATFORM

• BOLTED CONNECTION - NOTE 2

drawn	BT	EARTHING DIAGRAM				
traced	JMP	66kV CABLE TERMINATION WITH SURGE DIVERTERS 15.0-18.0m POLES				
checked	JMG					
approved	BT					
revision	A	date	8-6-90	original scale		Y204L0405