


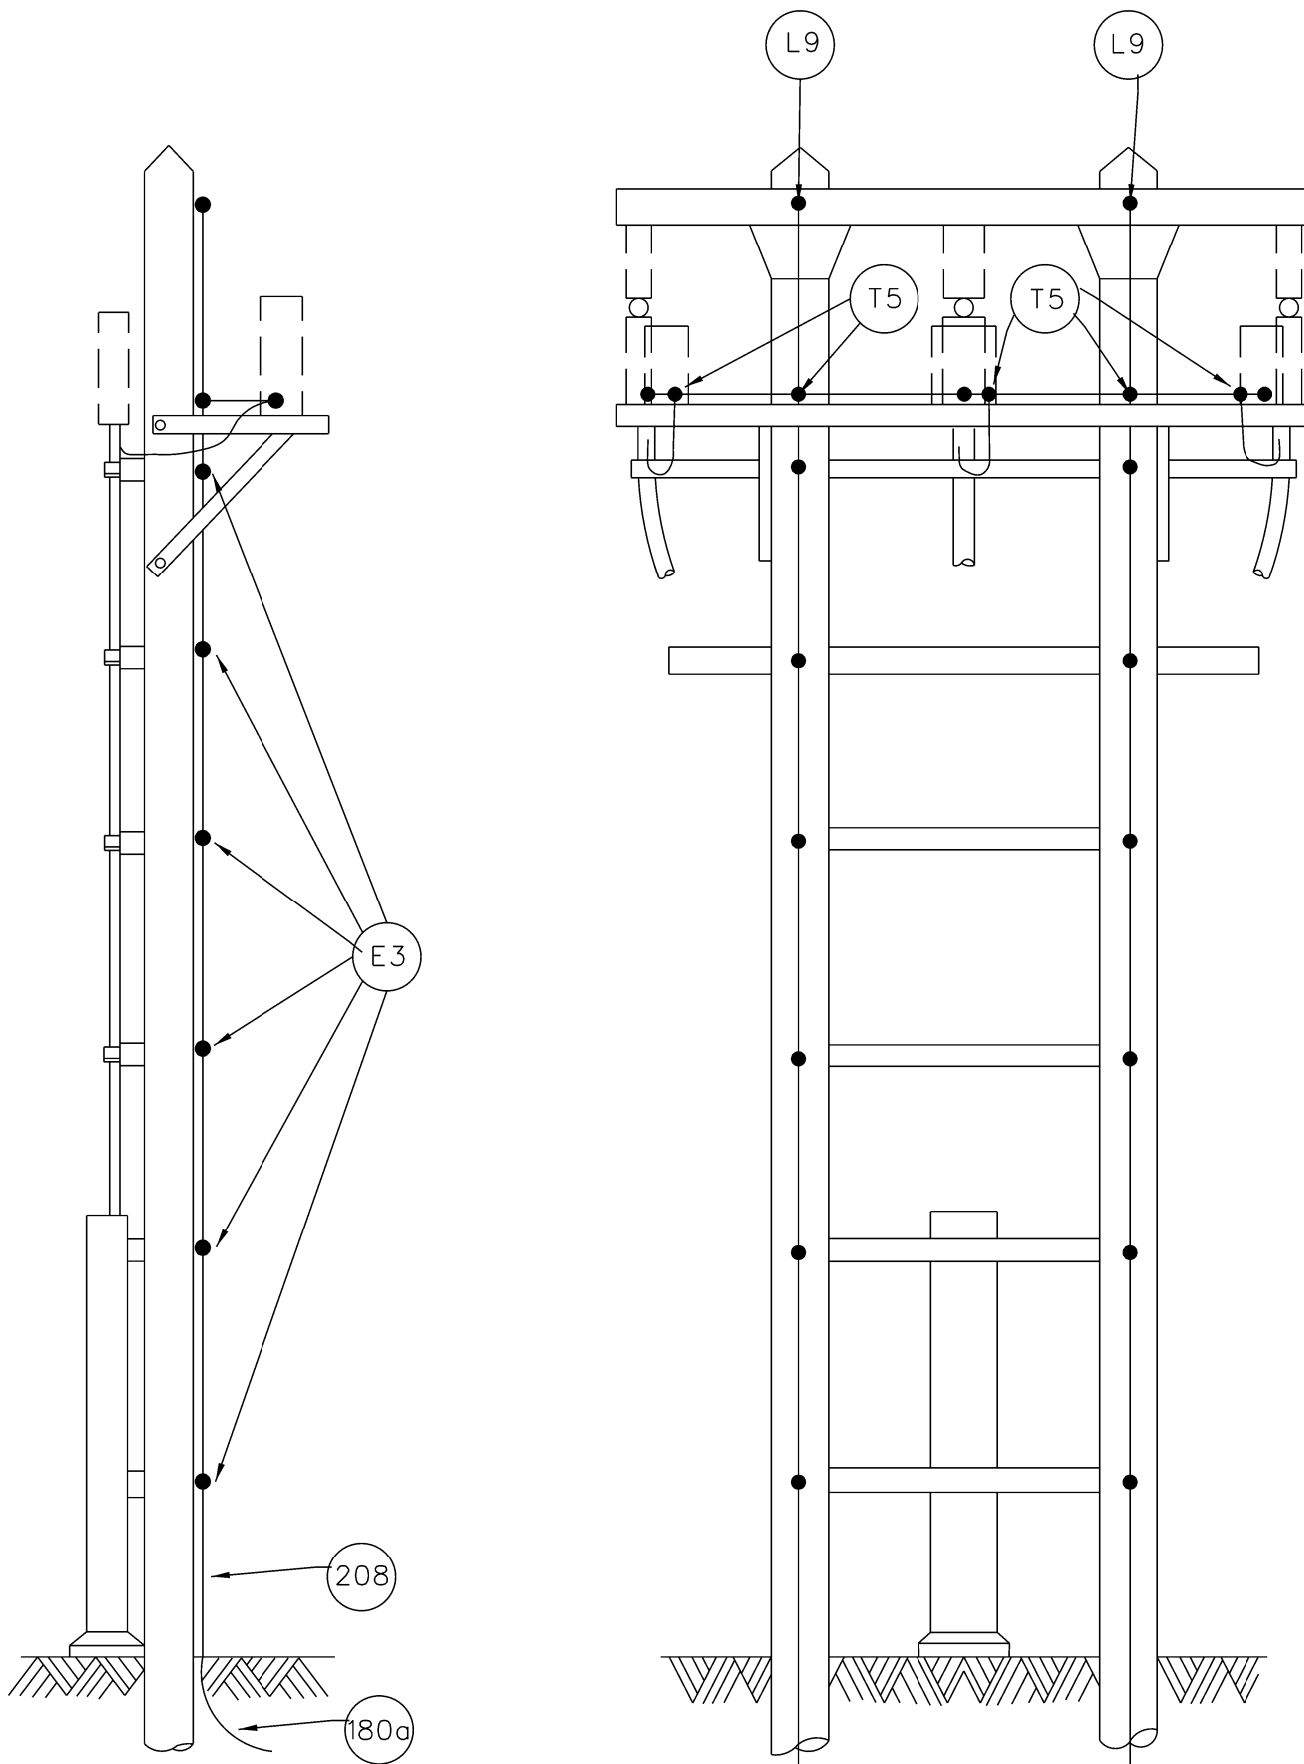

 CE Electric UK		Lloyds Court, 78 Grey Street, Newcastle Upon Tyne, NE1 6AF	
Manufacturer Details		EARTHING DIGRAM 66KV CABLE TERMINATION WITH MBA 75 SURGE DIVERTERS	
Sheet No. 1	Scale N.T.S.		
Prepared By Janis.Webb		Type OVERHEAD	LINES
Revised 25/05/07	Grid Reference	Ref No. C948748	Historic Drg.No. Y204L0409
Date Issued 24/05/07	Checked By	Revision A	Notes