


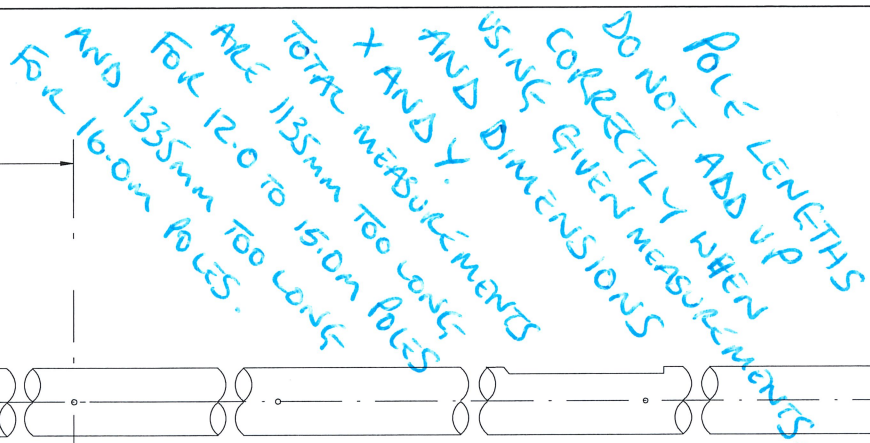

SAME ISSUE WITH TRS AS ON MY NOTES ON 1.09.123.1187541N

- ALL DIMENSIONS SHOWN ARE IN MILLIMETRES UNLESS OTHERWISE STATED**

 NORTHERN POWERGRID		Lloyds Court, 78 Grey Street, Newcastle Upon Tyne, NE1 6AF	
Manufacturer Details		33kV SINGLE CIRCUIT LINES	
Sheet No. 10	Scale 1:20	DRILLING SCARFING AND MARKING FOR TERMINAL SUPPORT WITH SURGE ARRESTORS AND HEAT SHRINK TERMINATION AS SHOWN ON 1.09.123.1173 SHEET 9	
Prepared By Caralyn Palmer	Type OVERHEAD	POLES	
Revised 27/03/15	Grid Reference	Ref No. C976718	Historic Dwg. No. 1091231173
Date Issued 24/06/09	Checked By S SALKELD	Revision A	Notes