

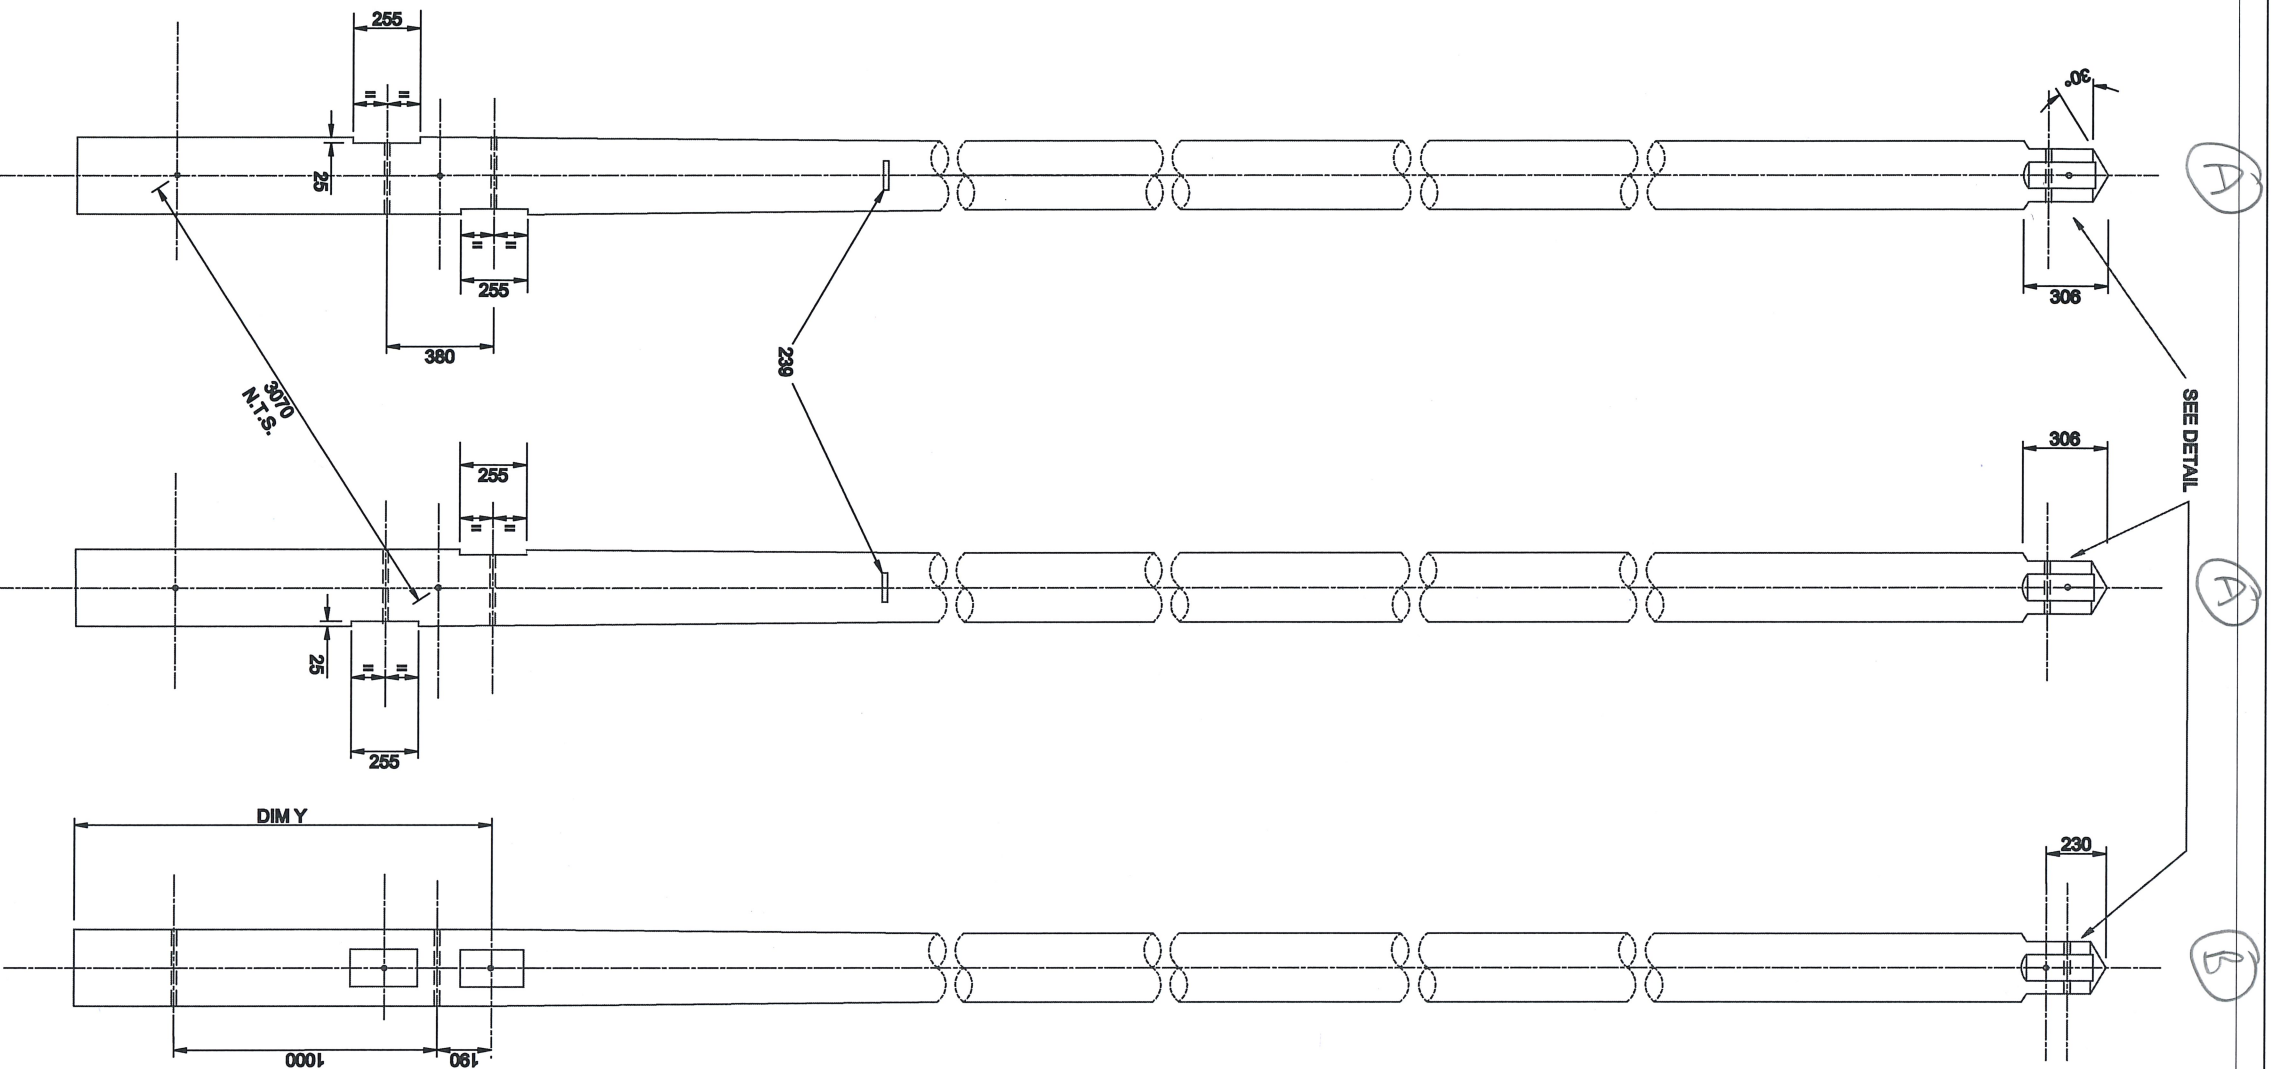


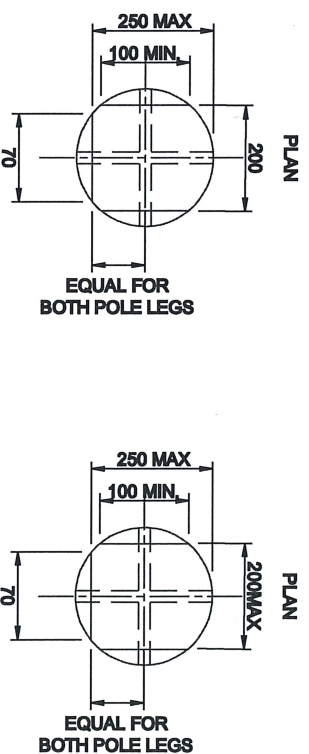

- NOTES:
- POLE LEGS TO BE MATCHED. POLE TOP MINIMUM DIAMETER BEFORE FABRICATION TO SUIT POLE FIGS.
 - ALL HOLES TO BE 22mm DIA. DRILLED AT RIGHT ANGLES TO VERTICAL CENTRE LINE OF POLE. ALL DRILLING AND CUTTING TO BE DONE STRICTLY TO TEMPLATE PRIOR TO CREASOTING.
 - POLE BUTTS TO CUT AT RIGHT ANGLES TO AXIS OF POLE.
 - POLE LEGS TO BE NOTCHED AND DRILLED FOR 250 X 125 WOOD BALUKS AS SHOWN
 - POLE TO BE SUPPLIED WITH 4 - 1300 X 250 X 125 BALUKS TO DRG NO 1 00 043 9130 TYPE 2 CUT FROM THE SQUARE AND 4 - M20 GALVANISED BOLTS EACH WITH 1 FLAT AND 1 CURVED GALVANISED WASHER TO DRG NOS 1 00 043 8604 AND 9805 RESPECTIVELY.
 - HOLES NOT REQUIRED FOR PARTICULAR APPLICATIONS WILL BE PLUGGED ON SITE

ALL DIMENSIONS SHOWN ARE IN MILLIMETRES UNLESS OTHERWISE STATED

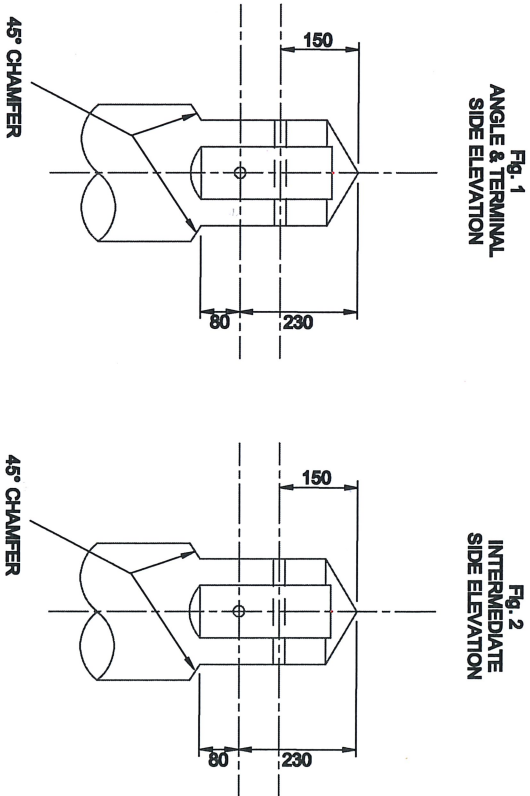

POLE TOP MIN. DIA. BEFORE FABRICATION EISTOUT 228mm (NORMALLY FABRICATED FROM STD. POLE HEIGHT PLUS 2m.

DETAIL SCALE 1/10

AS SHOWN IN THE DETAIL ABOVE, THIS POLE HAS 3 FLAT SIDES AT THE TIP.
POLES (A) SHOW A FLAT EITHER SIDE AND A FLAT ON THE FRONT. POLE (B) SHOWS THE SAME BUT IT SHOULDN'T AS THE POLE HAS BEEN ROTATED 90° LEFT OR RIGHT SO ONE OF THE SIDES SHOULDN'T SHOW A FLAT.
BECAUSE OF THIS WE CANNOT DETERMINE WHICH LAM (A) OR (B) THE POLES ARE IN ON THE DETAIL VIEW ABOVE SO DON'T KNOW WHICH SIDES TO APPLY THE MIN/MAX DIMENSIONS.

Rob Lonsdale.

POLE LENGTH	DIM Y
UP TO AND INCLUDING 12.0m	1600
13.0m TO 15.0m INCLUSIVE	1700
16.0m AND 17.0m	1900
18.0m	1900
20.0m	2500
22.0m	2500
24.0m	2500

NORTHERN POWERGRID		Lloyds Court, 78 Grey Street, Newcastle Upon Tyne, NE1 6AF	
Manufacturer Details		66KV SINGLE CIRCUIT OVERHEAD LINES DRILLING, SCARFING AND MARKING FOR STANDARD PORTAL TYPE POLE TO SPECIFICATION OHL 4/84	
Sheet No. 1	Scale 1:20	Type OVERHEAD	
Prepared By Jon Oakley		Ref No. C995423	
Revised 13/12/13		Grid Reference	
Date Issued 16/02/11		Checked By S SALKELD	
		Revision N	Notes
			POLES
			Historic Drg.No. 1091231187