


OUT OF LINE?

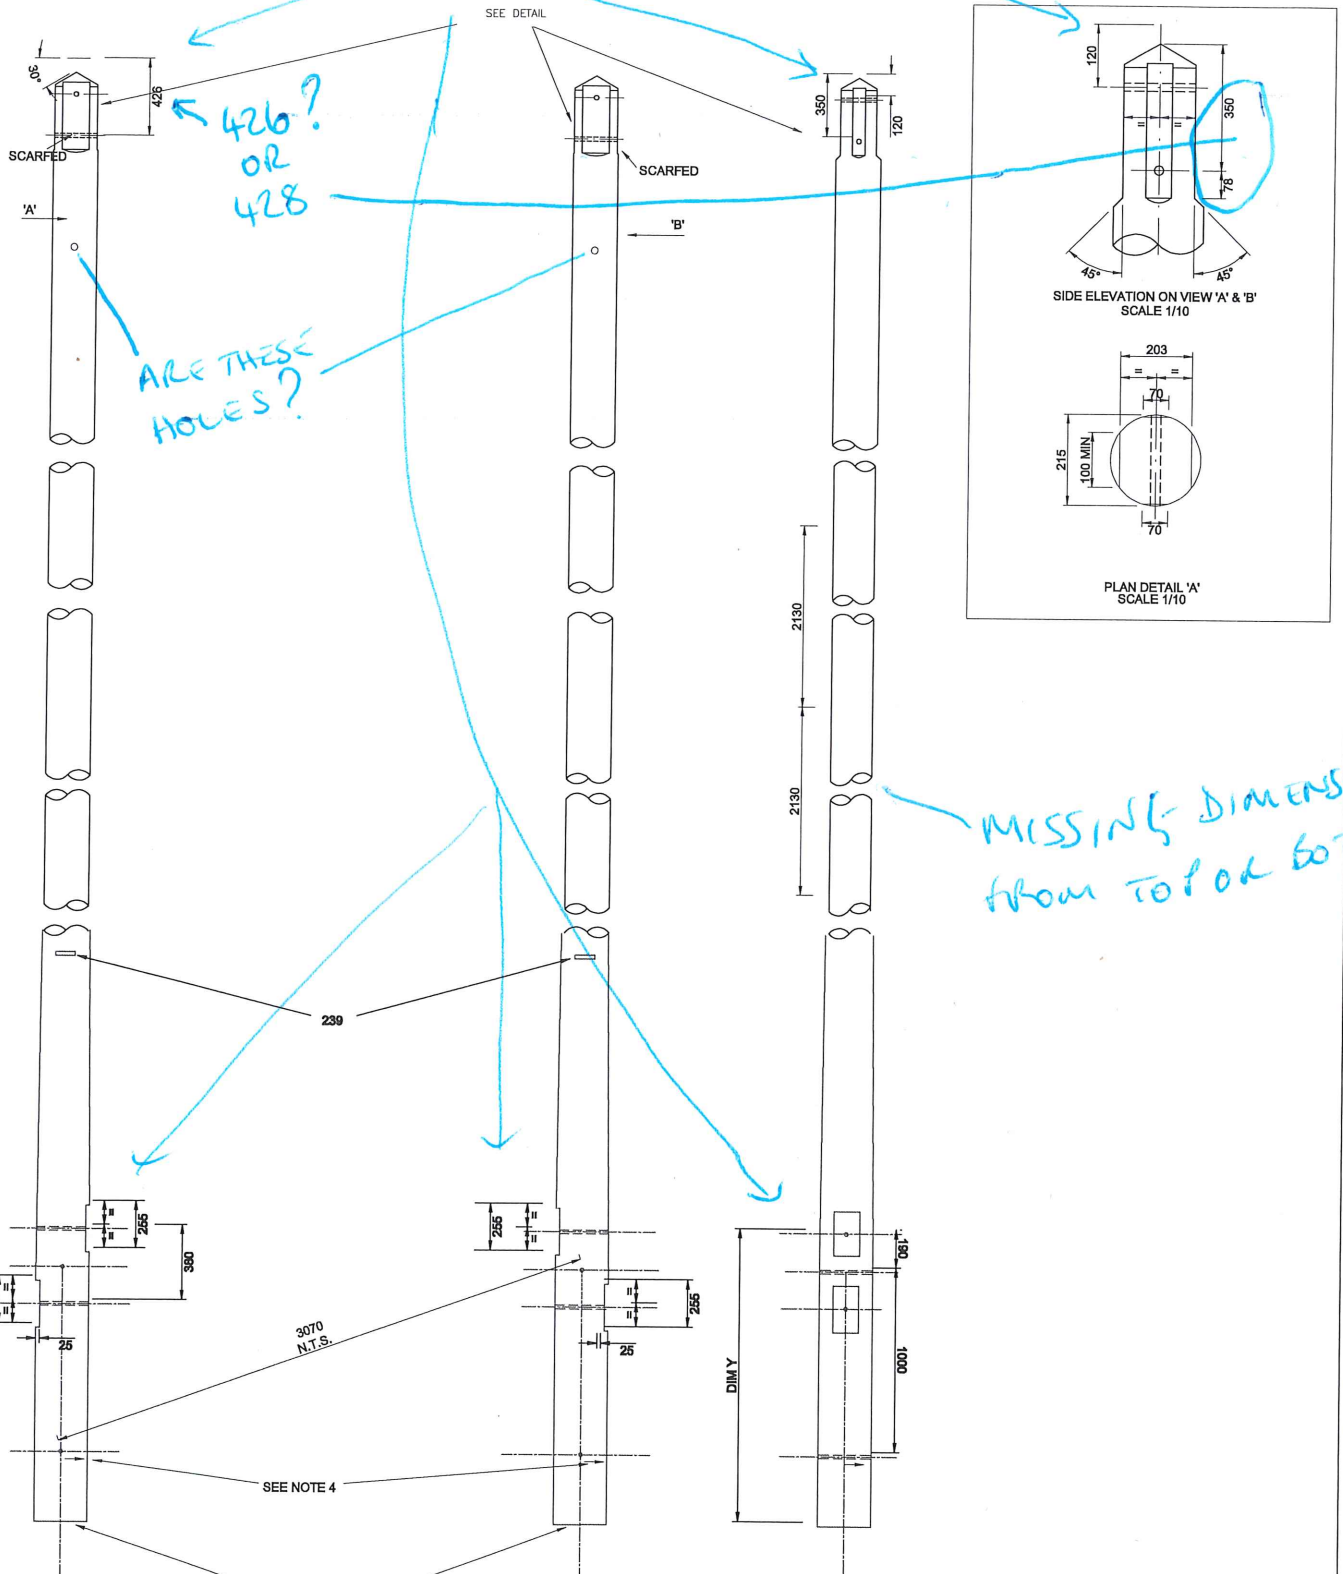

NOTES

- POLE LEGS TO BE MATCHED, POLE TOP MINIMUM DIAMETER BEFORE FABRICATION E/STOUT - 228mm.
- HOLES TO BE 22mm DIA. DRILLED AT RIGHT ANGLES TO VERTICAL CENTRE-LINE OF POLE. ALL DRILLING AND CUTTING TO BE DONE STRICTLY TO TEMPLATE PRIOR TO CREOSOTING.
- POLE BUTTS CUT AT RIGHT ANGLES TO AXIS OF POLE.
- 50x6x6 DEEP ARROW MARK POINTING TOWARDS OPPOSITE POLE LEG TO BE GOUGED ON BRACE BLOCK NOTCHING.

NOTE 5 MISSING

All dimensions shown are in millimetres unless stated otherwise

POLE LENGTH	DIM Y
UP TO AND INCLUDING 12.0m	1500
13.0m TO 15.0m INCLUSIVE	1700
16.0m AND 17.0m	1900
18.0m	1900
20.0m	2500
22.0m	2500
24.0m	2500

NORTHERN POWERGRID

Manufacturer Details

Sheet No. 2 Scale 1:20

Prepared By Joao Oakley

Revised 13/12/13

Date Issued 19/06/13

Grid Reference

Checked By G. HAMMEL

Lloyds Court, 78 Grey Street, Newcastle Upon Tyne, NE1 6AF

132KV SINGLE CIRCUIT OVERHEAD LINES
DRILLING, SCARFING & MARKING FOR
LARGE ANGLE 'H' POLE STRUCTURE

Type OVERHEAD

STANDARDS

Ref No. C1023988

Historic Drg. No.

1091390018

Revision A

Notes