


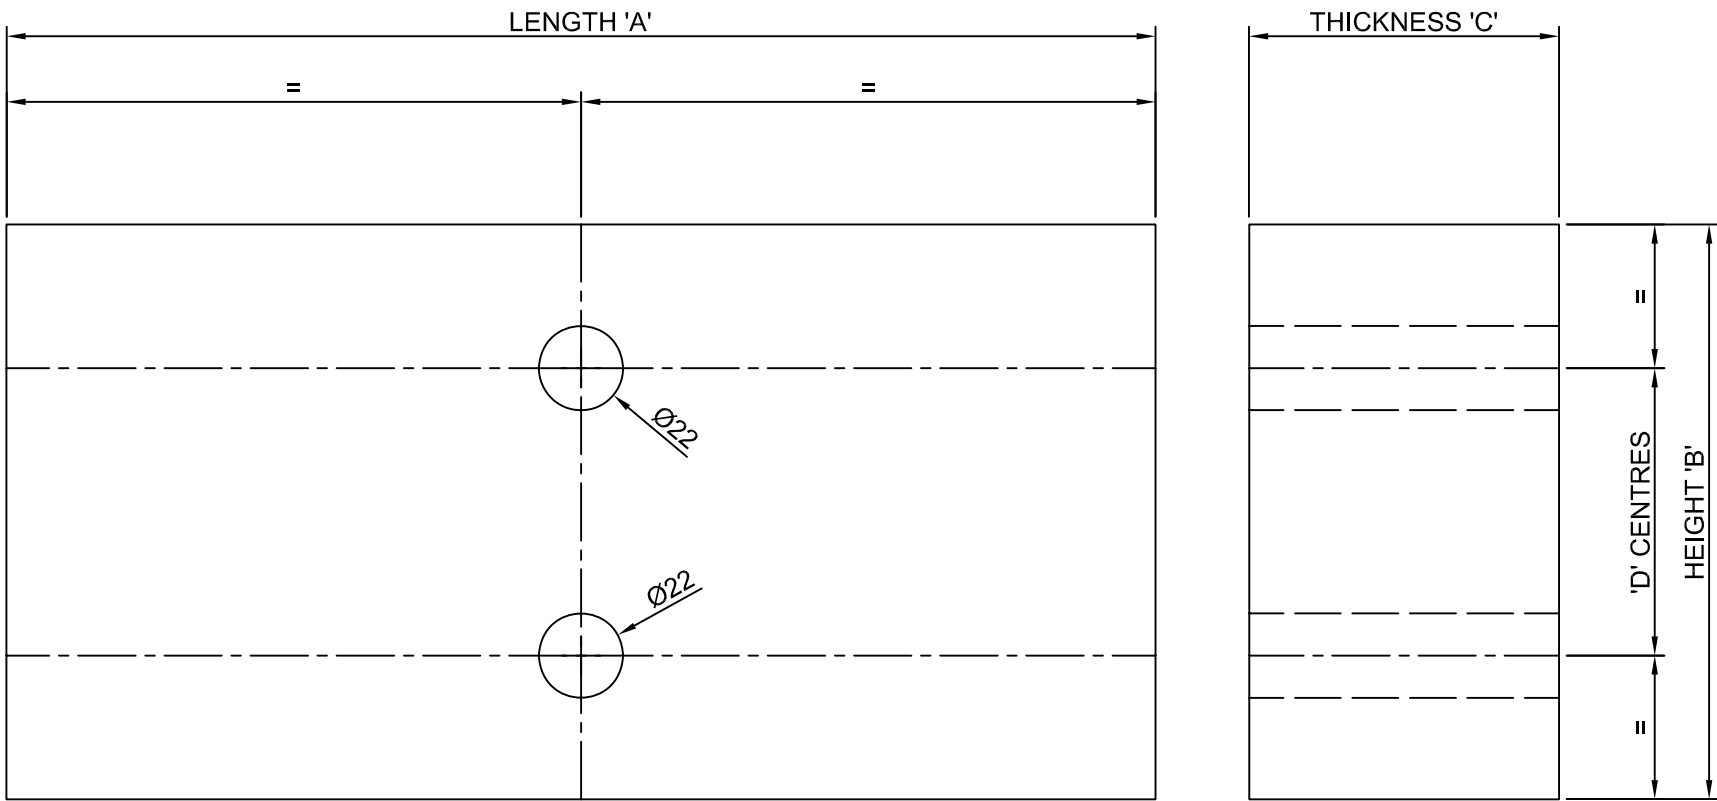

ITEM No.	LENGTH 'A'	HEIGHT 'B'	THICKNESS 'C'	'D' CENTRES
1	175	300	100	150
2	175	250	100	86
.	.	.	.	.
.	.	.	.	.
.	.	.	.	.
.	.	.	.	.
.	.	.	.	.
.	.	.	.	.
.	.	.	.	.

NOTES

- 1. TIMBER TO BE ENGLISH OAK.
- 2. BLOCKS TO BE CUT FROM SAWN TIMBER.
- 3. TIMBER GRAIN TO BE LONGITUDINALLY ALONG LENGTH 'A'.
- 4. LONGITUDINALLY CUT SURFACES TO BE STRAIGHT & CLEAN & ANNUALAR GROWTH RINGS SHALL BE APPROX. PARALLEL.

CE Electric UK		Lloyds Court, 78 Grey Street, Newcastle Upon Tyne, NE1 6AF			
Manufacturer Details		132kV OVERHEAD LINES RUTTER TYPE POLE SHEAR BLOCK SCHEDULE			
Sheet No. 30	Scale N.T.S.				
Prepared By TREVOR R. WILKIN		Type OVERHEAD		DOCUMENT_SUB_CLASS	
Revised 24/01/06	Grid Reference	Ref No.	62470B	Historic Drg.No.	1 09 101 0675
Date Issued 24/01/06	Checked By	Revision	Notes		