


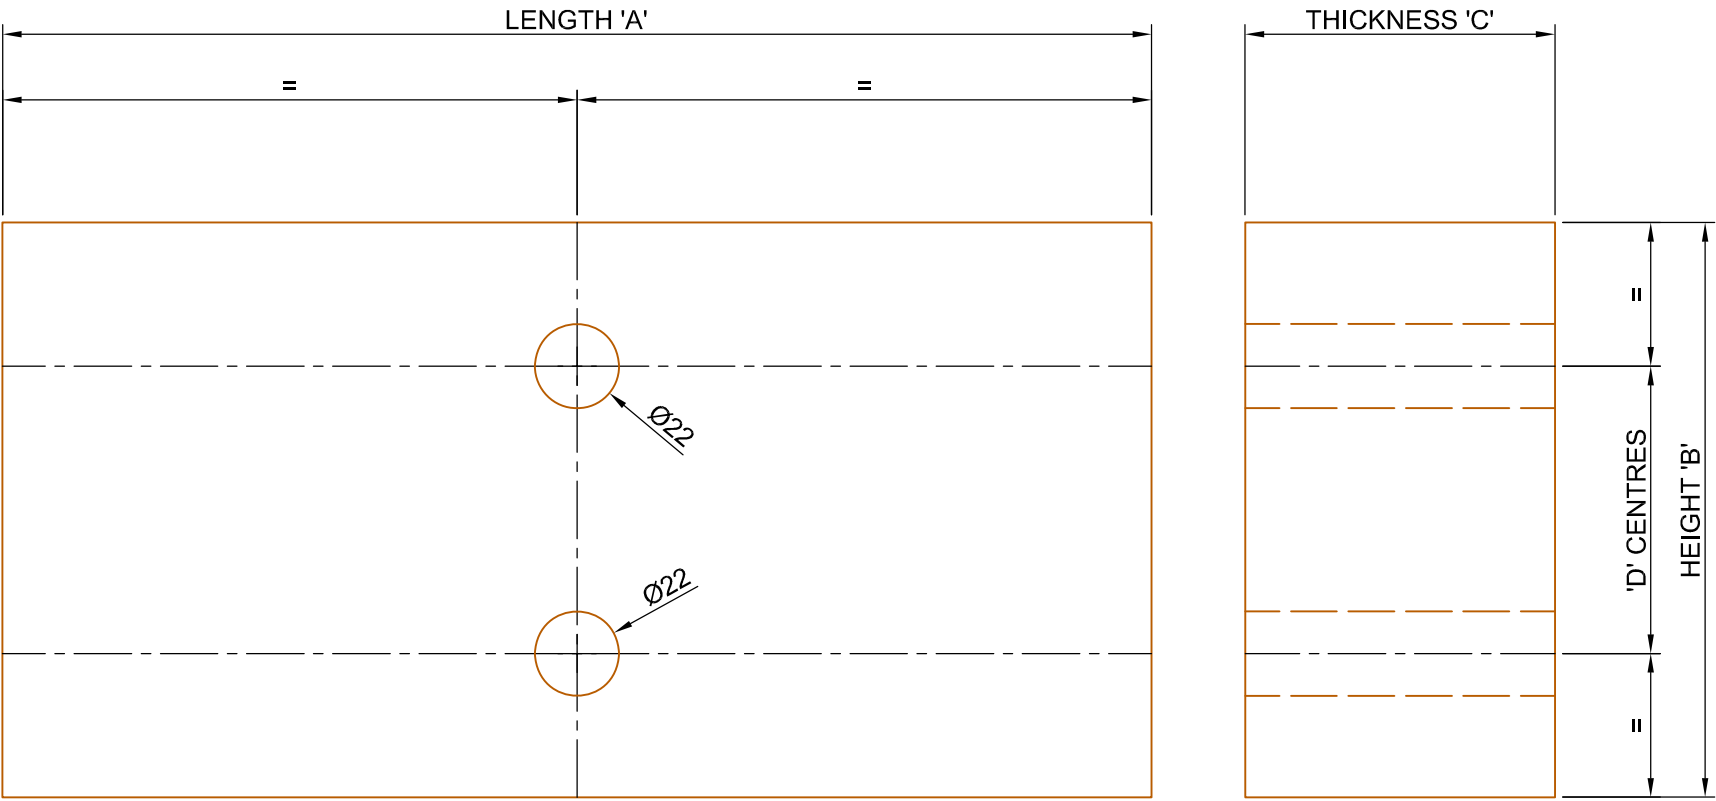

ITEM No.	LENGTH 'A'	HEIGHT 'B'	THICKNESS 'C'	'D' CENTRES	MATERIAL
1	175	300	100	150	ANGELIM PEDRA
2	175	250	100	86	ANGELIM PEDRA
3	1300	250	125	86	PINUS SYLVESTRIS
4	2500	250	125	86	PINUS SYLVESTRIS
.	.	.	.	.	.
.	.	.	.	.	.
.	.	.	.	.	.
.	.	.	.	.	.
.	.	.	.	.	.

NOTES

1. SEE MATERIAL COLUMN IN TABLE. A SUITABLE ALTERNATIVE MAY BE USED PROVIDED IT IS OF SUITABLE STRENGTH & DURABILITY.
2. BLOCKS TO BE CUT FROM SAWN TIMBER.
3. TIMBER GRAIN TO BE LONGITUDINALLY ALONG LENGTH 'A'.
4. LONGITUDINALLY CUT SURFACES TO BE STRAIGHT & CLEAN & ANNUALAR GROWTH RINGS SHALL BE APPROX. PARALLEL.

**CE Electric UK**

Manufacturer Details

Sheet No.
30

Scale
N.T.S.

Prepared By
TREVOR R. WILKIN

Revised
24/01/06

Date Issued
24/01/06

Grid Reference

Checked By
DAVE MARSHALL

Lloyds Court, 78 Grey Street, Newcastle Upon Tyne, NE1 6AF

132kV OVERHEAD LINES
RUTTER TYPE POLE
SHEAR BLOCK SCHEDULE

Type
OVERHEAD

DOCUMENT_SUB_CLASS

Ref No.
62470B

Historic
Drg.No.

1 09 101 0675

Revision 1Notes MATERIAL COLUMN & ITEMS 3 & 4 ADDED