

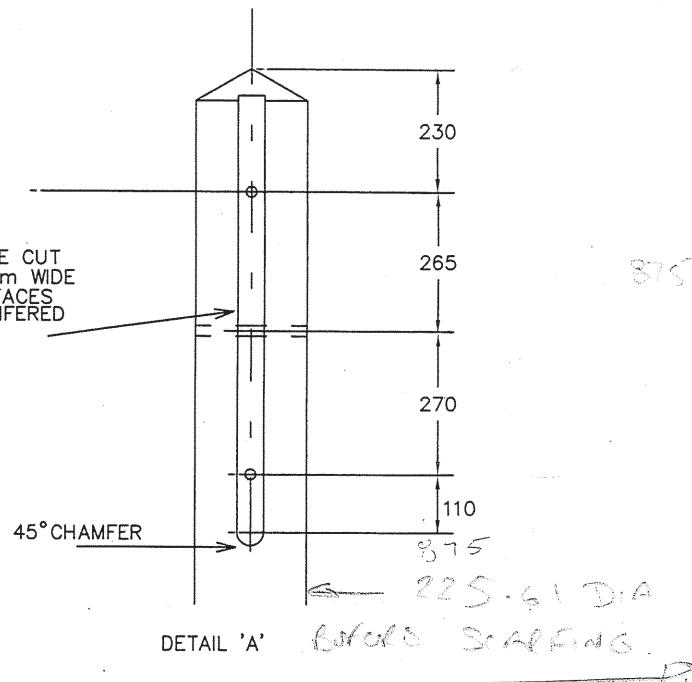
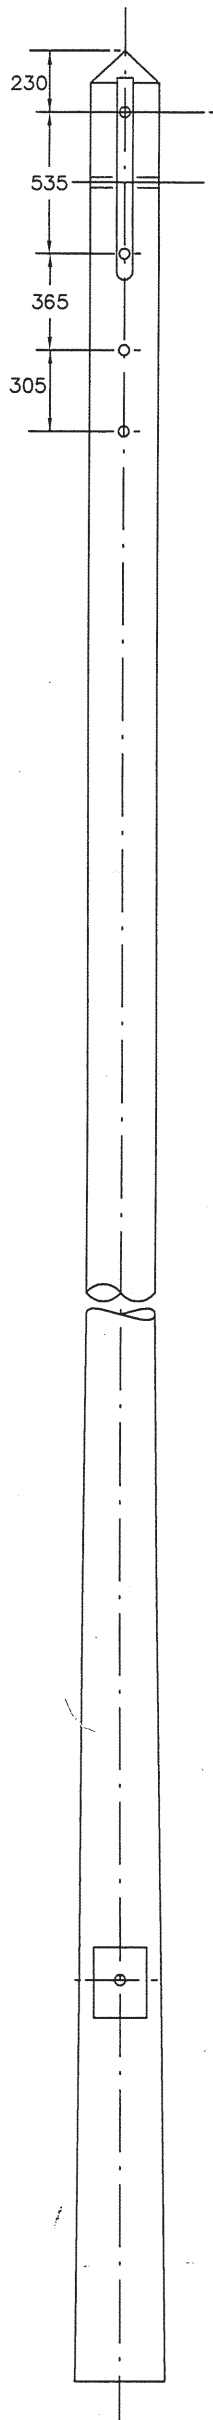


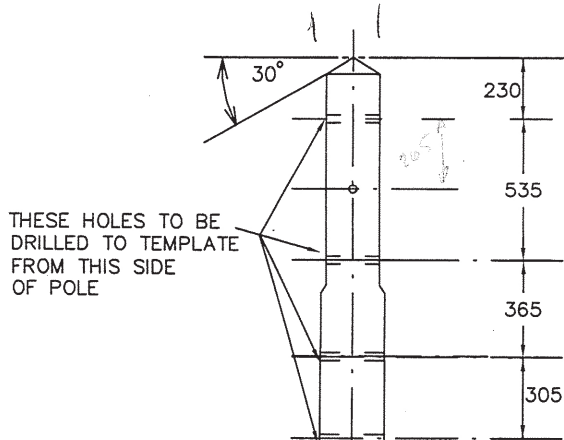

NOTES REFERRED TO

NOTES

1. CLASS OF POLE TO BE 'STOUT' OR EXTRA STOUT IN ACCORDANCE WITH 1.09.101.0238
2. POLE BUTT TO BE CUT AT RIGHT ANGLES TO AXIS OF POLE
3. ALL HOLES TO BE 22mm DIA. DRILLED AT RIGHT ANGLES TO VERTICAL CENTRE LINE OF POLE. ALL DRILLING AND CUTTING TO BE DONE STRICTLY TO TEMPLATE PRIOR TO CREOSOTING
4. POLE TO BE NOTCHED AND DRILLED FOR
1 x 250 x 125 x 2500 AND
1 x 250 x 125 x 1300 LONG BAULKS
5. EXTRA STOUT POLES TO BE NORMALLY FITTED WITH DOUBLE BAULKS. EXTRA STOUT POLES DESIGNED TO INCREASE WIND SPANS MAY BE UNSUITABLE FOR POOR GROUND CONDITIONS. SEE SPECIFICATION.

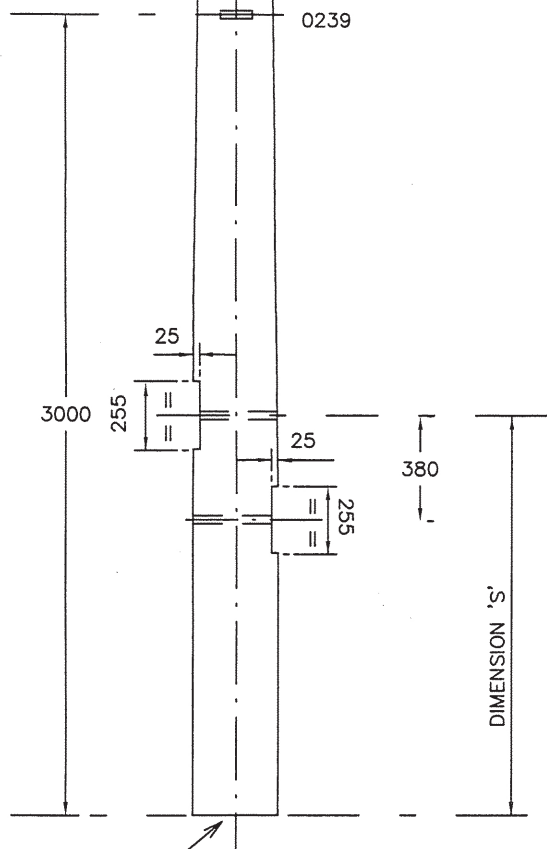

POLE LENGTH/ CLASS TO BE IMPRESSED ON POLE BUTT

THIS VIEW SHOWS THE POLE FACE (NATURAL LIE OF POLE.)

POLE LENGTH	DIM. 'S'
8.5m - 12m INCLUSIVE	1.5
13.0m - 15.0m INCLUSIVE	1.7
16.0m - 18.0m INCLUSIVE	1.9
20.0m - 24m INCLUSIVE	2.5

ALL DIMENSIONS SHOWN ARE IN MILLIMETRES UNLESS OTHERWISE STATED

NEDL

Prepared by J.L.W.
Checked M.M. Date Issued AUG 99

NEDL, Manor House, Station Road, Houghton le Spring, DH4 7LA.

132kV SINGLE CIRCUIT OVERHEAD LINES
DRILLING, SCARFING AND MARKINGS
FOR SINGLE INTERMEDIATE POLE ARRANGEMENT

Drg.No. 1 09 138 0006

Sheet No. 2
Revised
Scale 1:20 & 10

1-00-138-002