


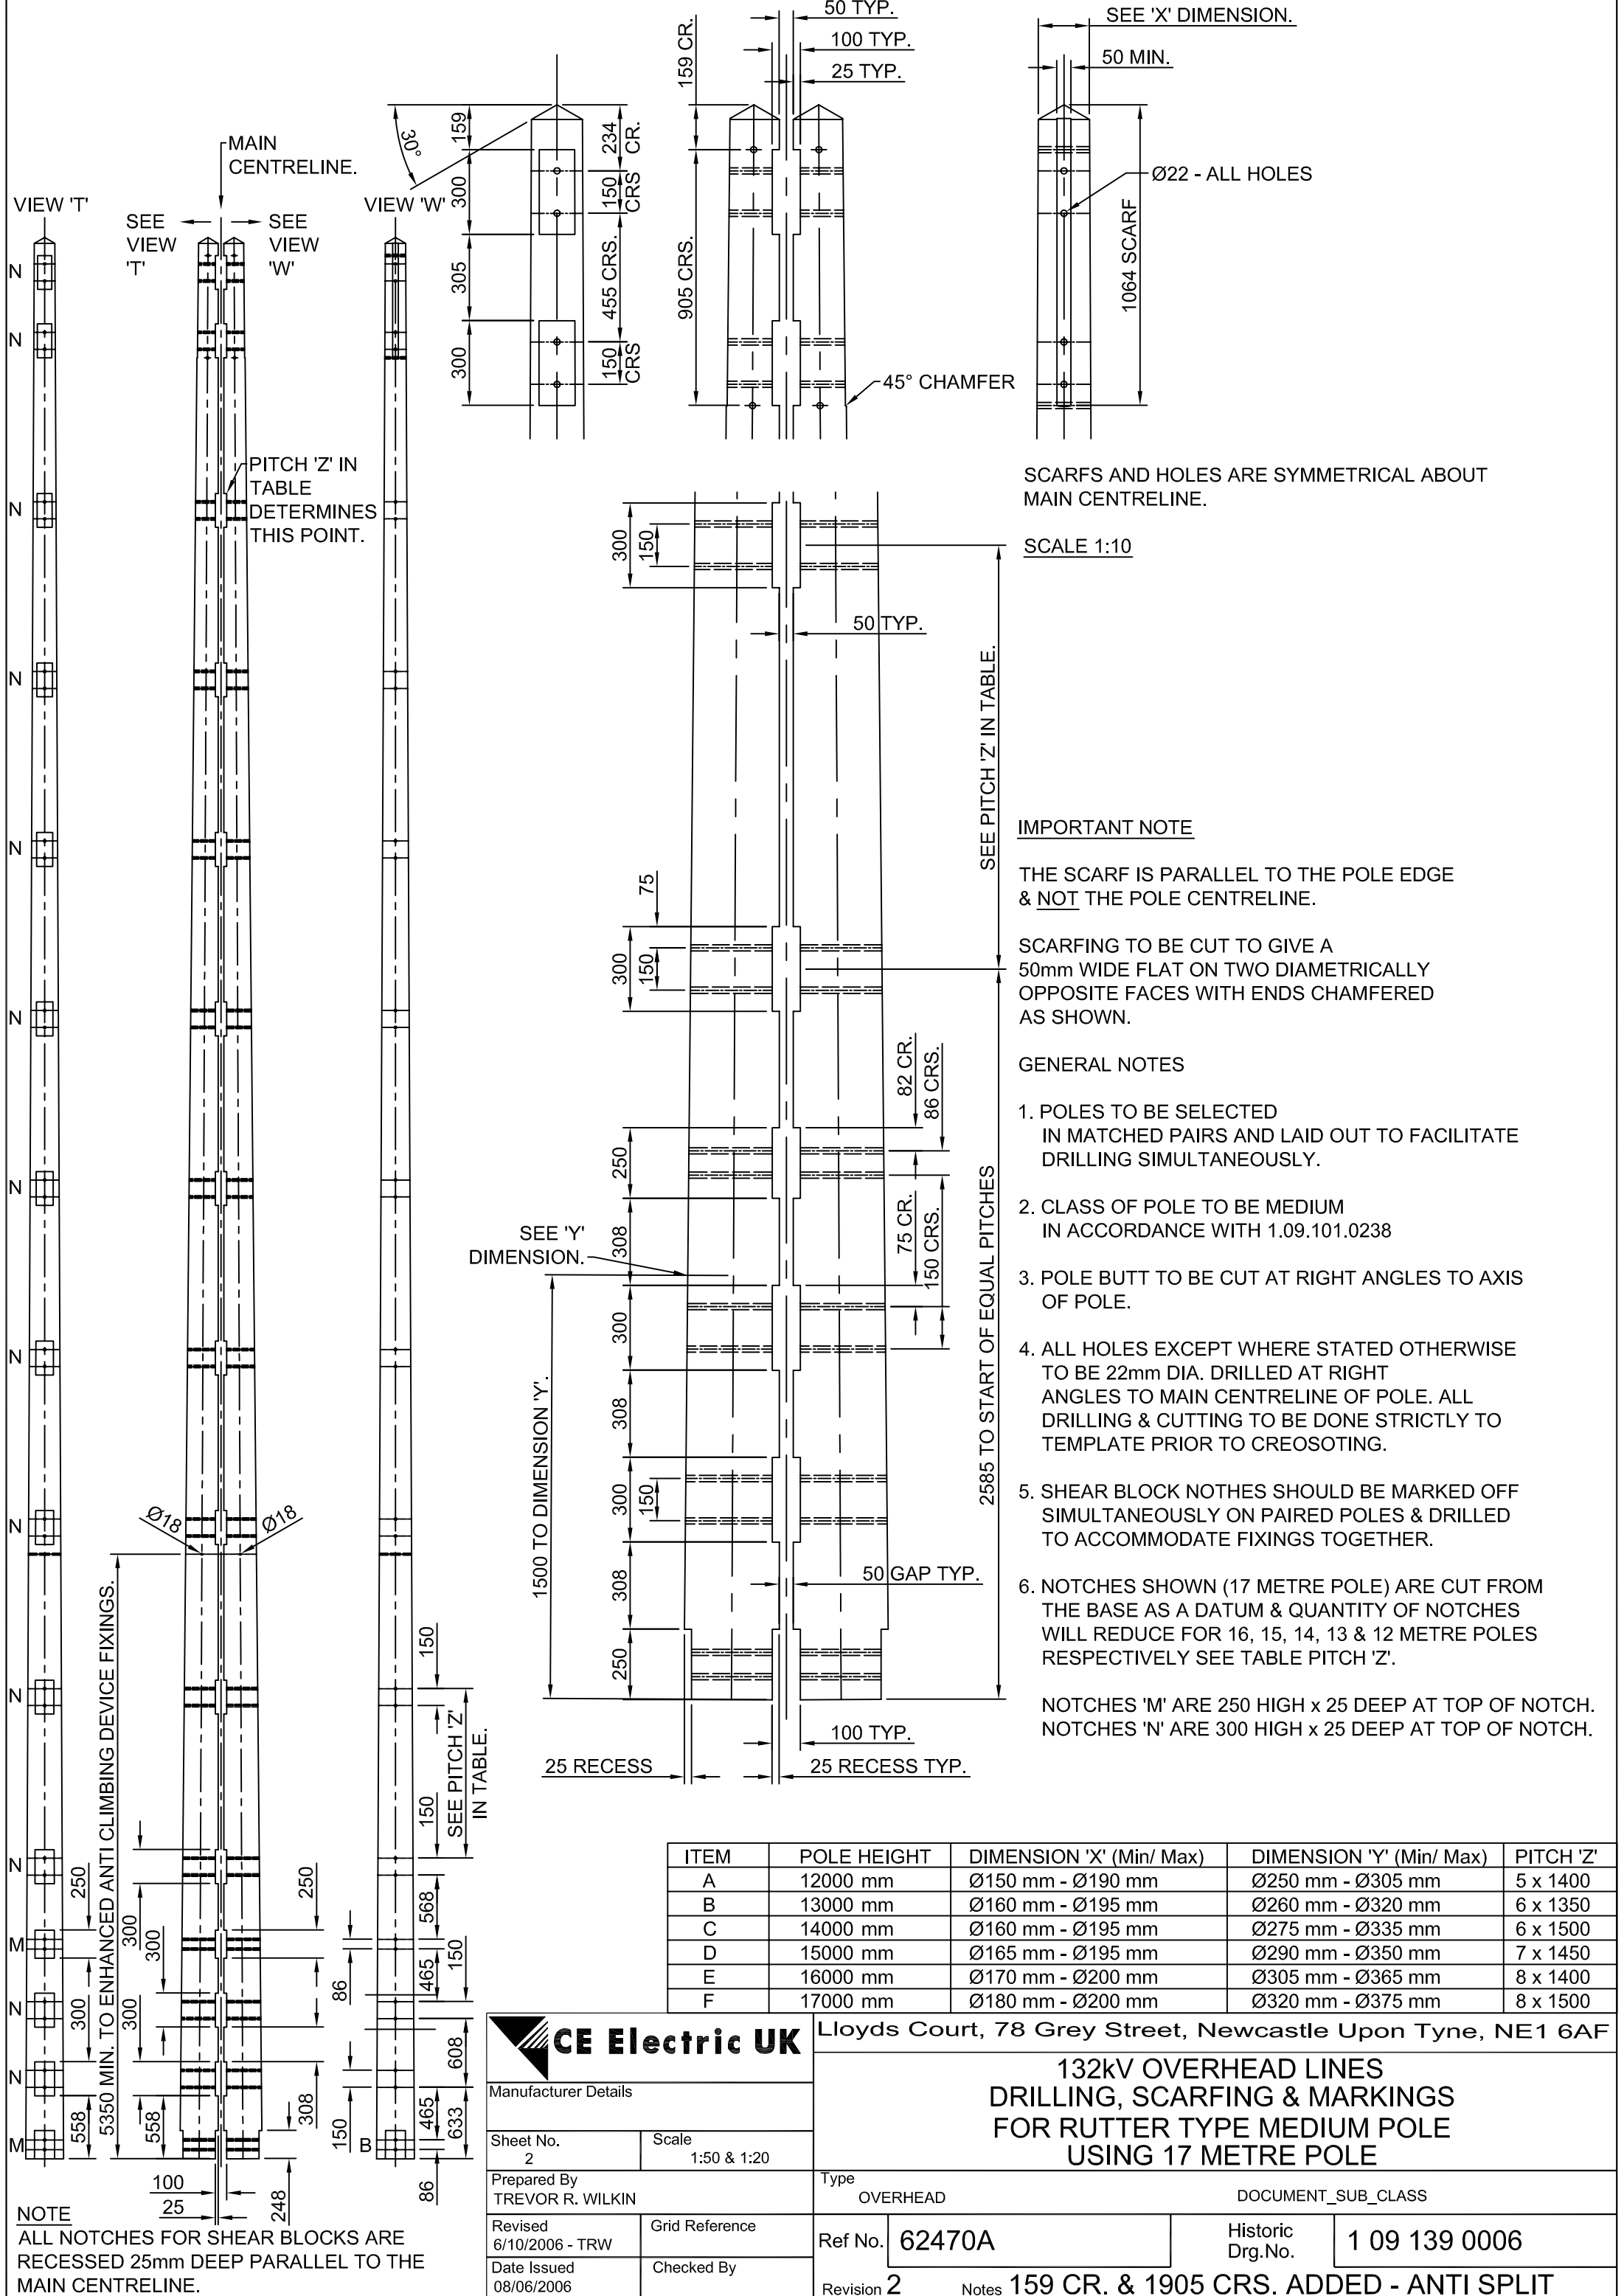

SCARFS AND HOLES ARE SYMMETRICAL ABOUT MAIN CENTRELINE.

SCALE 1:10

IMPORTANT NOTE

THE SCARF IS PARALLEL TO THE POLE EDGE & NOT THE POLE CENTRELINE.

SCARFING TO BE CUT TO GIVE A 50mm WIDE FLAT ON TWO DIAMETRICALLY OPPOSITE FACES WITH ENDS CHAMFERED AS SHOWN.

GENERAL NOTES

1. POLES TO BE SELECTED IN MATCHED PAIRS AND LAID OUT TO FACILITATE DRILLING SIMULTANEOUSLY.
2. CLASS OF POLE TO BE MEDIUM IN ACCORDANCE WITH 1.09.101.0238
3. POLE BUTT TO BE CUT AT RIGHT ANGLES TO AXIS OF POLE.
4. ALL HOLES EXCEPT WHERE STATED OTHERWISE TO BE 22mm DIA. DRILLED AT RIGHT ANGLES TO MAIN CENTRELINE OF POLE. ALL DRILLING & CUTTING TO BE DONE STRICTLY TO TEMPLATE PRIOR TO CREOSOTING.
5. SHEAR BLOCK NOTHES SHOULD BE MARKED OFF SIMULTANEOUSLY ON PAIRED POLES & DRILLED TO ACCOMMODATE FIXINGS TOGETHER.
6. NOTCHES SHOWN (17 METRE POLE) ARE CUT FROM THE BASE AS A DATUM & QUANTITY OF NOTCHES WILL REDUCE FOR 16, 15, 14, 13 & 12 METRE POLES RESPECTIVELY SEE TABLE PITCH 'Z'.

NOTCHES 'M' ARE 250 HIGH x 25 DEEP AT TOP OF NOTCH. NOTCHES 'N' ARE 300 HIGH x 25 DEEP AT TOP OF NOTCH.

ITEM	POLE HEIGHT	DIMENSION 'X' (Min/ Max)	DIMENSION 'Y' (Min/ Max)	PITCH 'Z'
A	12000 mm	Ø150 mm - Ø190 mm	Ø250 mm - Ø305 mm	5 x 1400
B	13000 mm	Ø160 mm - Ø195 mm	Ø260 mm - Ø320 mm	6 x 1350
C	14000 mm	Ø160 mm - Ø195 mm	Ø275 mm - Ø335 mm	6 x 1500
D	15000 mm	Ø165 mm - Ø195 mm	Ø290 mm - Ø350 mm	7 x 1450
E	16000 mm	Ø170 mm - Ø200 mm	Ø305 mm - Ø365 mm	8 x 1400
F	17000 mm	Ø180 mm - Ø200 mm	Ø320 mm - Ø375 mm	8 x 1500

	
Manufacturer Details	
Sheet No. 2	Scale 1:50 & 1:20
Prepared By TREVOR R. WILKIN	
Revised 6/10/2006 - TRW	Grid Reference
Date Issued 08/06/2006	Checked By

Lloyds Court, 78 Grey Street, Newcastle Upon Tyne, NE1 6AF			
132kV OVERHEAD LINES DRILLING, SCARFING & MARKINGS FOR RUTTER TYPE MEDIUM POLE USING 17 METRE POLE			
Type OVERHEAD	DOCUMENT_SUB_CLASS		
Ref No. 62470A	Historic Drg.No.	1 09 139 0006	
Revision 2	Notes	159 CR. & 1905 CRS. ADDED - ANTI SPLIT	

NOTE
ALL NOTCHES FOR SHEAR BLOCKS ARE RECESSED 25mm DEEP PARALLEL TO THE MAIN CENTRELINE.