


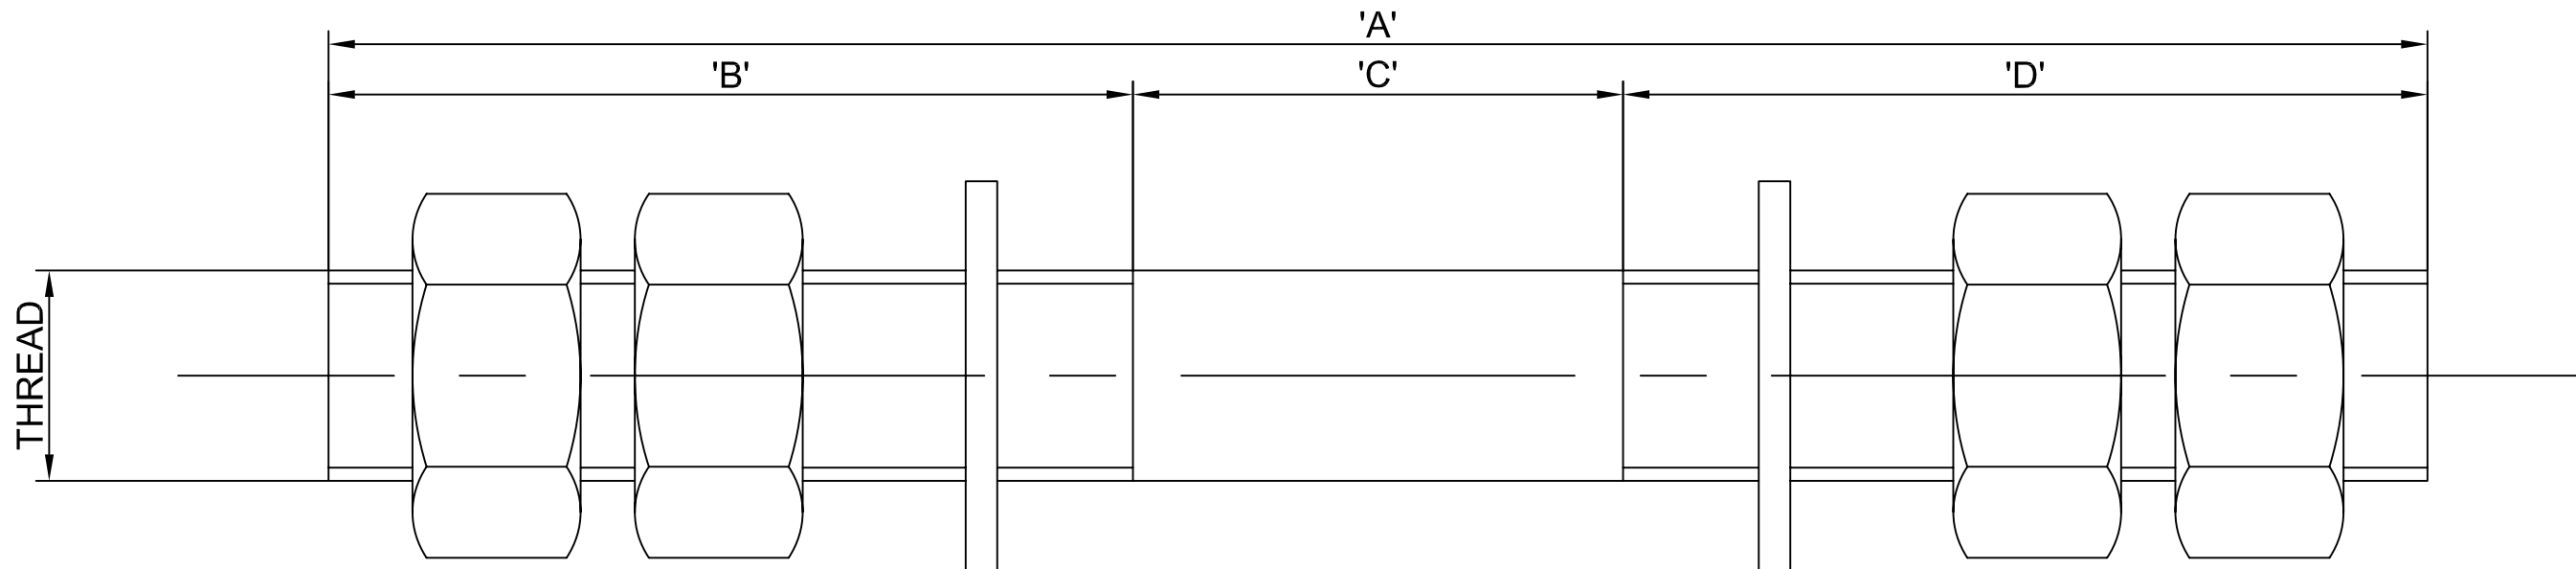

ITEM No.	THREAD	'A'	'B'	'C'	'D'
1	M20	1050	125	800	125
2	M20	850	125	600	125
3	M20	800	225	350	225
4	M20	310	70	170	70
5	M20	700	250	200	250
.	.	.	.	.	.

NOTES

1. TIE ROD MATERIAL: STEEL TO B.S. 4190, STRENGTH GRADE DESIGNATION 4.6 & SHALL MEET REQUIREMENTS AS SHOWN IN B.S. 4190 TABLE 14.
2. TIE RODS SHALL BE SUPPLIED WITH FOUR FULL NUTS TO B.S. 4190 & TWO PLAIN WASHERS TO B.S. 4320.
3. ALL ITEMS SHALL BE GALVANISED TO B.S. 729 AFTER FABRICATION.

 CE Electric UK Manufacturer Details		Lloyds Court, 78 Grey Street, Newcastle Upon Tyne, NE1 6AF			
		OVERHEAD LINES M20 TIE ROD SCHEDULE			
		Sheet No. 29	Scale N.T.S.		
Prepared By TREVOR R. WILKIN		Type OVERHEAD		DOCUMENT_SUB_CLASS	
Revised	Grid Reference	Ref No.	C730115	Historic Drg.No.	1 09 101 0675
Date Issued 08/06/2006	Checked By	Revision	Notes		