
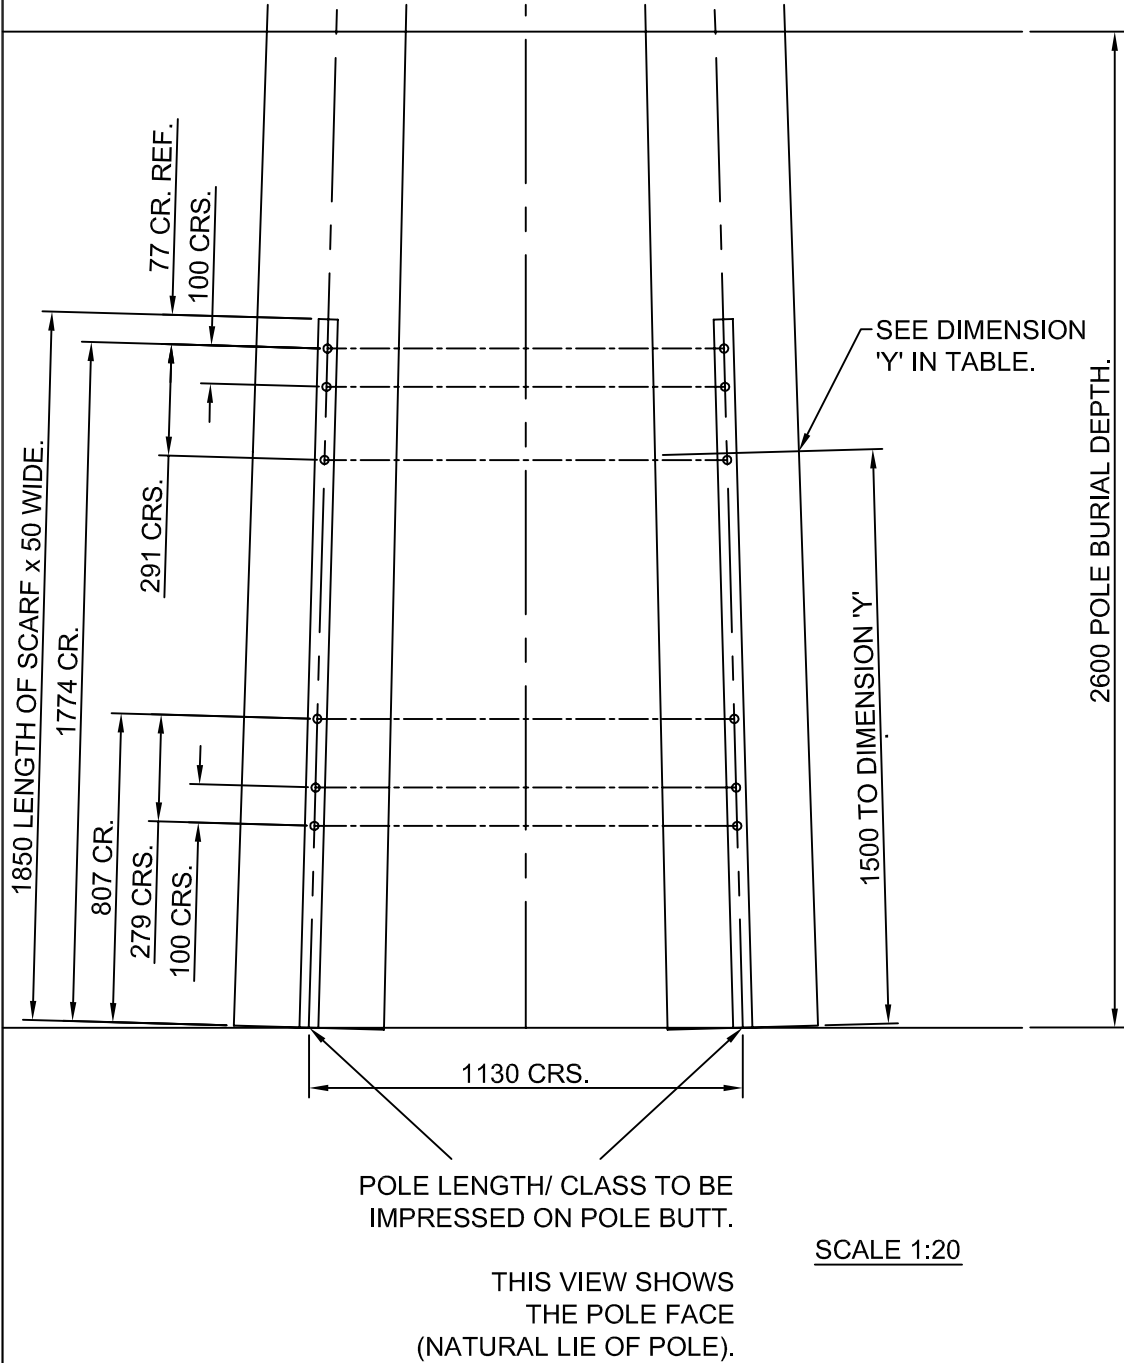


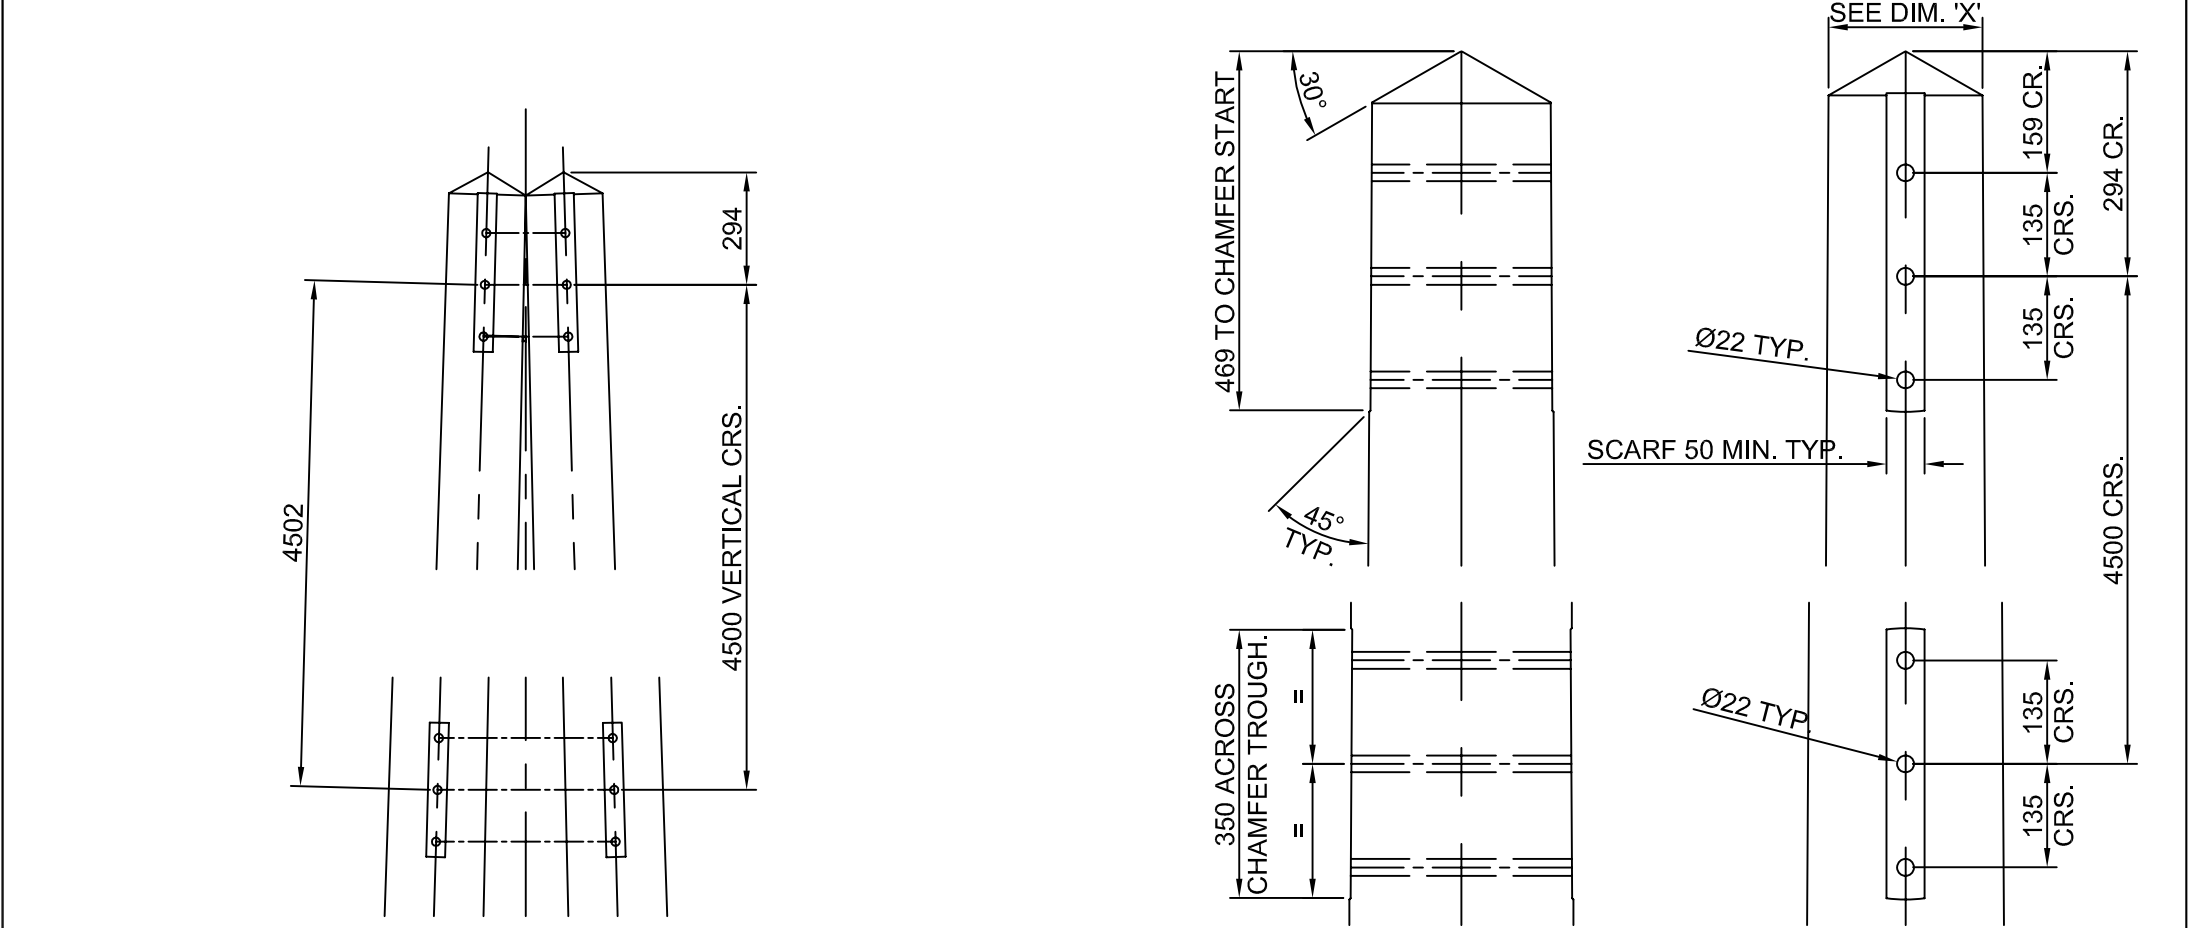

SCARFS AND HOLES ARE SYMMETRICAL ABOUT INDIVIDUAL POLE CENTRELINE.

ENLARGED VIEWS OF POLE APEX SCARF AND CHEEK PLATE SCARF ON 4500 CENTRES BELOW AS DRAWN.

ON THE ABOVE VIEWS ONLY.
NOTE THE POLE ELEVATIONS AND DIMENSIONS ARE DRAWN UP WITH POLE VERTICAL CENTRELINE AXIS.

SCALE 1:10

- IMPORTANT NOTE**
- THE SCARFE IS PARALLEL TO THE POLE EDGE & NOT THE POLE CENTRELINE.
- SCARFING TO BE CUT TO GIVE A 50mm WIDE FLAT ON TWO DIAMETRICALLY OPPOSITE FACES WITH ENDS CHAMFERED AS SHOWN.
- GENERAL NOTES
1. IDEALLY POLES SHOULD BE SELECTED IN MATCHED PAIRS AND LAID OUT TO FACILITATE DRILLING SIMULTANEOUSLY.
 2. CLASS OF POLE TO BE MEDIUM IN ACCORDANCE WITH 1.09.101.0238
 3. POLE BUTT TO BE CUT AT RIGHT ANGLES TO AXIS OF POLE.
 4. ALL HOLES TO BE 22mm DIA. DRILLED AT RIGHT ANGLES TO VERTICAL CENTRELINE OF POLE. ALL DRILLING & CUTTING TO BE DONE STRICTLY TO TEMPLATE PRIOR TO CREOSOTING.

ITEM	POLE HEIGHT	DIMENSION 'X' (Min/ Max)	DIMENSION 'Y' (Min/ Max)
A	12000 mm	Ø150 mm - Ø190 mm	Ø250 mm - Ø305 mm
B	13000 mm	Ø160 mm - Ø195 mm	Ø260 mm - Ø320 mm
C	14000 mm	Ø160 mm - Ø195 mm	Ø275 mm - Ø335 mm
D	15000 mm	Ø165 mm - Ø195 mm	Ø290 mm - Ø350 mm
E	16000 mm	Ø170 mm - Ø200 mm	Ø305 mm - Ø365 mm
F	17000 mm	Ø180 mm - Ø200 mm	Ø320 mm - Ø375 mm

		Lloyds Court, 78 Grey Street, Newcastle Upon Tyne, NE1 6AF	
Manufacturer Details		132kV OVERHEAD LINES DRILLING, SCARFING & MARKINGS FOR 'A' FRAME POLE (MEDIUM CLASS POLE)	
Sheet No. 2	Scale 1:20 & 1:10	Type OVERHEAD	DOCUMENT_SUB_CLASS
Prepared By TREVOR R. WILKIN	Grid Reference	Ref No. 62470A	Historic Drg.No. 1 09 139 0001
Revised	Checked By	Revision	Notes
Date Issued 24/06/2006			