


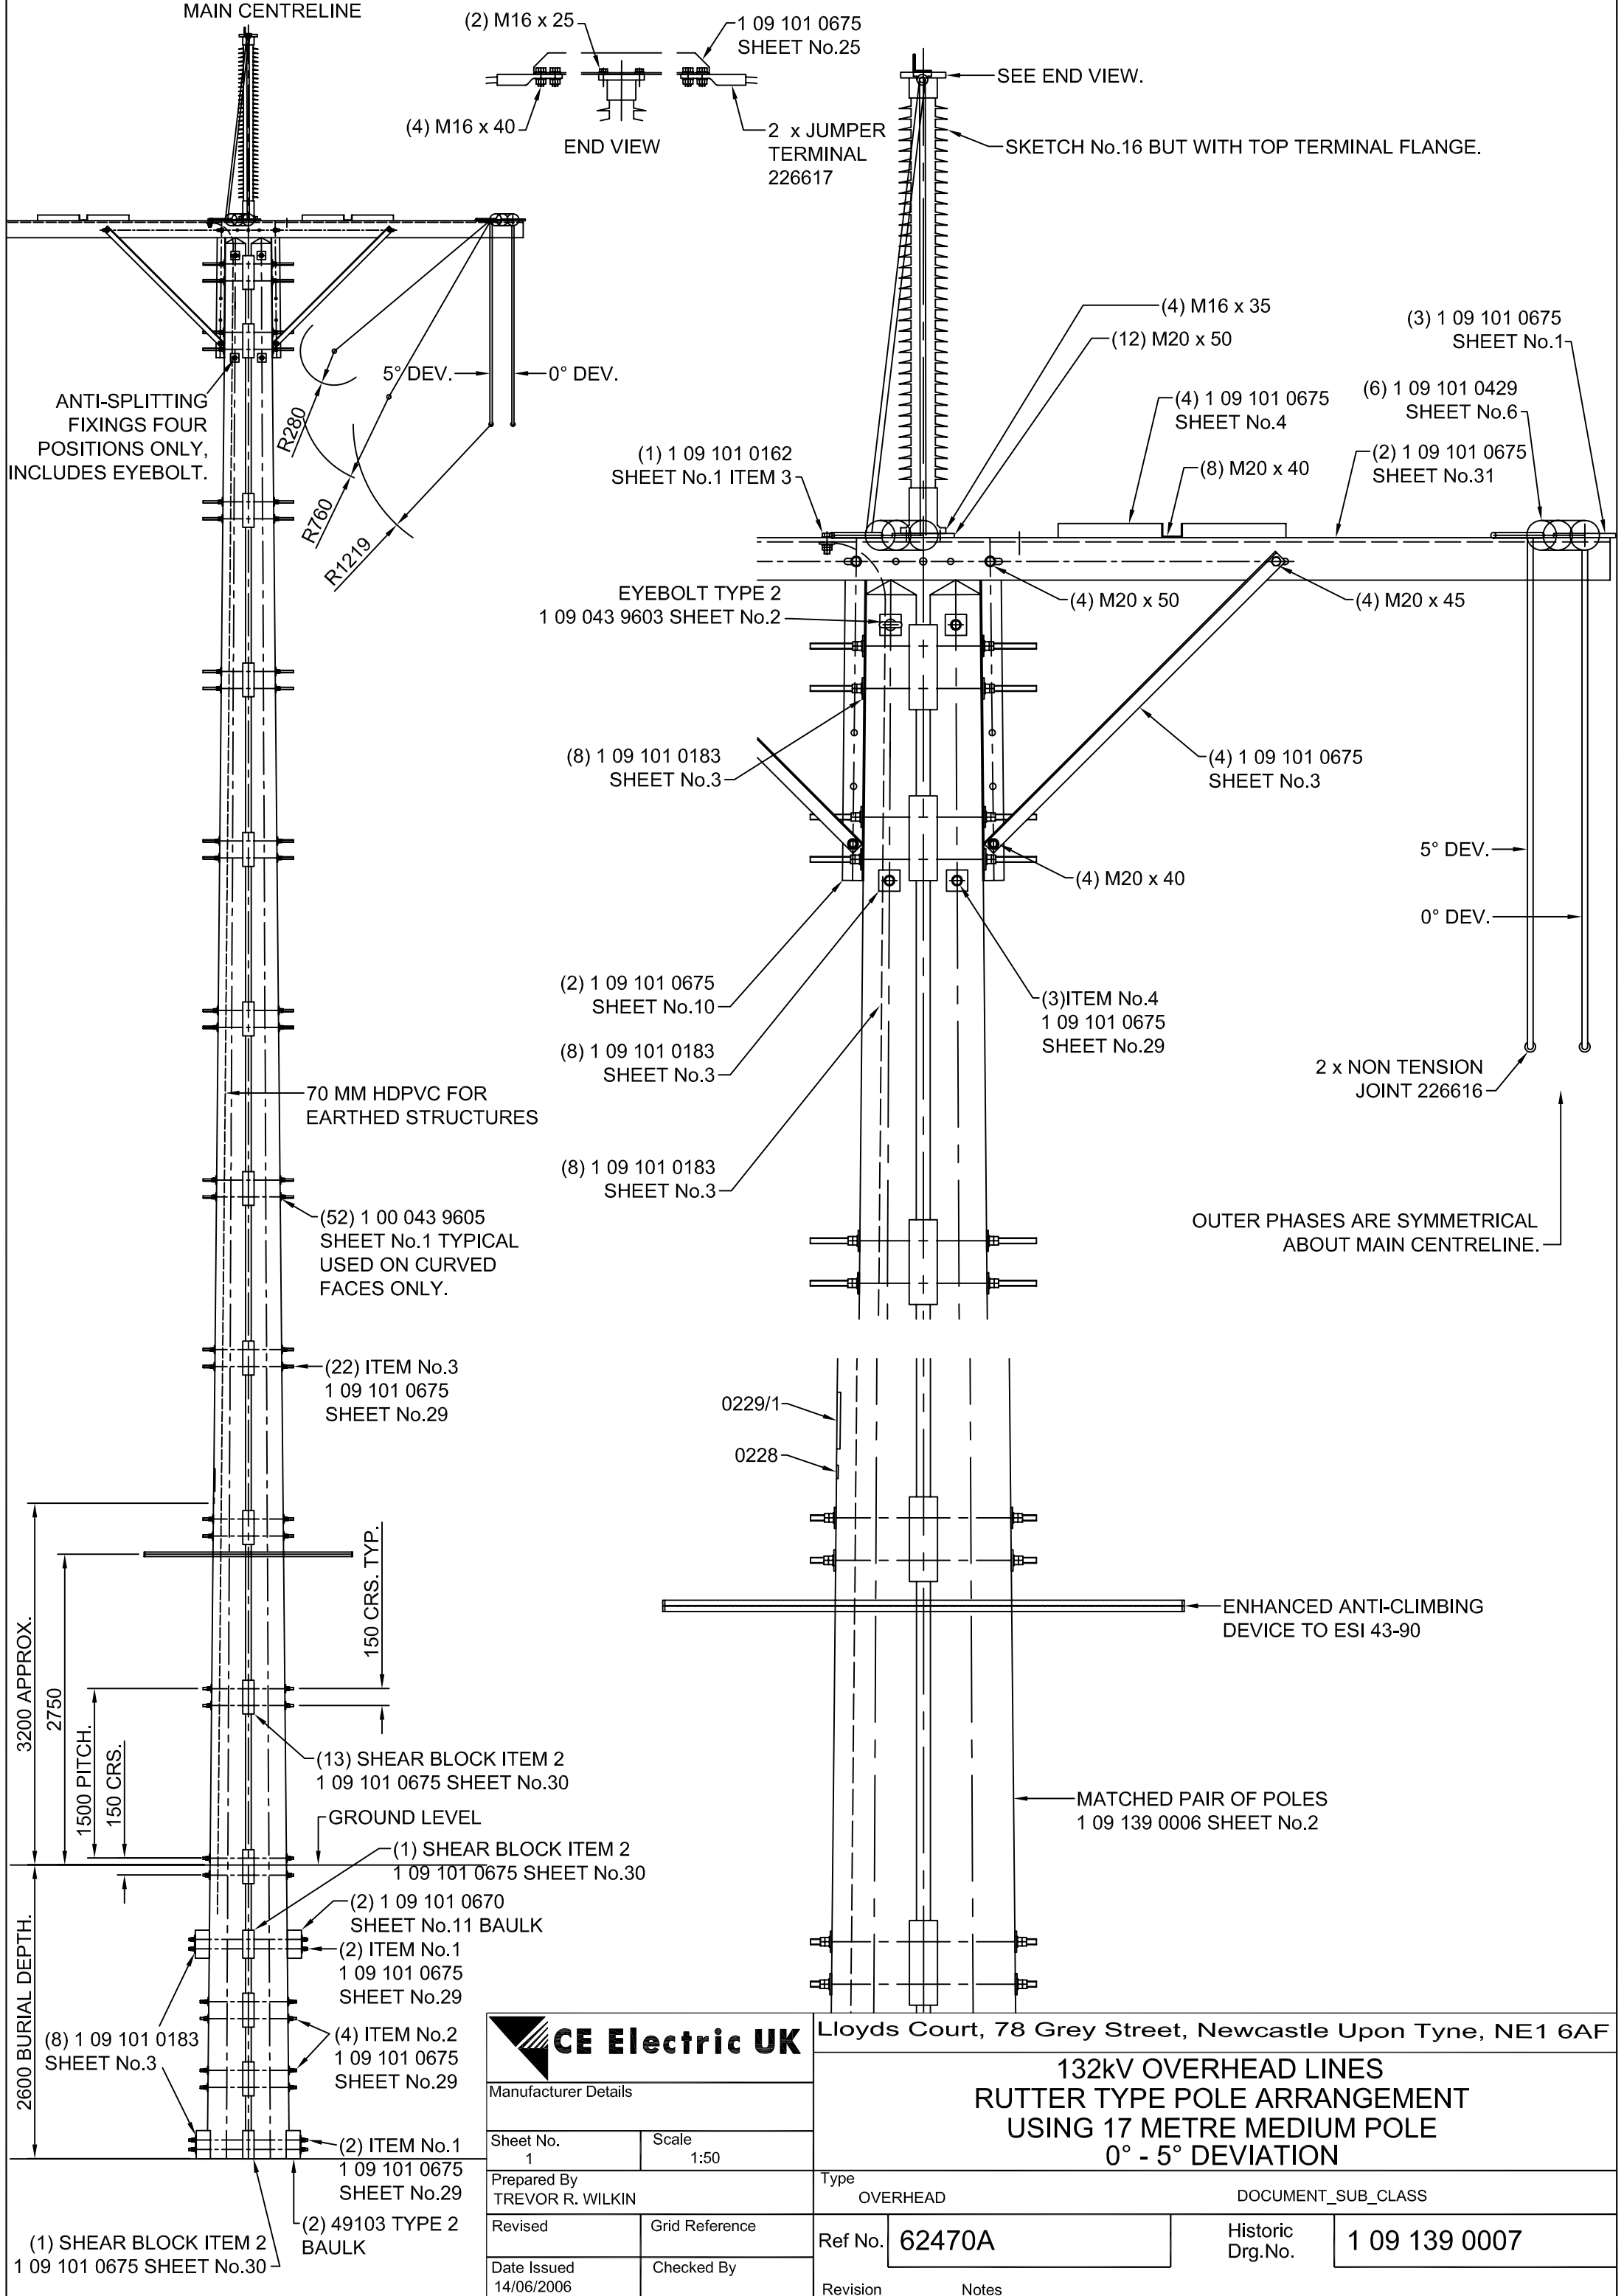

Manufacturer Details	
Sheet No. 1	Scale 1:50
Prepared By TREVOR R. WILKIN	
Revised	Grid Reference
Date Issued 14/06/2006	Checked By

Lloyds Court, 78 Grey Street, Newcastle Upon Tyne, NE1 6AF			
132kV OVERHEAD LINES RUTTER TYPE POLE ARRANGEMENT USING 17 METRE MEDIUM POLE 0° - 5° DEVIATION			
Type	DOCUMENT_SUB_CLASS		
OVERHEAD			
Ref No.	62470A	Historic Drg.No.	1 09 139 0007
Revision	Notes		