
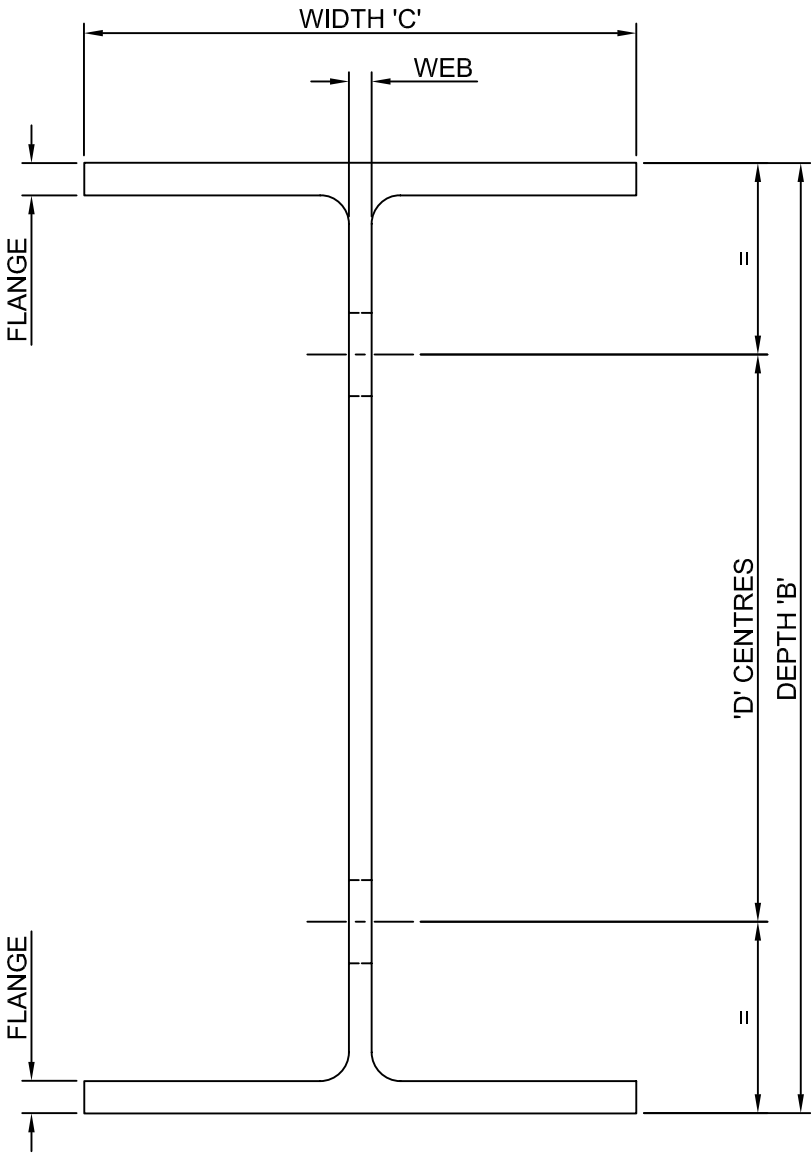


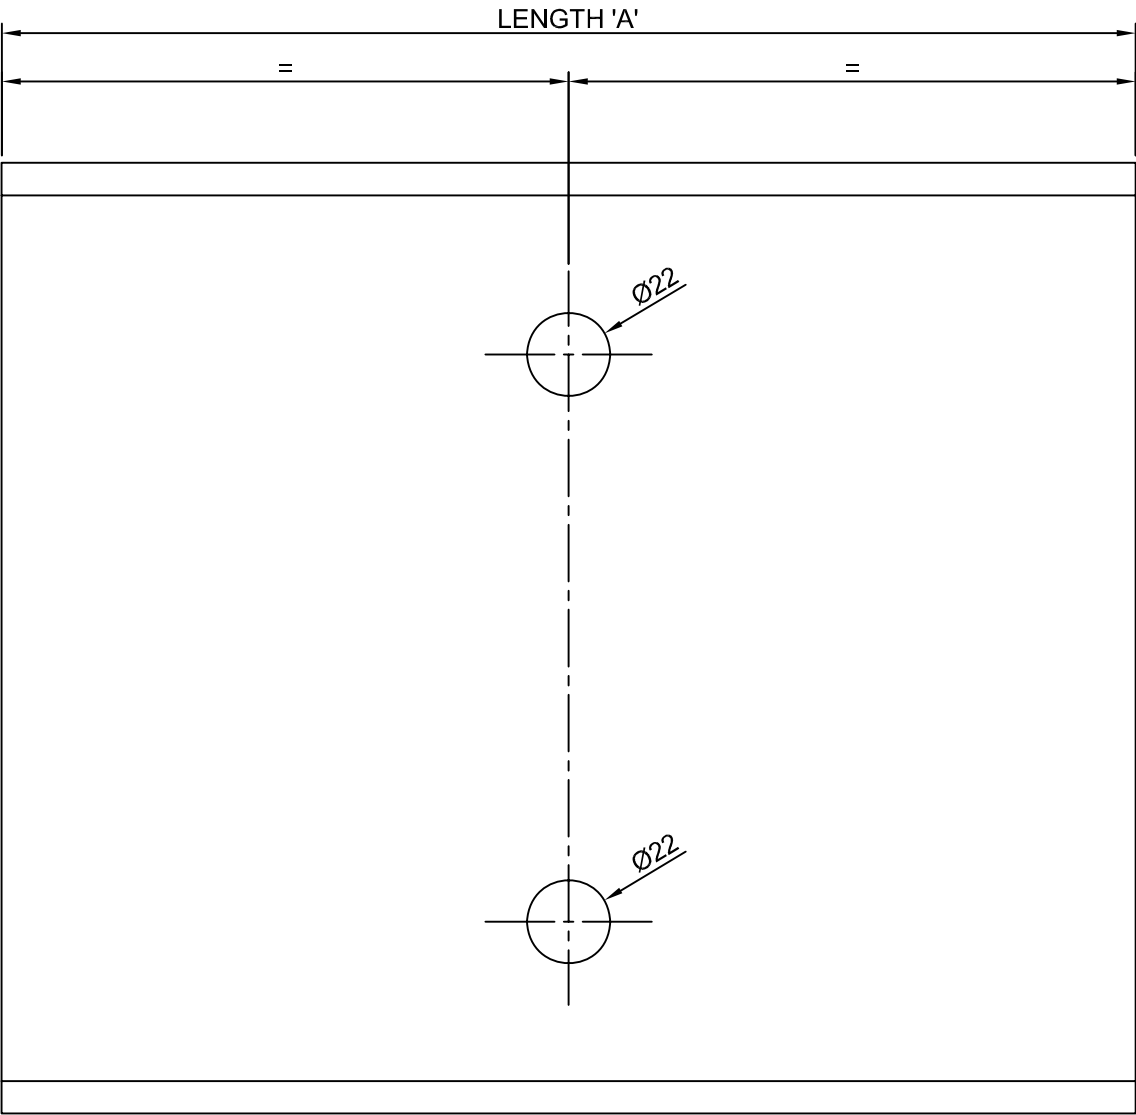

ITEM No.	LENGTH 'A'	DEPTH 'B'	WIDTH 'C'	'D' CENTRES	WEB	FLANGE	MATERIAL
1	270	251.4	146.1	150	6.0	8.6	UNIVERSAL BEAM STEEL 254x146x31kg/m
.	.	.	.	.	.	.	.
.	.	.	.	.	.	.	.
.	.	.	.	.	.	.	.
.	.	.	.	.	.	.	.
.	.	.	.	.	.	.	.
.	.	.	.	.	.	.	.
.	.	.	.	.	.	.	.
.	.	.	.	.	.	.	.

NOTES

1. ALL DIMENSIONS ARE IN MILLIMETRES.

CE Electric UK		Lloyds Court, 78 Grey Street, Newcastle Upon Tyne, NE1 6AF			
Manufacturer Details		132kV OVERHEAD LINES RUTTER TYPE POLE SHEAR BLOCK SCHEDULE			
Sheet No. 36	Scale N.T.S.				
Prepared By		Type OVERHEAD		DOCUMENT_SUB_CLASS	
Revised	Grid Reference	Ref No.	62470B	Historic Drg.No.	1 09 101 0675
Date Issued 2/01/2007	Checked By DAVE MARSHALL	Revision	Notes		