


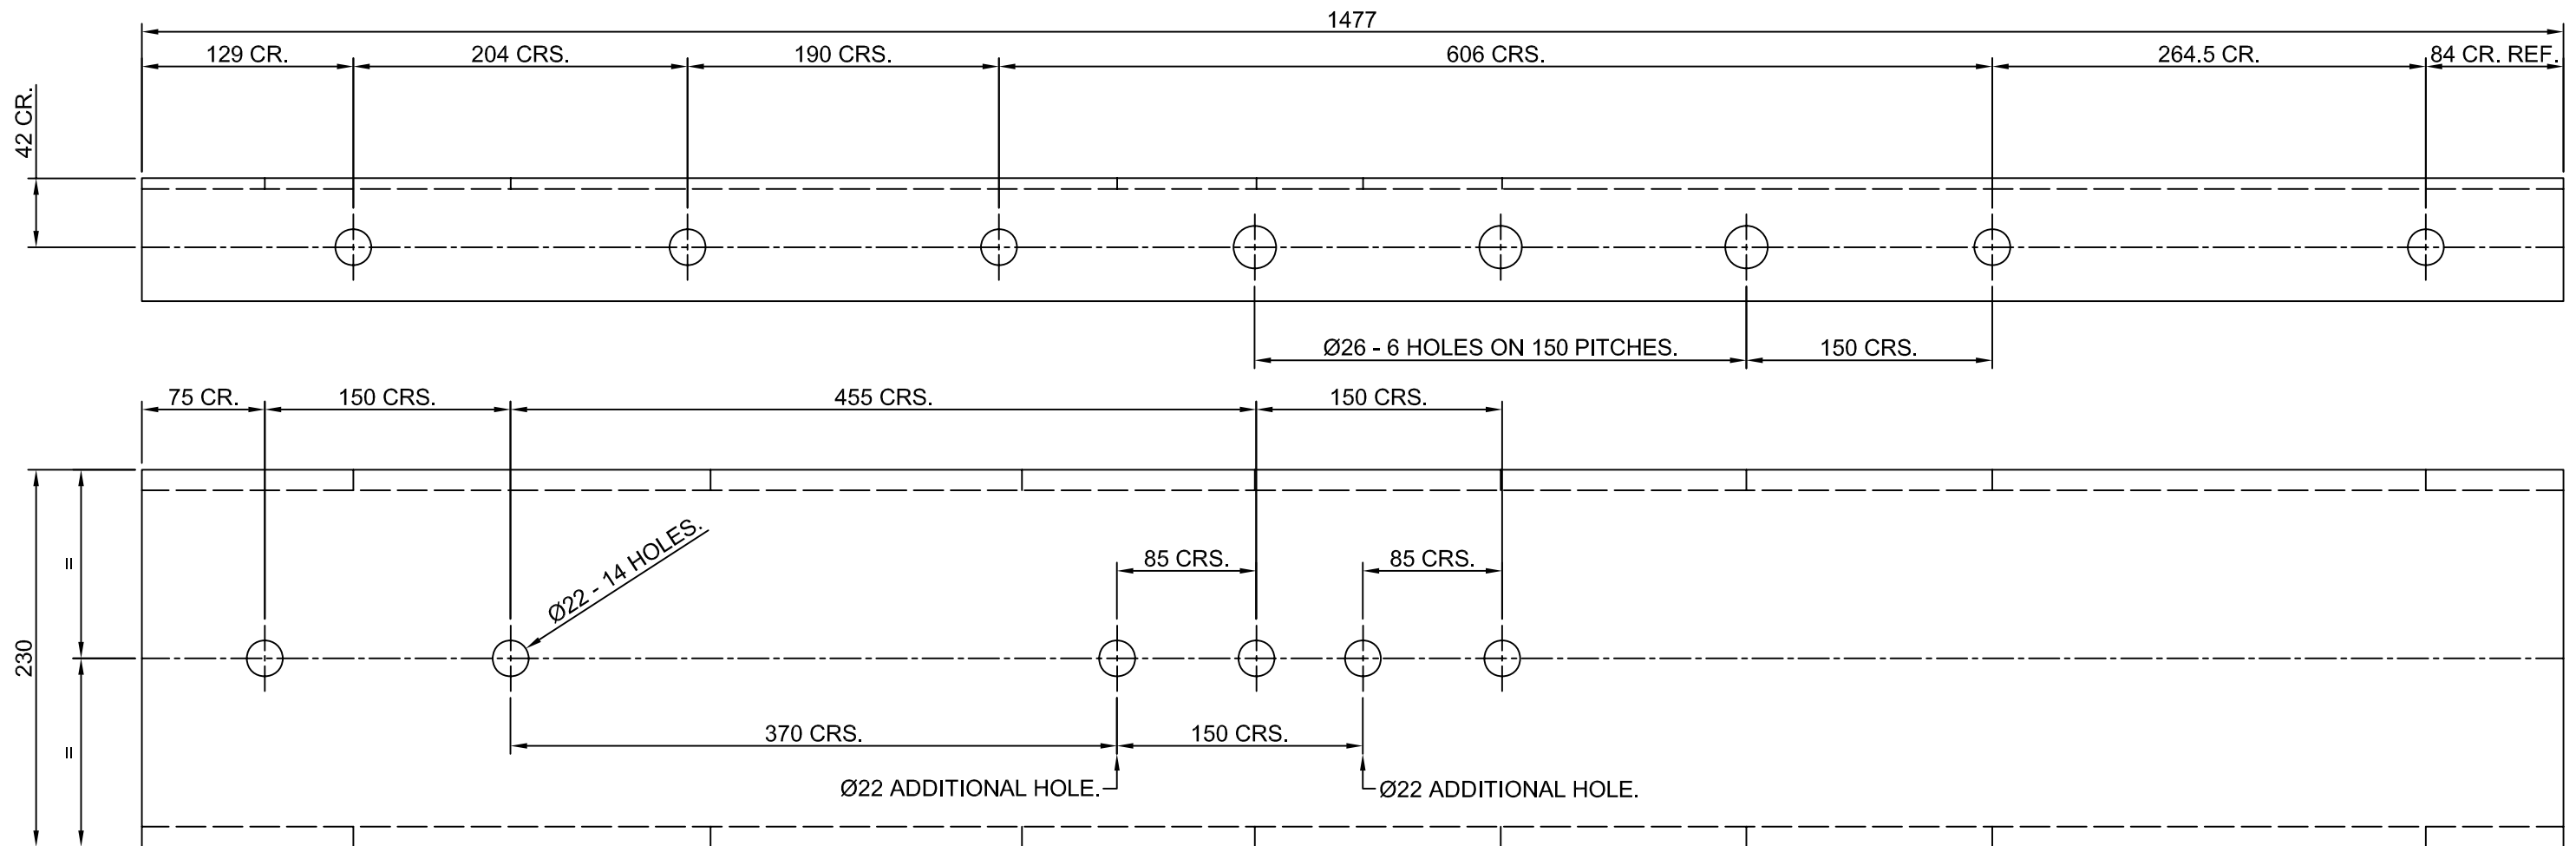

MATERIAL: 1477 LONG x 230 WEB x 75 FLANGE (25.7 kg/m) PARALLEL FLANGE CHANNEL TO B.S. 4 PART 1: 1993.

NOTE:- MADE FROM SKETCH No.31, BUT WITH TWO ADDITIONAL HOLES, WHERE SHOWN.

- NOTES:-
1. STEELWORK TO B.S. 4360, GRADE 43A & B.S. 449
 2. SECTIONS TO B.S. 4, PART 1, FLATS TO B.S. 6722
 3. ALL BURRS TO BE REMOVED.
 4. GALVANIZING TO B.S. 729 AFTER FABRICATION.

		Lloyds Court, 78 Grey Street, Newcastle Upon Tyne, NE1 6AF	
		132kV OVERHEAD LINES 125kN TENSION INSULATOR SET TWO x SHORT CROSSARM SUPPORT CHANNEL FOR FOR STRENGTH TEST RIG	
Manufacturer Details		Type OVERHEAD	
Sheet No. 1	Scale 1:4		
Prepared By TREVOR R. WILKIN		DOCUMENT_SUB_CLASS	
Revised	Grid Reference	Ref No.	62470B
Date Issued 3/01/2007	Checked By	Revision	Notes
		Historic Drg.No.	SKETCH No.31