


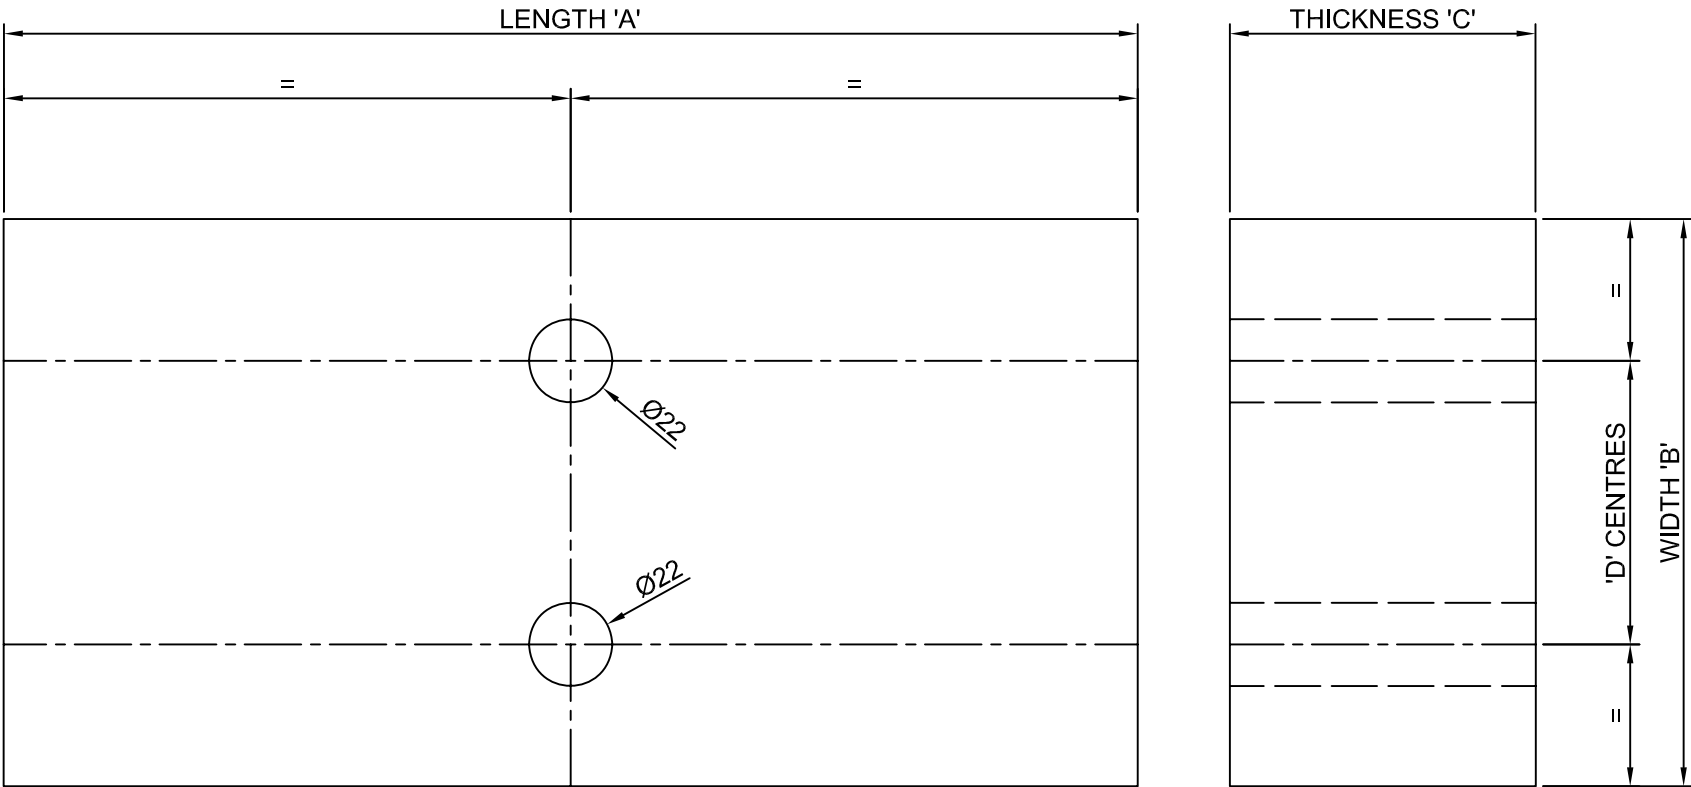

ITEM No.	LENGTH 'A'	WIDTH 'B'	THICKNESS 'C'	'D' CENTRES	MATERIAL
1	270	220	10	150	STEEL
2	270	220	5	150	STEEL
3	270	220	2	150	STEEL
.	.	.	.	.	.
.	.	.	.	.	.
.	.	.	.	.	.
.	.	.	.	.	.
.	.	.	.	.	.
.	.	.	.	.	.

NOTES

- 1. ALL DIMENSIONS ARE IN MILLIMETRES.
- 2. ALL ITEMS SHOULD BE HOT DIP GALVANIZED AFTER DRILLING & DEBURRING.

Manufacturer Details

Sheet No.

Scale
N.T.S.

Prepared By
TREVOR R. WILKIN

Revised

Date Issued
24/01/06

Grid Reference

Checked By
DAVE MARSHALL

Lloyds Court, 78 Grey Street, Newcastle Upon Tyne, NE1 6AF

132kV OVERHEAD LINES

SCHEDULE OF STEEL SHIMS FOR USE
ON RUTTER TYPE POLE WITH UNIVERSAL
BEAM STYLE SHEAR BLOCKS

Type
OVERHEAD

DOCUMENT_SUB_CLASS

Ref No. 62470B

Historic Drg.No.

Revision

Notes

SKETCH No.32