


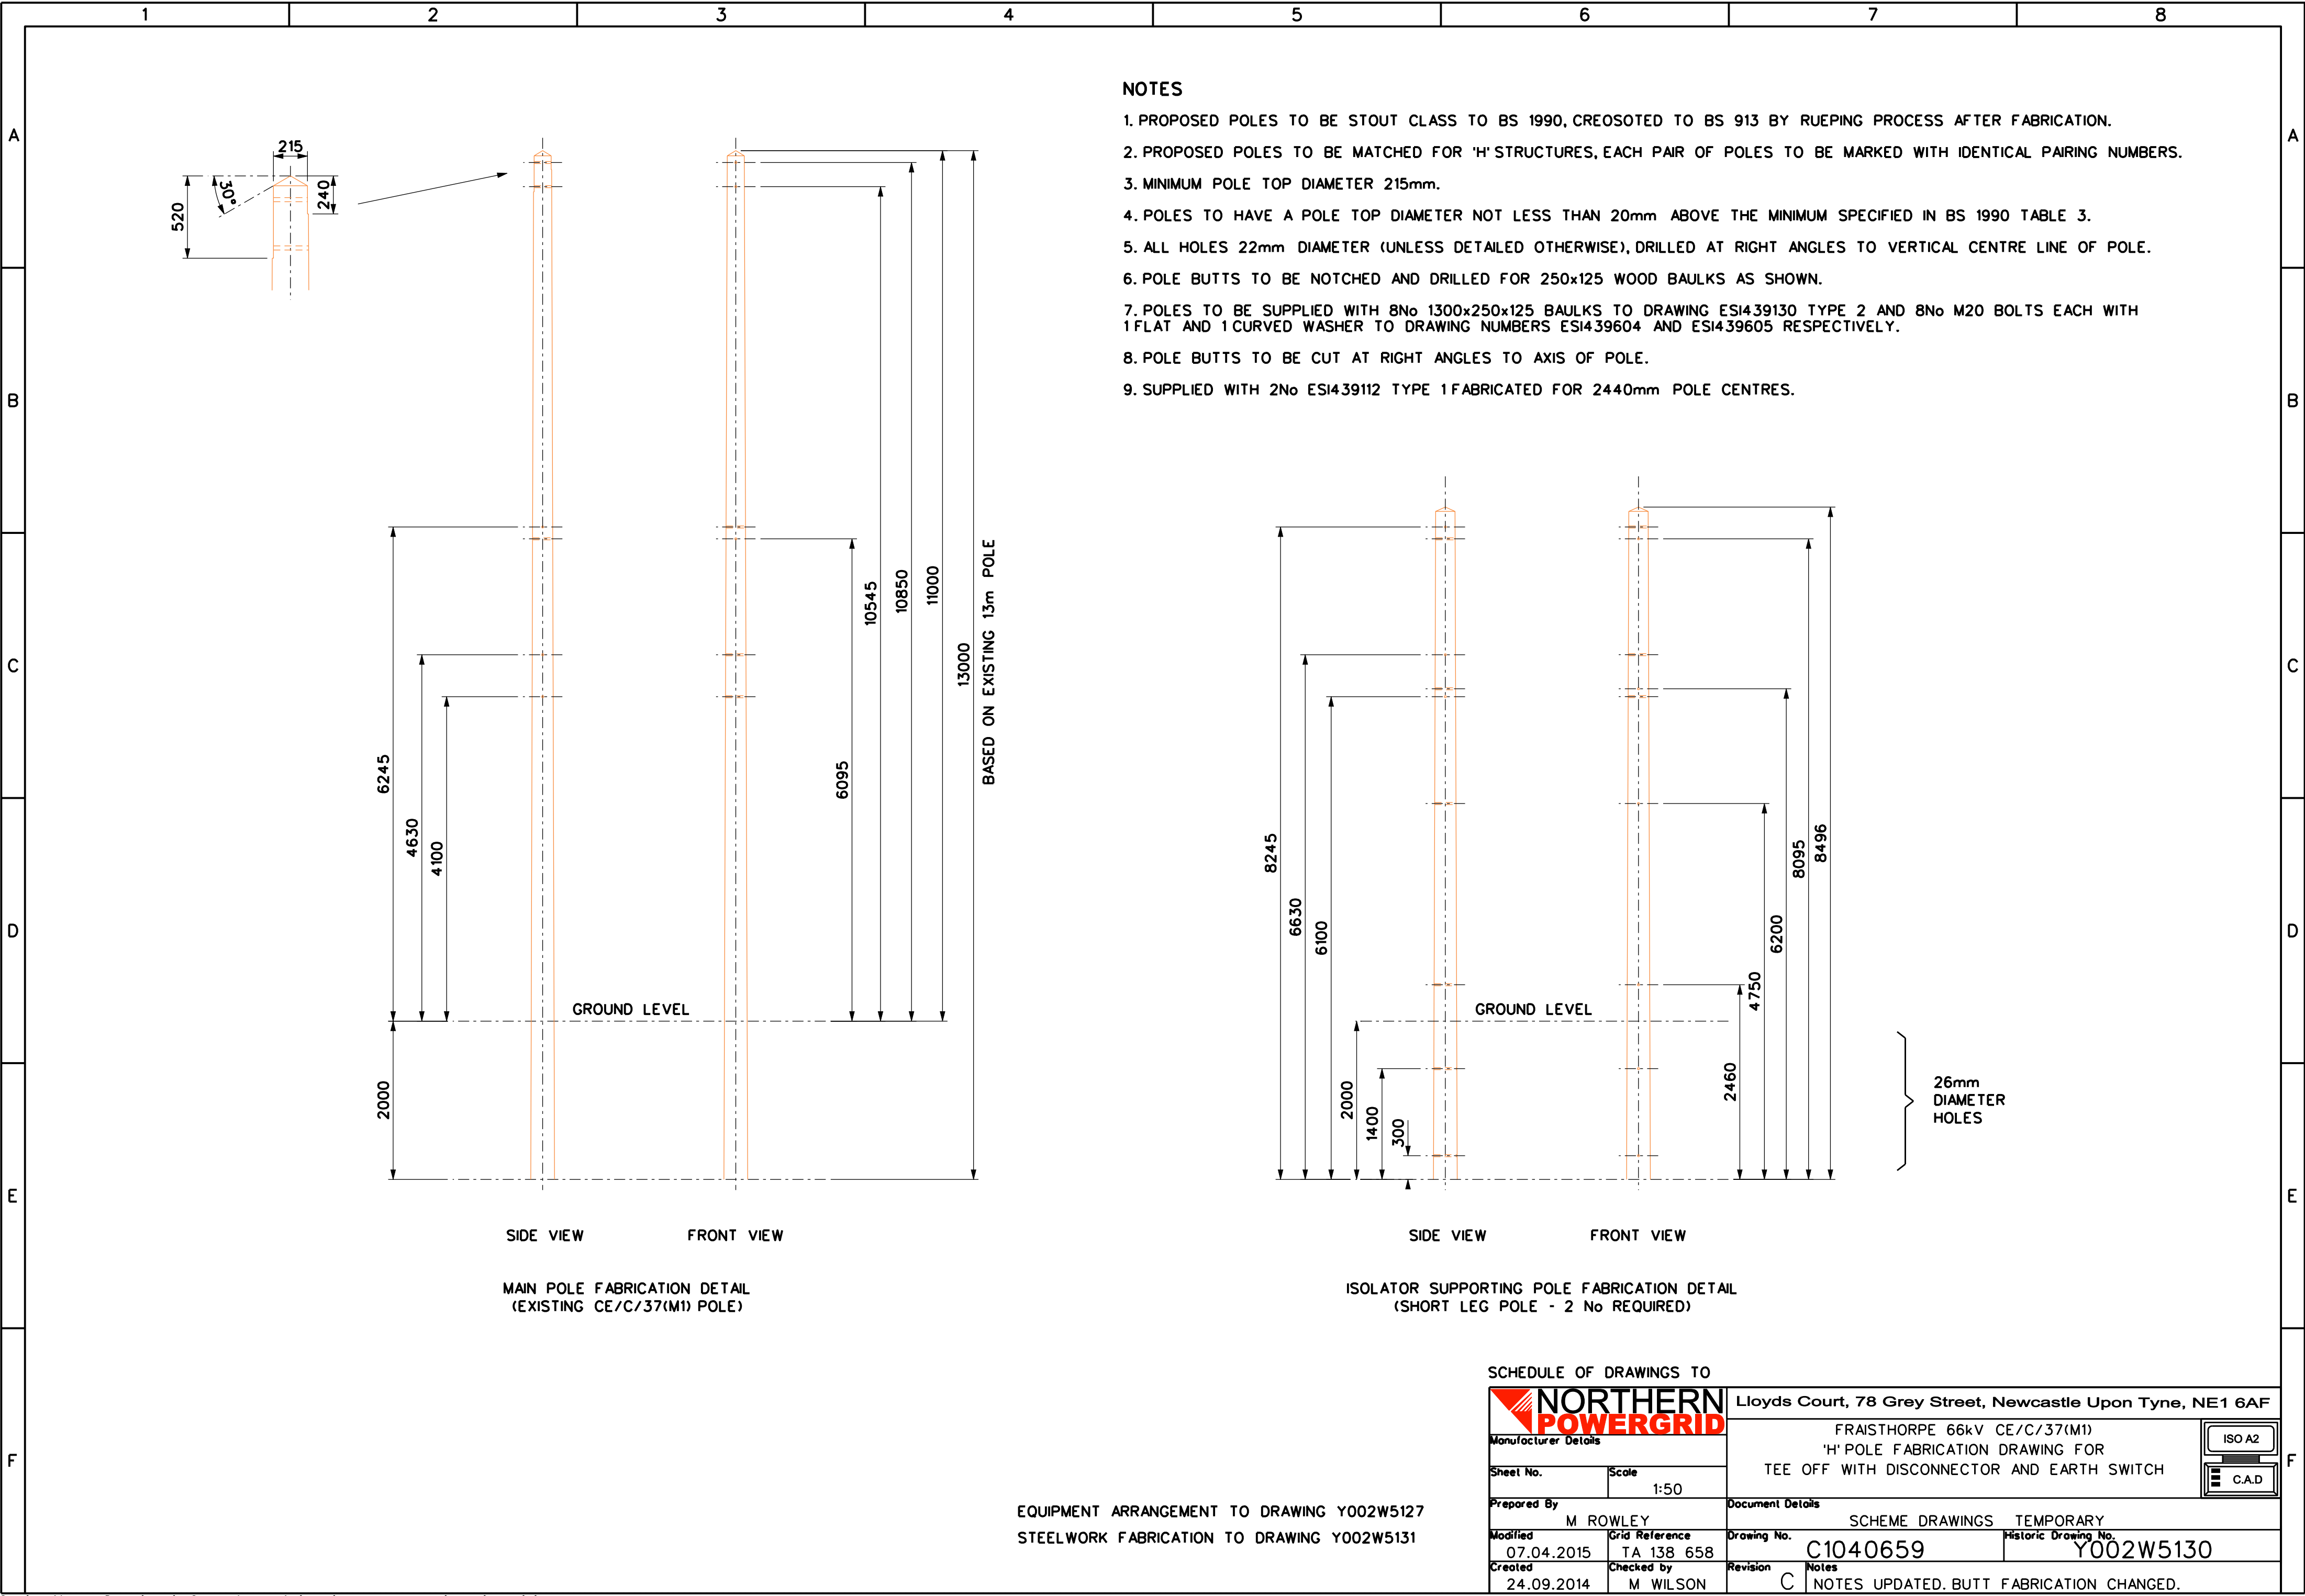

EQUIPMENT ARRANGEMENT TO DRAWING Y002W5127
STEELWORK FABRICATION TO DRAWING Y002W5131

SCHEDULE OF DRAWINGS TO			
NORTHERN POWERGRID		Lloyds Court, 78 Grey Street, Newcastle Upon Tyne, NE1 6AF	
Manufacturer Details		FRAISTHORPE 66kV CE/C/37(M1)	
Sheet No.		Scale	
		1:50	
Prepared By		M ROWLEY	
Modified		Grid Reference	
07.04.2015		TA 138 658	
Created		Checked by	
24.09.2014		M WILSON	
Document Details		SCHEME DRAWINGS TEMPORARY	
Drawing No.		C1040659	
Historic Drawing No.		Y002W5130	
Revision		Notes	
C		NOTES UPDATED. BUTT FABRICATION CHANGED.	