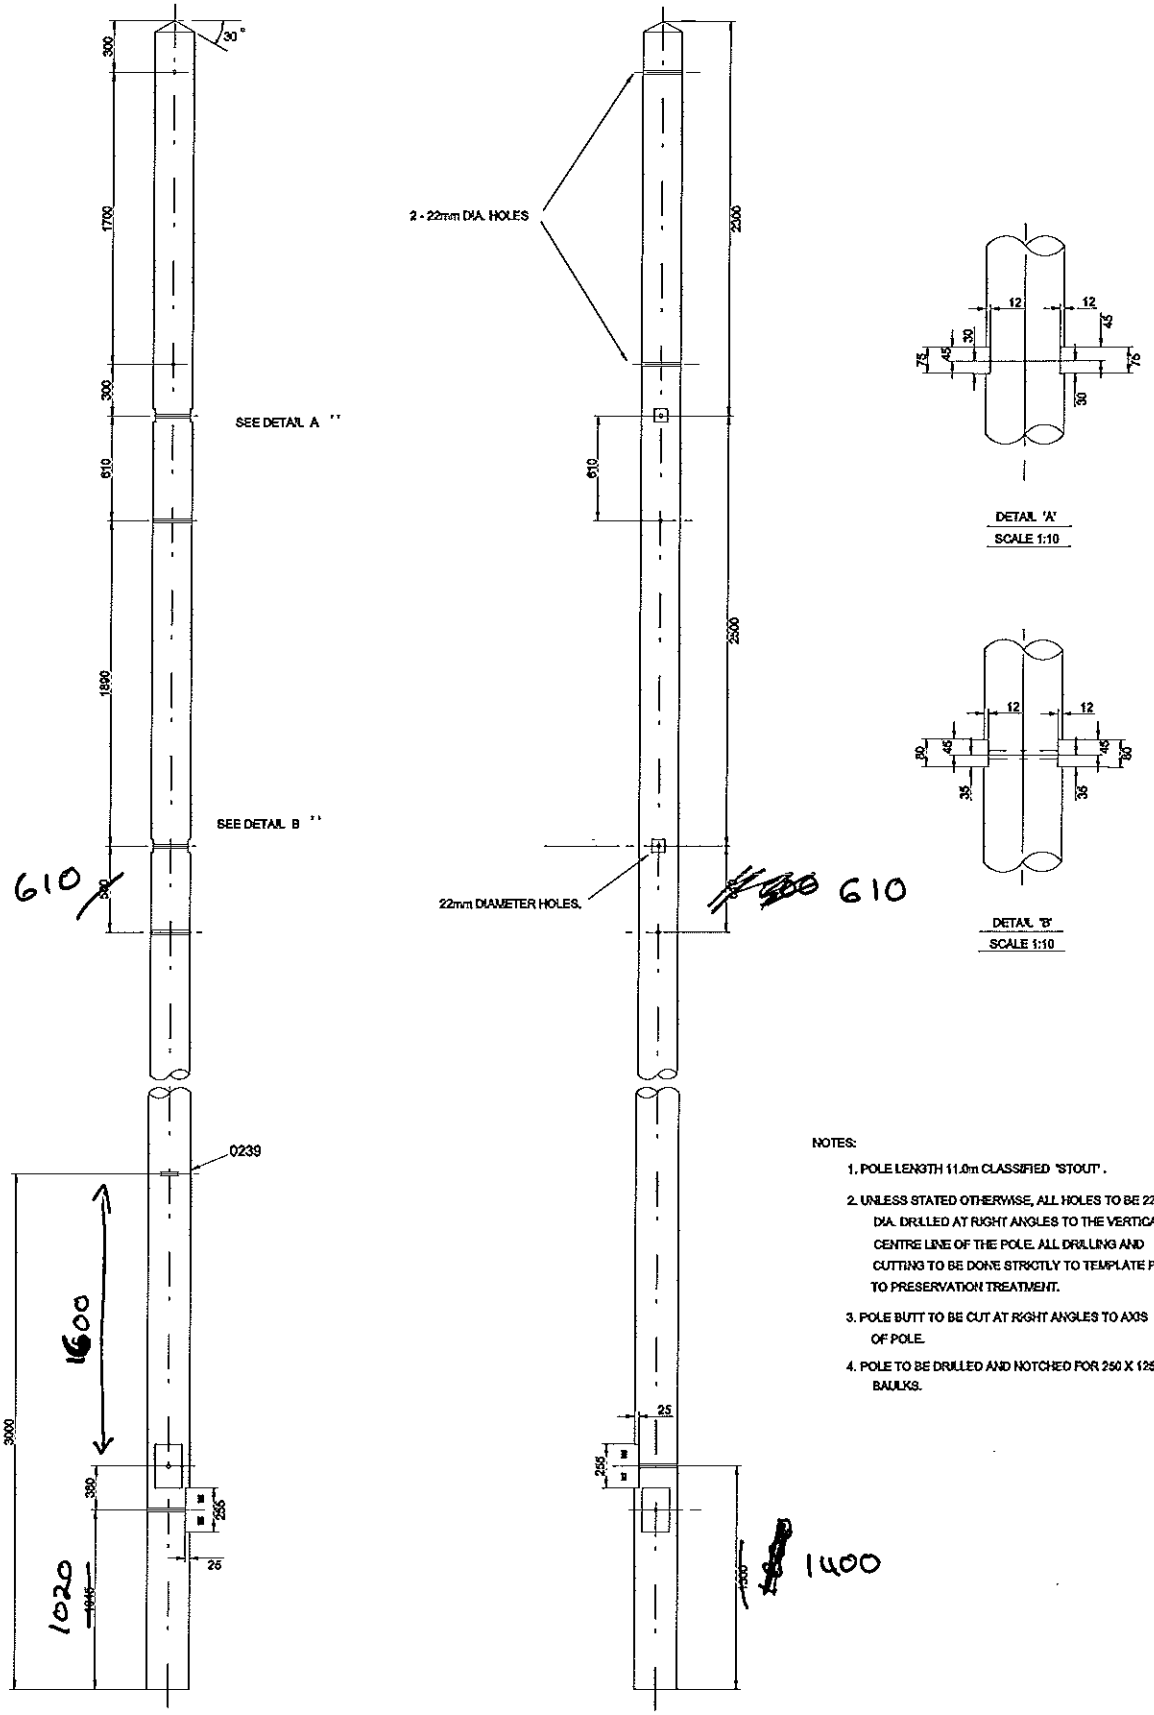


DETAIL 'A'
SCALE 1:10

DETAIL 'B'
SCALE 1:10

NOTES:

1. POLE LENGTH 11.0m CLASSIFIED 'STOUT'.
2. UNLESS STATED OTHERWISE, ALL HOLES TO BE 22mm DIA. DRILLED AT RIGHT ANGLES TO THE VERTICAL CENTRE LINE OF THE POLE. ALL DRILLING AND CUTTING TO BE DONE STRICTLY TO TEMPLATE PRIOR TO PRESERVATION TREATMENT.
3. POLE BUTT TO BE CUT AT RIGHT ANGLES TO AXIS OF POLE.
4. POLE TO BE DRILLED AND NOTCHED FOR 250 X 125 BAULKS.

ALL DIMENSIONS SHOWN ARE IN MILLIMETRES UNLESS OTHERWISE STATED.

NORTHERN POWERGRID Manufacturer Details		Lloyds Court, 78 Grey Street, Newcastle Upon Tyne, NE1 6AF
Sheet No. 2	Scale AS SHOWN	11KV & 20KV OVERHEAD LINES FABRICATION FOR THREE PHASE TOTEM POLE S.S. WITH HV FUSE UNITS & HV SUPPLY OFF U/G CABLE & U/G SUPPLY TO LV NETWORK (1.09.108.0865 SHT1)
Prepared By Joan Oakley		Type OVERHEAD STANDARDS
Revised 13/11/13	Grid Reference	Ref No. 0990260 Historic Drg.No. 1091080865
Date Issued 10/03/11	Checked By S BLAKELD	Revision A Notes