

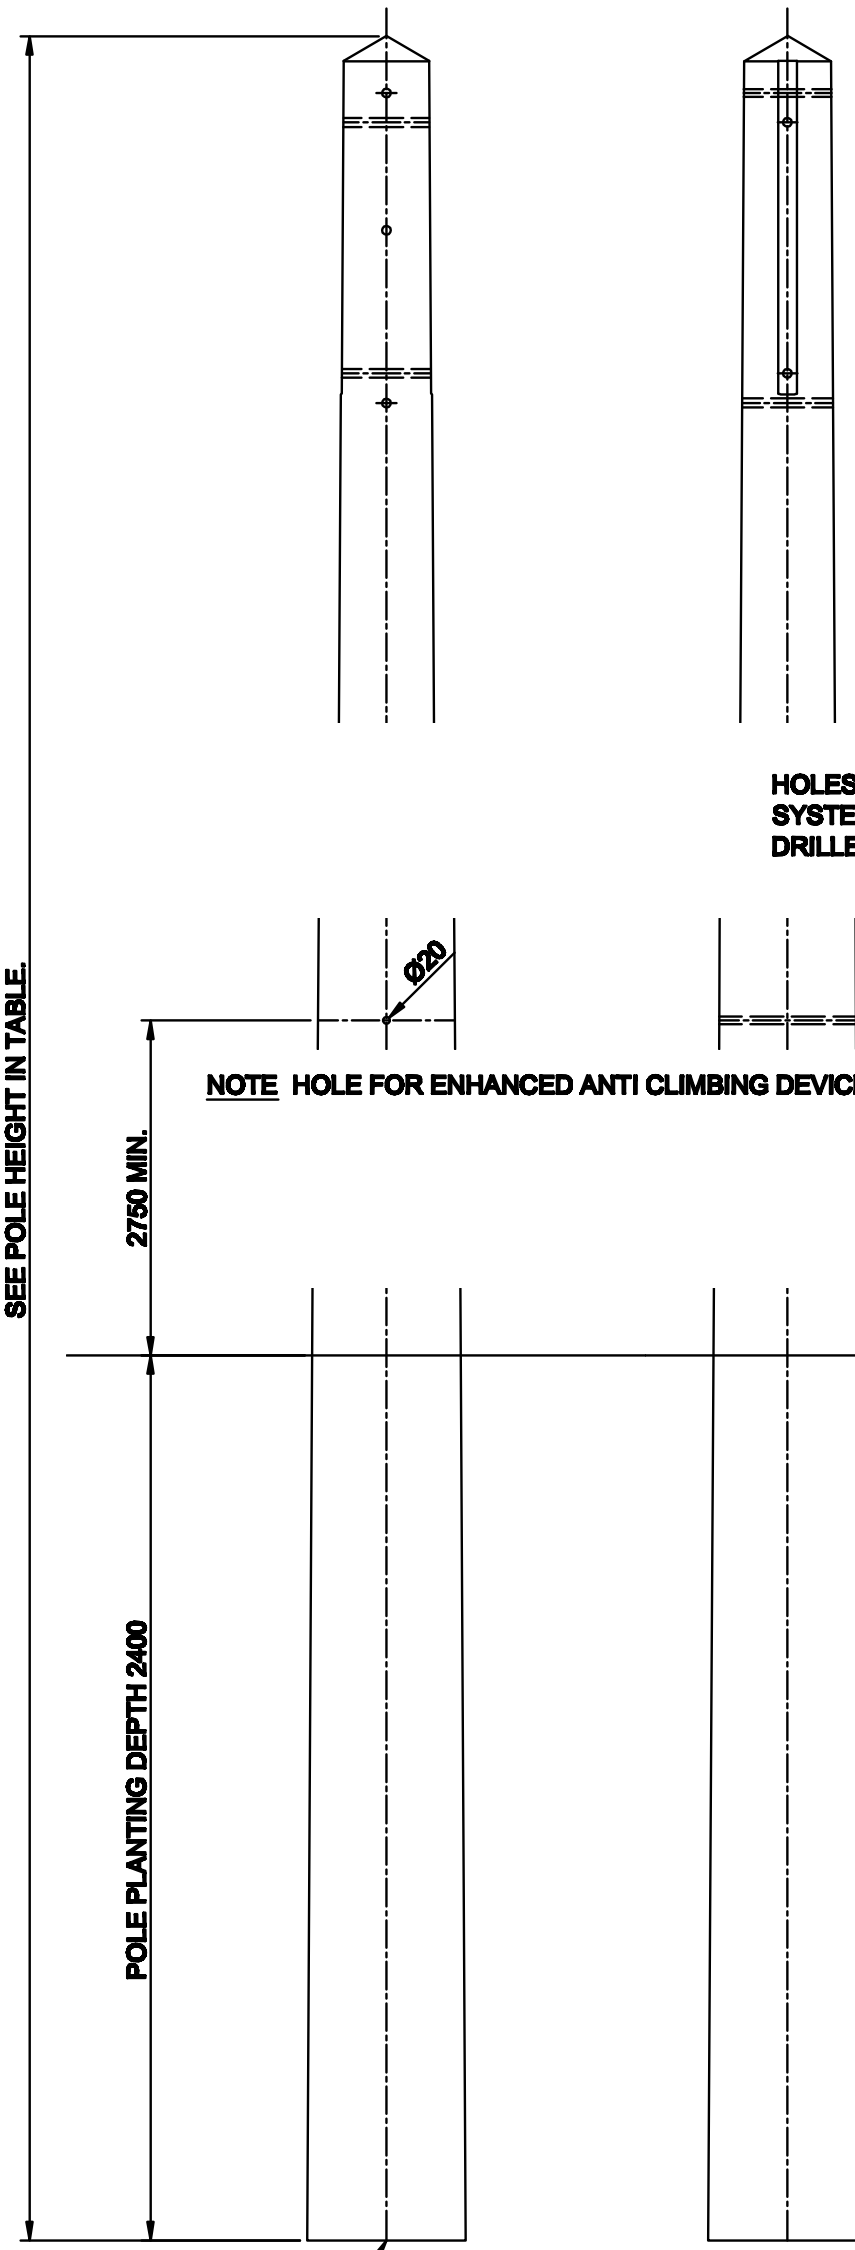


SCALE:- 1:20

POLE LENGTH/ CLASS TO BE IMPRESSED ON POLE BUTT.

THIS VIEW SHOWS THE POLE FACE (NATURAL LIE OF POLE).

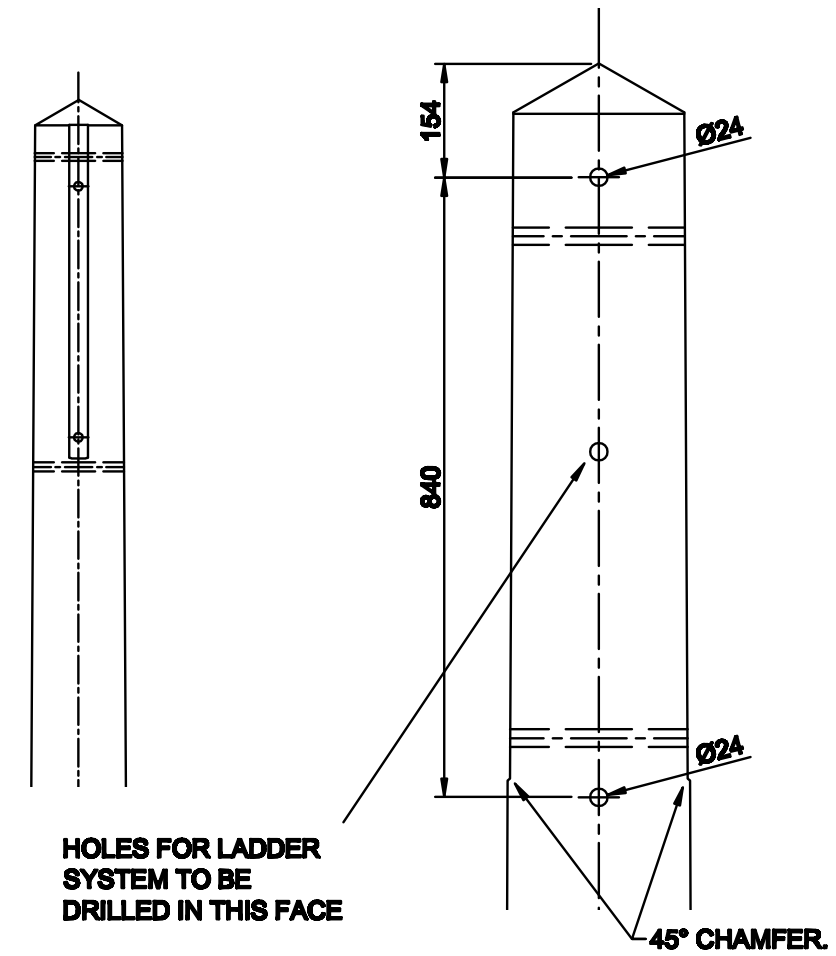

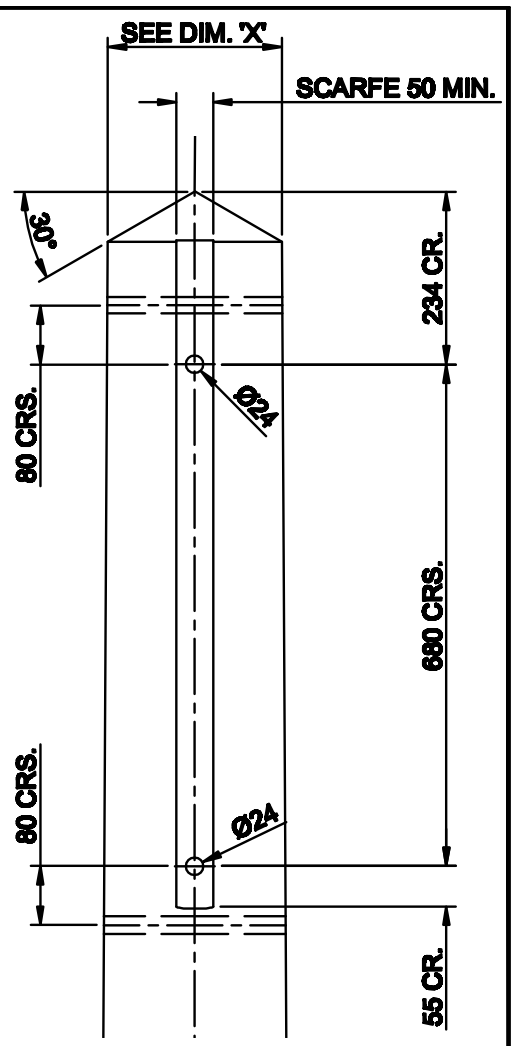

ENLARGED VIEWS OF POLE APEX SCALE 1:10

IMPORTANT NOTE

THE SCARFE IS PARALLEL TO THE POLE EDGE & NOT THE POLE CENTRELINE.

SCARFING TO BE CUT TO GIVE A 50mm WIDE FLAT ON TWO DIAMETRICALLY OPPOSITE FACES WITH ENDS CHAMFERED AS SHOWN.

NOTES
1. CLASS OF POLE TO BE EXTRA STOUT IN ACCORDANCE WITH 1.09.101.0238
2. POLE BUTT TO BE CUT AT RIGHT ANGLES TO AXIS OF POLE.
3. ALL HOLES EXCEPT WHERE STATED OTHERWISE TO BE 24mm DIA. DRILLED AT RIGHT ANGLES TO VERTICAL CENTRELINE OF POLE. ALL DRILLING & CUTTING TO BE DONE STRICTLY TO TEMPLATE PRIOR TO CREOSOTING.
4. BS 1990 TABULATED MIN VALUES HAVE BEEN AMENDED TO REFLECT CALCULATED MEAN VALUES

ITEM	POLE HEIGHT	DIMENSION 'X' (MIN/MAX)	DIMENSION 'Y' (MIN/MAX)
A	12000mm	245	335
B	13000mm	245	350
C	14000mm	245	365
D	15000mm	245	375
E	16000mm	250	390
F	17000mm	250	415

NORTHERN POWERGRID

Lloyds Court, 78 Grey Street, Newcastle Upon Tyne, NE1 6AF

Manufacturer Details

Sheet No. 2 | Scale AS SHOWN

Prepared By Joan.Oakley

Revised 19/11/13 | Grid Reference

Date Issued 02/07/07 | Checked By G HAMMEL

132KV OVERHEAD LINES DRILLING, SCARFING AND MARKINGS FOR SINGLE ANGLE POLE ARRANGEMENT

Type OVERHEAD | DOCUMENT_SUB_CLASS

Ref No. C949737 | Historic Drg.No. 1091390003

Revision F | Notes