


ITEM	CATALOGUE No
1	252651
2	252666
3	258709
4	252670
5	240739
6	246538

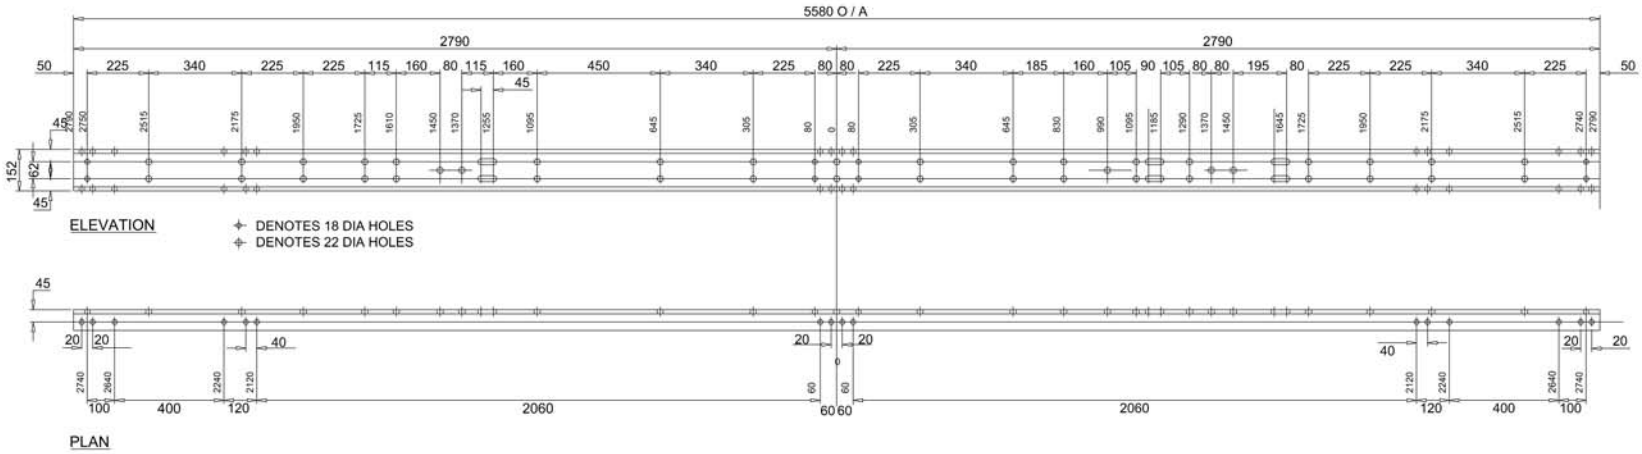


ITEM 1 152 x 76 x 5580 LONG CHANNEL

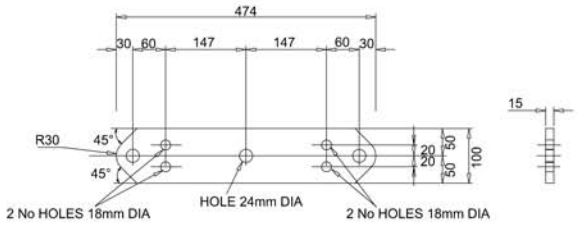


ITEM 2 100 x 15 x 474 LONG FLAT BAR

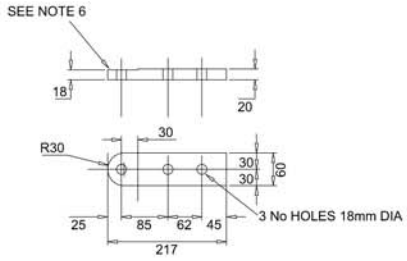


ITEM 3 60 x 20 FLAT BAR 217 LONG

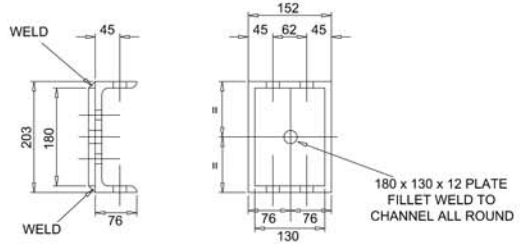

ITEM 4 203 x 76 CHANNEL 152 LONG

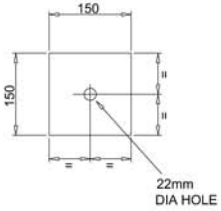

ITEM 5 150 x 150 x 15 THICK PLATE

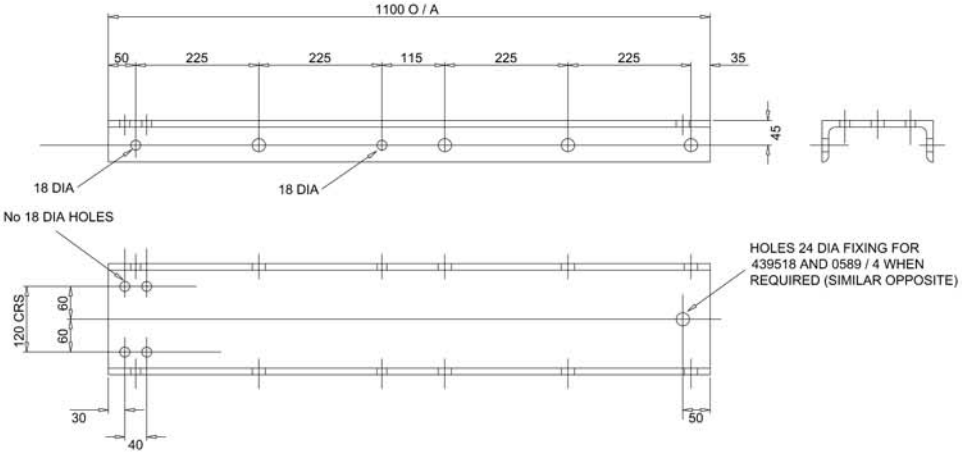

ITEM 6 203 x 76 x 23.82 kg / METRE CHANNEL

NOTES:-

1. STEELWORK TO BS EN 10025 GRADE Fe 430B
2. SECTIONS TO BS 4848 PART 3 FLATS TO BS 6727
3. GALVANISING TO BS 729 AFTER FABRICATION
4. HOLES ARE 22mm DIA EXCEPT HOLES MARKED OTHERWISE
5. 22mm DIA SLOTS TO HAVE STRAIGHT PARALLEL SIDES
6. ITEM 3 20mm THICK FLAT AT ROUNDED END OF BAR TO BE MACHINED ON ONE FACE TO 18mm THICK FOR A DISTANCE OF 55mm
7. COMPONENTS TO BE MARKED WITH COMPANY STACK CATALOGUE NUMBER

ALL DIMENSIONS SHOWN ARE IN MILLIMETRES UNLESS OTHERWISE STATED

CE Electric UK
Manufacturer Details

Lloyds Court, 78 Grey Street, Newcastle Upon Tyne, NE1 6AF

66KV OVERHEAD LINES - PORTAL TYPE
CROSSARM COMPONENTS

Sheet No. 1	Scale 1:10
Prepared By Janis.Webb	Type OVERHEAD LINES
Revised 08/08/06	Grid Reference
Date Issued 06/12/04	Checked By G HAMMEL
Ref No. C318503	Historic Drg.No. 1091010650
Revision R	Notes