


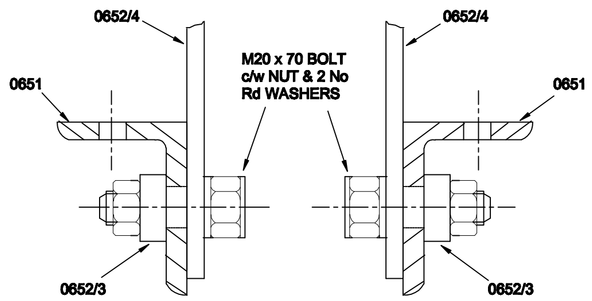


ENLARGED DETAIL 'A'
STOUT POLE SCALE 1:2

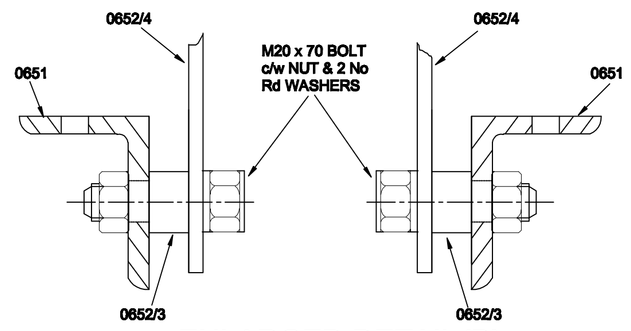


ENLARGED DETAIL 'B'
EXTRA STOUT POLE SCALE 1:2

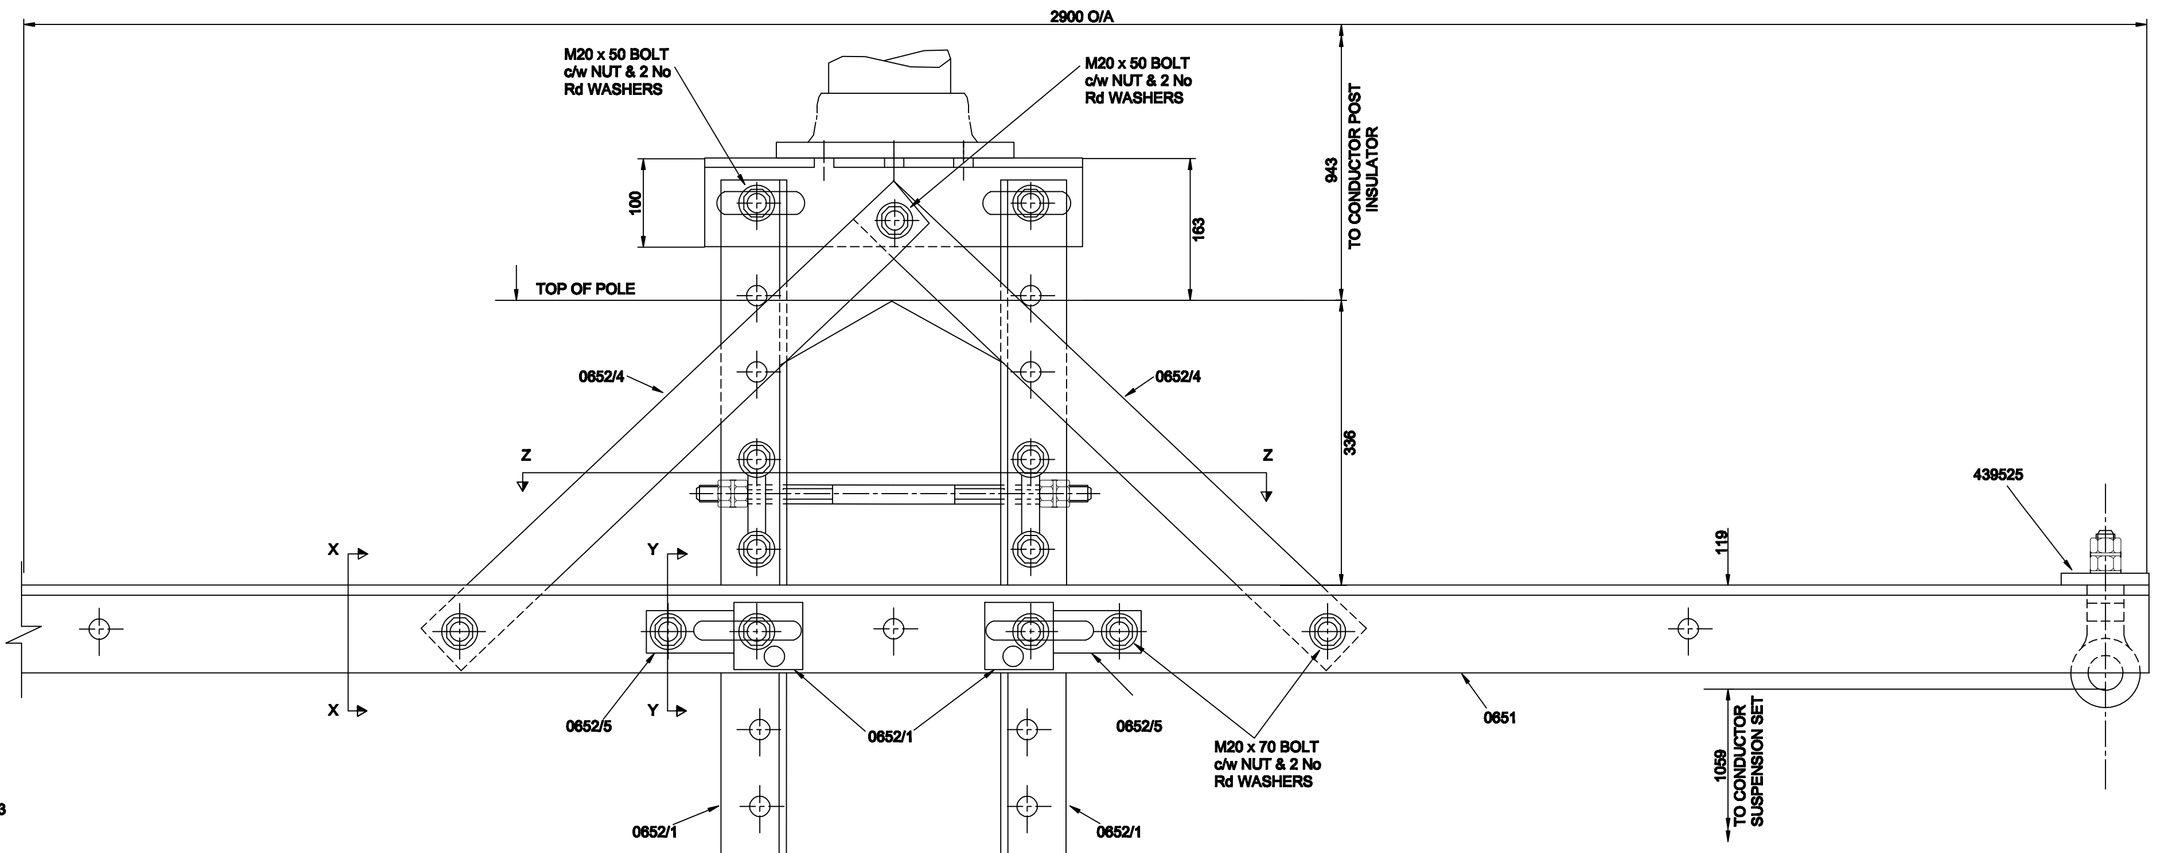

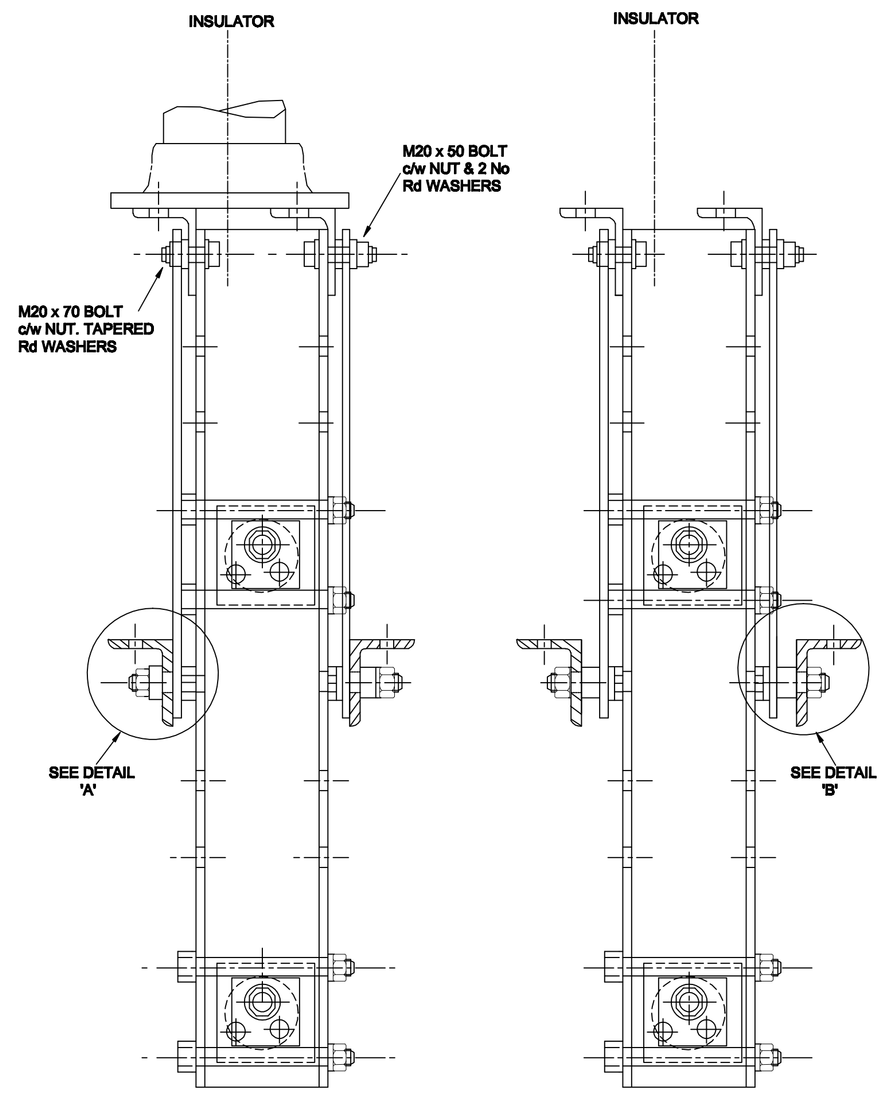


STOUT POLE EXTRA STOUT POLE


SECTION X - X

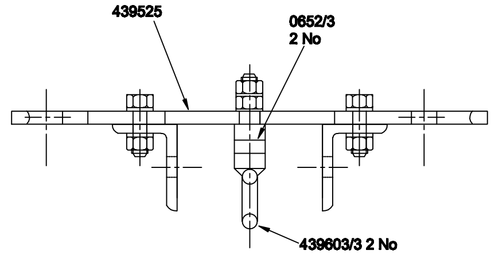

CROSSARM ARRANGEMENT

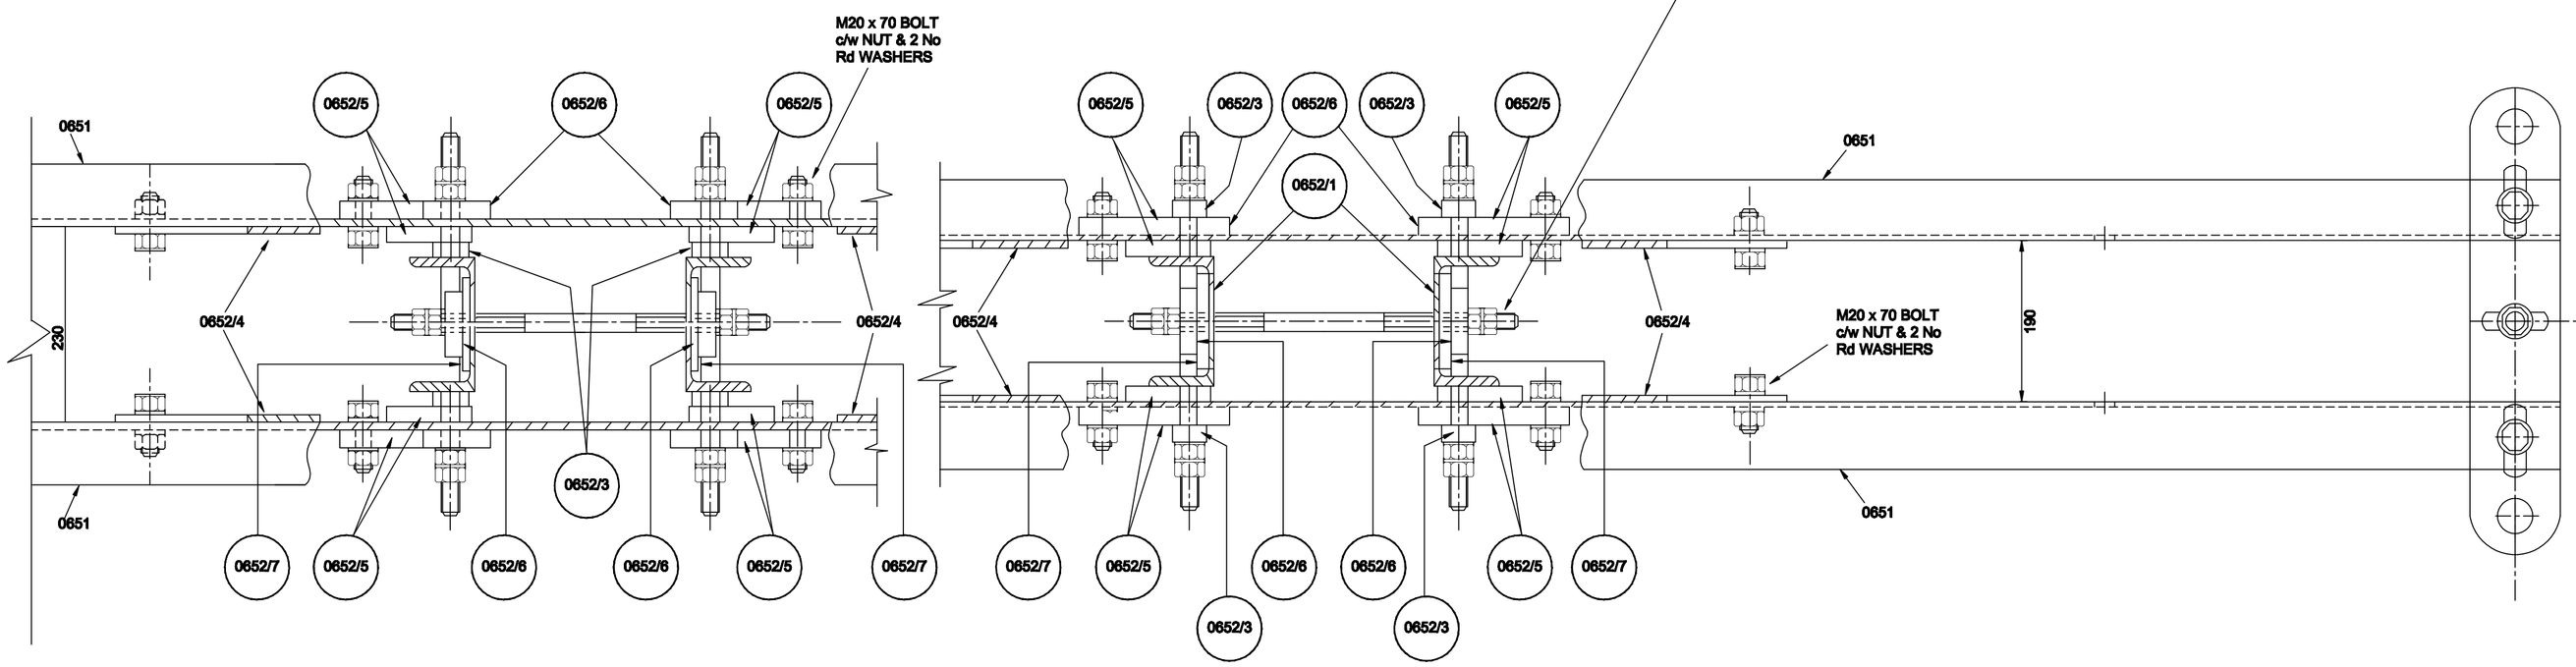

SECTIONAL PLAN ON Z - Z
STOUT POLE

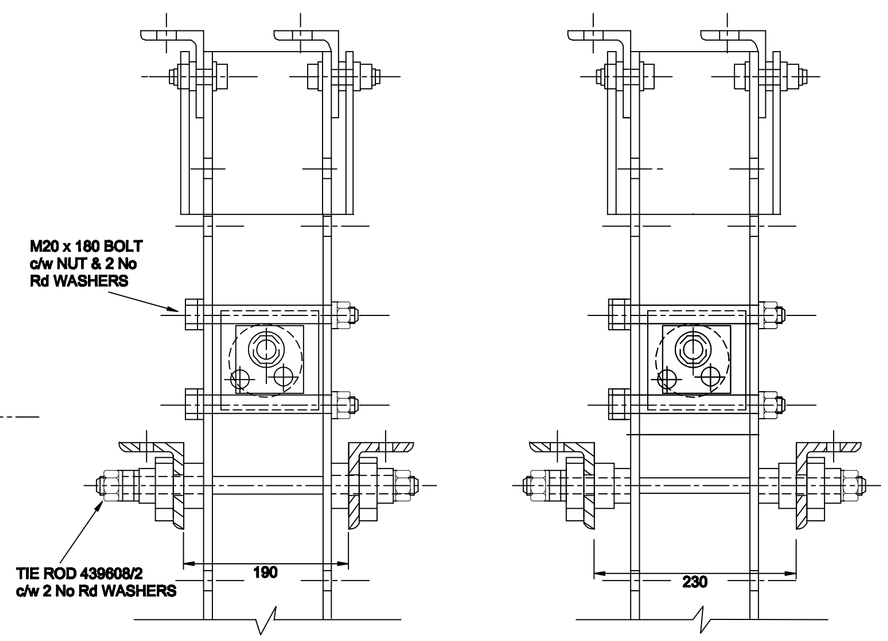

STOUT POLE EXTRA STOUT POLE

SECTION Y - Y

NOTES

1) COMPONENTS WHICH MUST BE LOCATED PRECISELY TO CATER FOR VARIATION IN POLE SIZE SHOWN

2) DETAIL DRAWINGS PREFIXED 43 REFER TO ENA TS DRAWINGS
OTHER DETAIL DRAWINGS REFER TO 1.09.101 SERIES

3) ALL STEELWORK FIXING BOLTS TO BE COMPLETE WITH 1 ROUND WASHER UNDER NUT
1 ROUND WASHER UNDER BOLT HEADS EXCEPT WHERE SPECIFIED OTHERWISE

TO BE READ IN CONJUNCTION WITH DRG No. 1 09 123 1190 SHEET 3
ALL DIMENSIONS SHOWN ARE IN MILLIMETRES UNLESS OTHERWISE STATED

CE Electric UK		Lloyds Court, 78 Grey Street, Newcastle Upon Tyne, NE1 6AF
Manufacturer Details		66KV SINGLE CIRCUIT LINES ASSEMBLY OF COMPONENTS FOR SINGLE POLE HEAVY DUTY STRAIGHT LINE APPLICATION
Sheet No. 3	Scale 1:5	
Prepared By Joan.Oakley		Type OVERHEAD STANDARDS
Revised 16/08/10	Grid Reference	Ref No. C989763 Historic Drg.No. 1091010652
Date Issued 02/08/10	Checked By G HAMMEL	Revision A Notes