
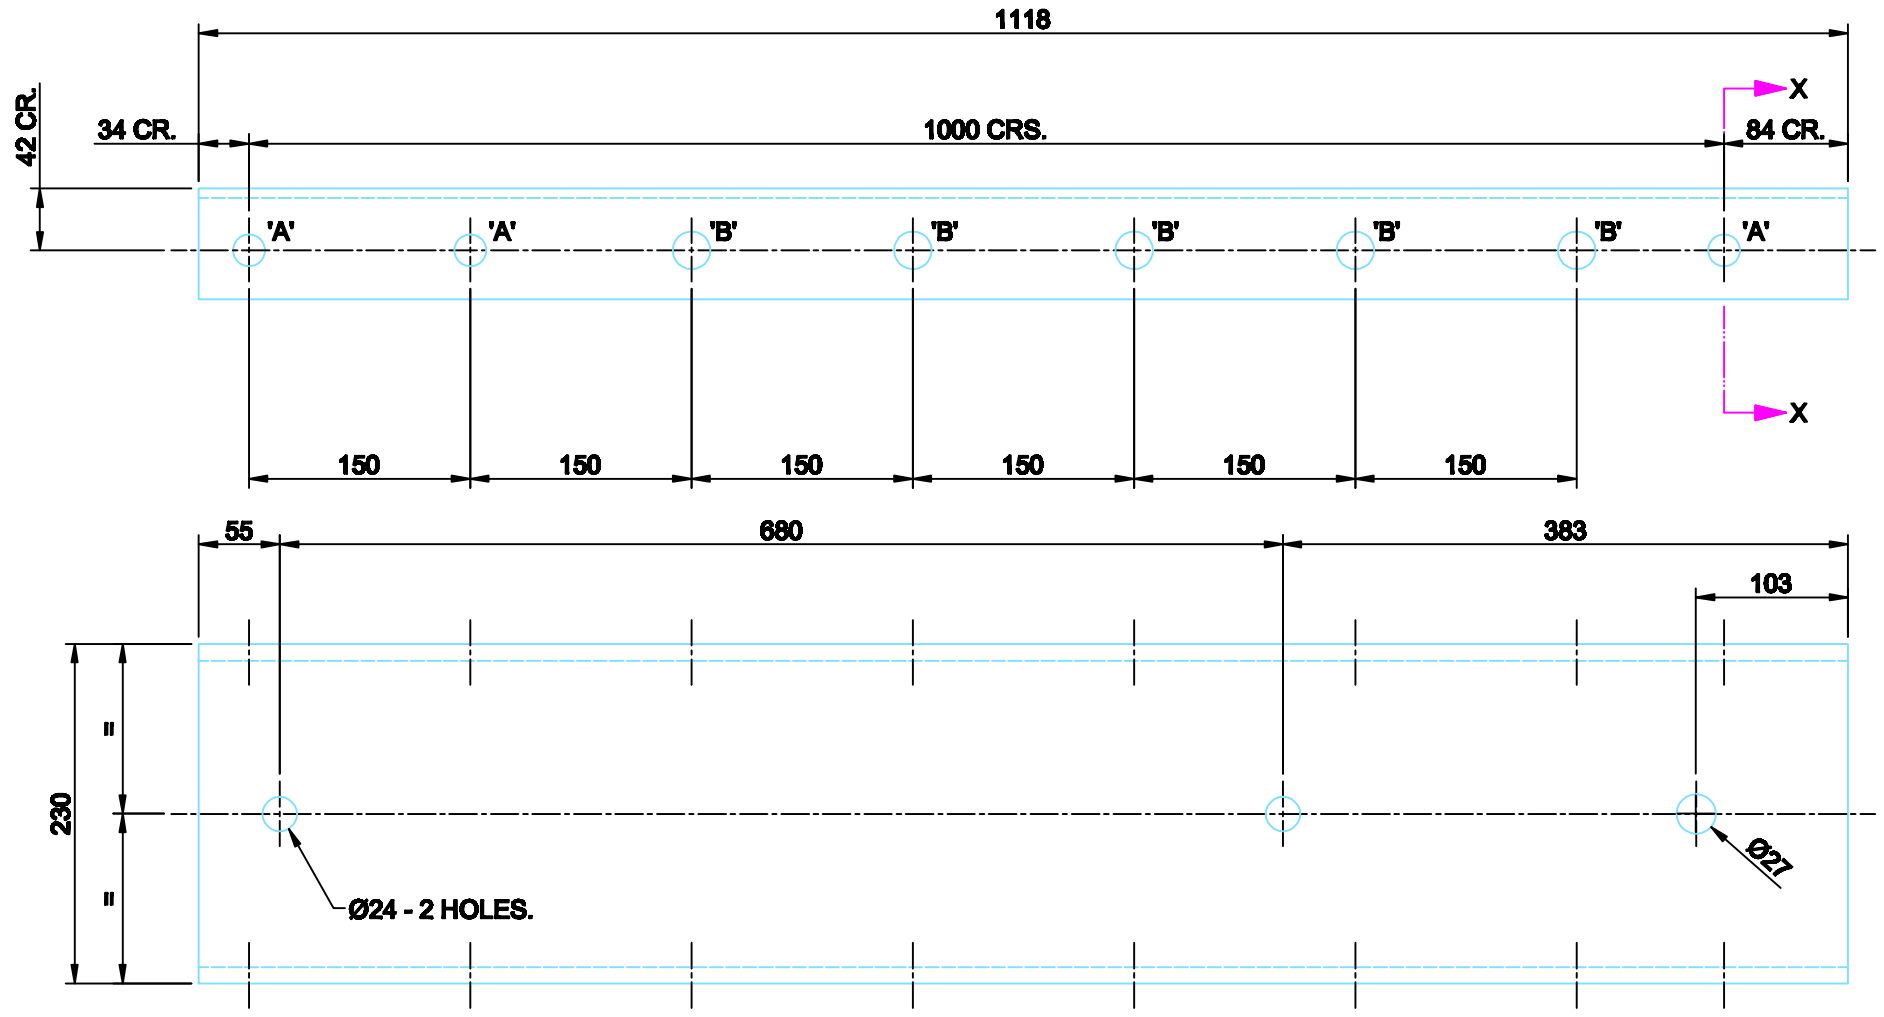


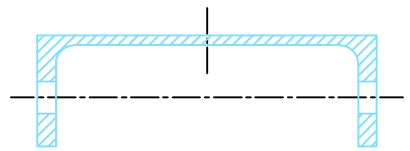

SECTION ON X-X

ITEM 5. 1118 x 230 x 75 (25.7 kg/m) PARALLEL FLANGE CHANNEL TO B.S. 4 PART 1: 1993.

HOLES MARKED 'A' ARE Ø22 DRILLED THROUGH BOTH FLANGES.
HOLES MARKED 'B' ARE Ø26 DRILLED THROUGH BOTH FLANGES.

NOTES:-
1. STEELWORK TO B.S. 4360, GRADE 43A & B.S. 449
2. SECTIONS TO B.S. 4, PART 1, FLATS TO B.S. 6722
3. ALL BURRS TO BE REMOVED.
4. GALVANIZING TO ISO 1461 AFTER FABRICATION.

CE Electric UK		Lloyds Court, 78 Grey Street, Newcastle Upon Tyne, NE1 6AF
Manufacturer Details		132KV OVERHEAD LINES CROSSARM SUPPORT CHANNEL ITEM NO. 5
Sheet No. 5	Scale 1:5	
Prepared By Barbara.Simpson		Type OVERHEAD — DOCUMENT_SUB_CLASS
Revised 03/07/07	Grid Reference	Ref No. C949704 — Historic Drg.No. 1091010675
Date Issued 02/07/07	Checked By G HAMMEL	Revision A — Notes