

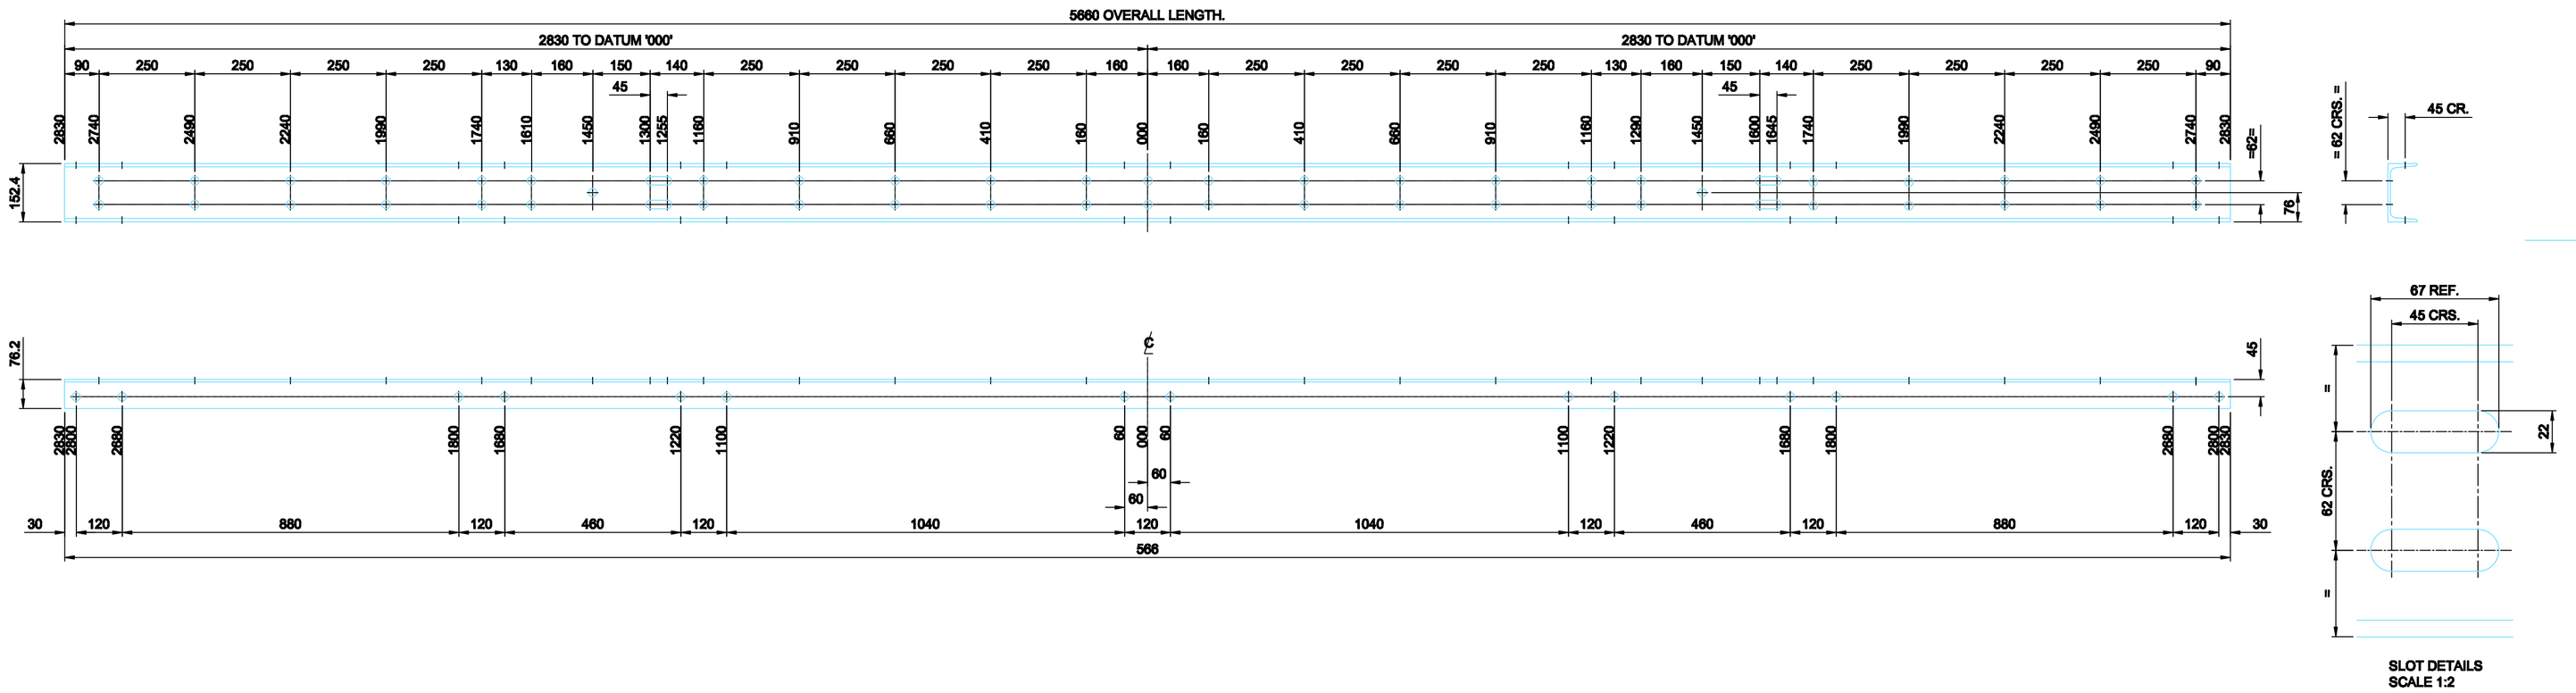



ITEM No.	CATALOGUE No.
1	346507
2	346508
3	258709
4	252670
5	240739
6	346510
7	NOT USED

ITEM 1 152 x 76 x 17.88kg/m CHANNEL
SCALE:- 1:10
QUANTITY:- 2 PER 'H' POLE

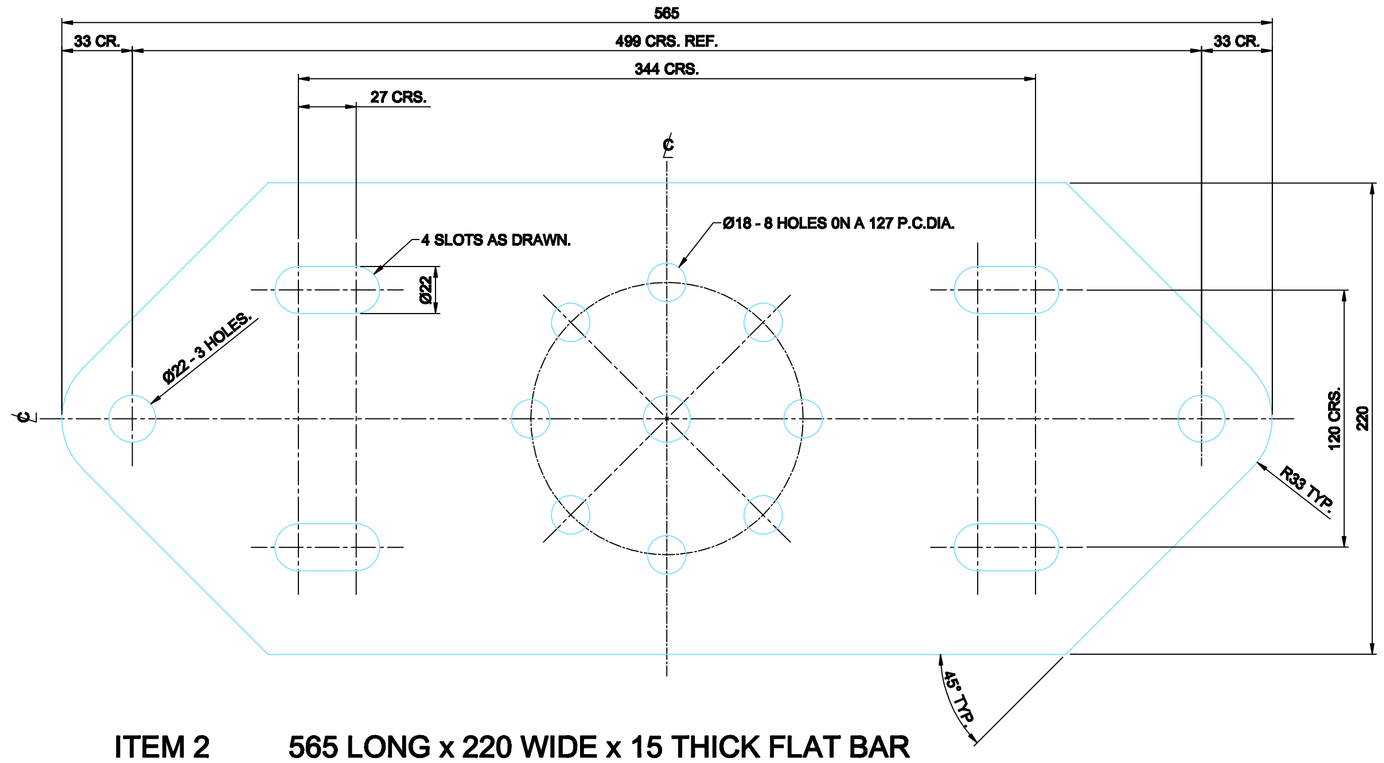


ITEM 2 565 LONG x 220 WIDE x 15 THICK FLAT BAR
SCALE:- 1:2
QUANTITY:- 3 PER 'H' POLE

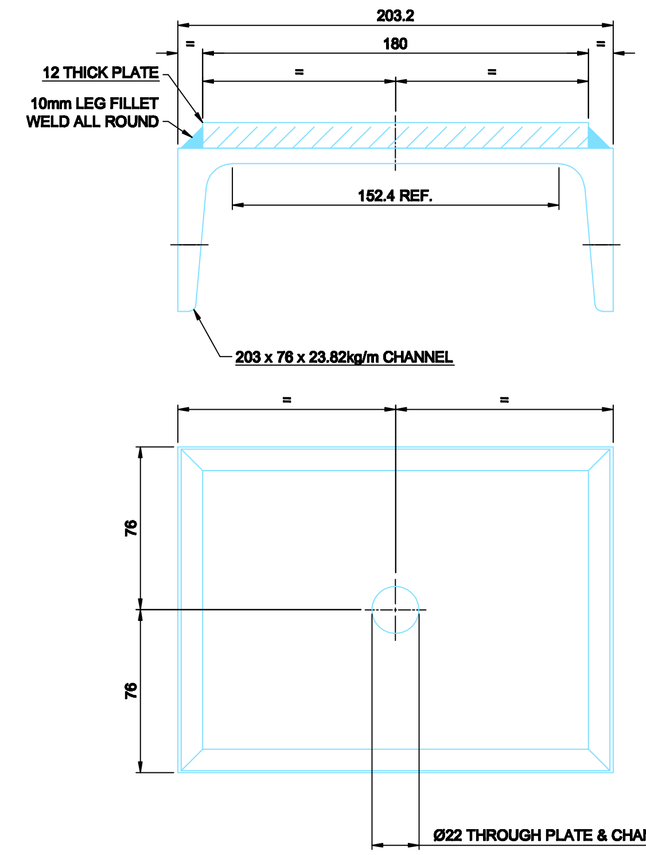


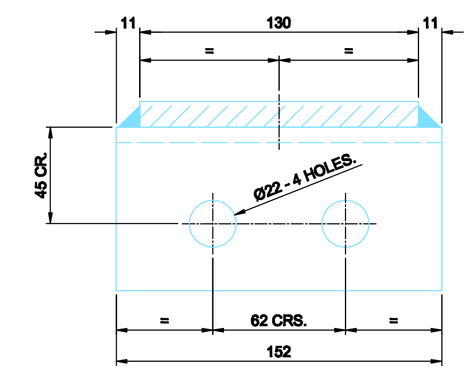

ITEM 4 SEE ABOVE
SCALE:- 1:2
QUANTITY:- 4 PER 'H' POLE

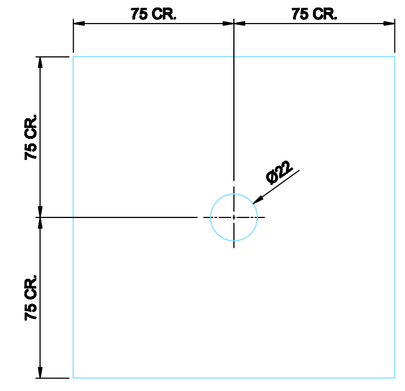


ITEM 5 150 x 150 x 15 THICK PLATE
SCALE:- 1:2
QUANTITY:- 4 PER 'H' POLE

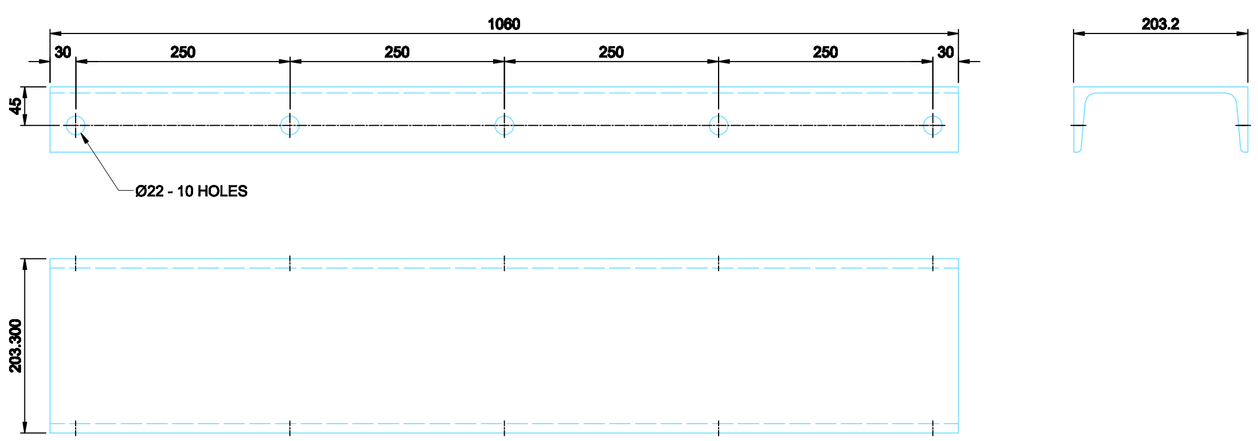

ITEM 6 203 x 76 x 23.82kg/m CHANNEL
SCALE:- 1:5
QUANTITY:- 4 PER 'H' POLE

SEE NOTE 6

SCALE 1:5

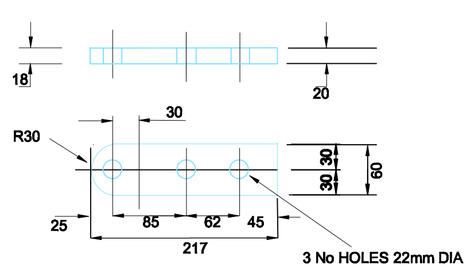

ITEM 3 60 x 20 FLAT BAR 217 LONG

NOTES:-

1. STEELWORK TO BS EN 10025 GRADE Fe 430B.
2. SECTIONS TO BS 4848 PART 3. FLATS TO BS 6727
3. GALVANIZING TO BS 729 AFTER FABRICATION.
4. 22 WIDE SLOTS TO HAVE STRAIGHT PARALLEL SIDES.
5. ALL HOLES ARE 22mm EXCEPT HOLES MARKED OTHERWISE.
6. ITEM 3 20mm THICK FLAT AT ROUNDED END OF BAR TO BE MACHINED ON ONE FACE TO 18mm THICK FOR A DISTANCE OF 55mm.
7. COMPONENTS TO BE MARKED WITH COMPANY STOCK CAT NO.

CE Electric UK
Manufacturer Details

Lloyds Court, 78 Grey Street, Newcastle Upon Tyne, NE1 6AF

132KV OVERHEAD LINES
PORTAL TYPE CROSSARM COMPONENTS

Sheet No. 50	Scale AS SHOWN		
Prepared By Pauline.Moore		Type OVERHEAD	DOCUMENT_SUB_CLASS
Revised 08/05/10	Grid Reference	Ref No. C949730	Historic Drg.No. 1091010675
Date Issued 02/07/07	Checked By G HAMMEL	Revision A Notes	