



THE ASSEMBLED PLAN

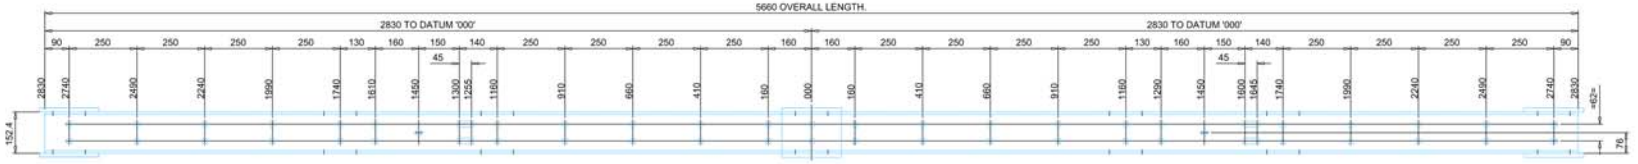

ELEVATION VIEW

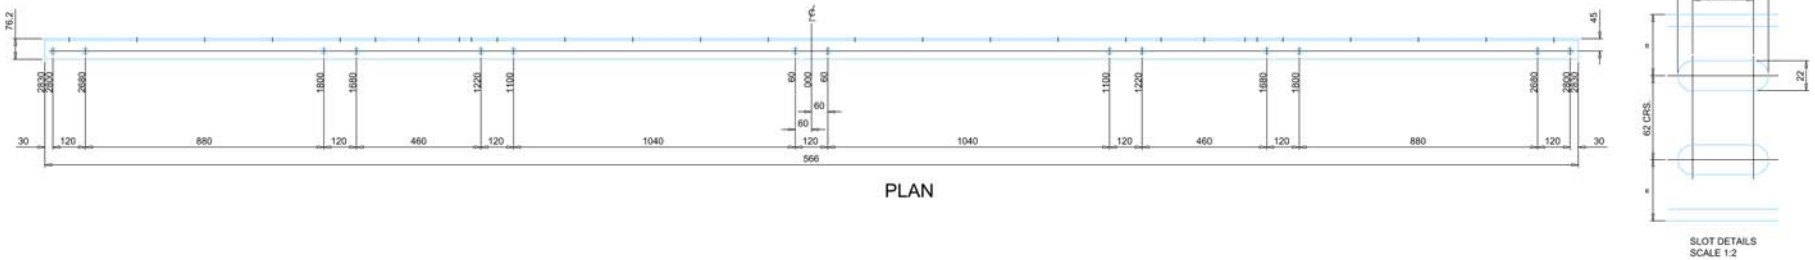

PLAN

SLOT DETAILS
SCALE 1:2

NOTE 1
INNER AND OUTER STIFFNER CHANNELS 0675 SHT50 ITEM 6 EACH FIXED WITH 10 OFF M20x50 LONG BOLTS.
TO BE READ IN CONJUNCTION WITH SHT4.

CE Electric UK		Lloyds Court, 78 Grey Street, Newcastle Upon Tyne, NE1 6AF	
Manufacturer Details		66KV OVERHEAD LINES - LARGE SECTION 'H' CROSSARM ASSEMBLY	
Sheet No. 5	Scale 1:10		
Prepared By Joan.Oakley		Type OVERHEAD	DOCUMENT_SUB_CLASS
Revised 04/06/10	Grid Reference	Ref No. C987600	Historic Drg.No. 1091231162
Date Issued 03/06/10	Checked By G HAMMEL	Revision	Notes