

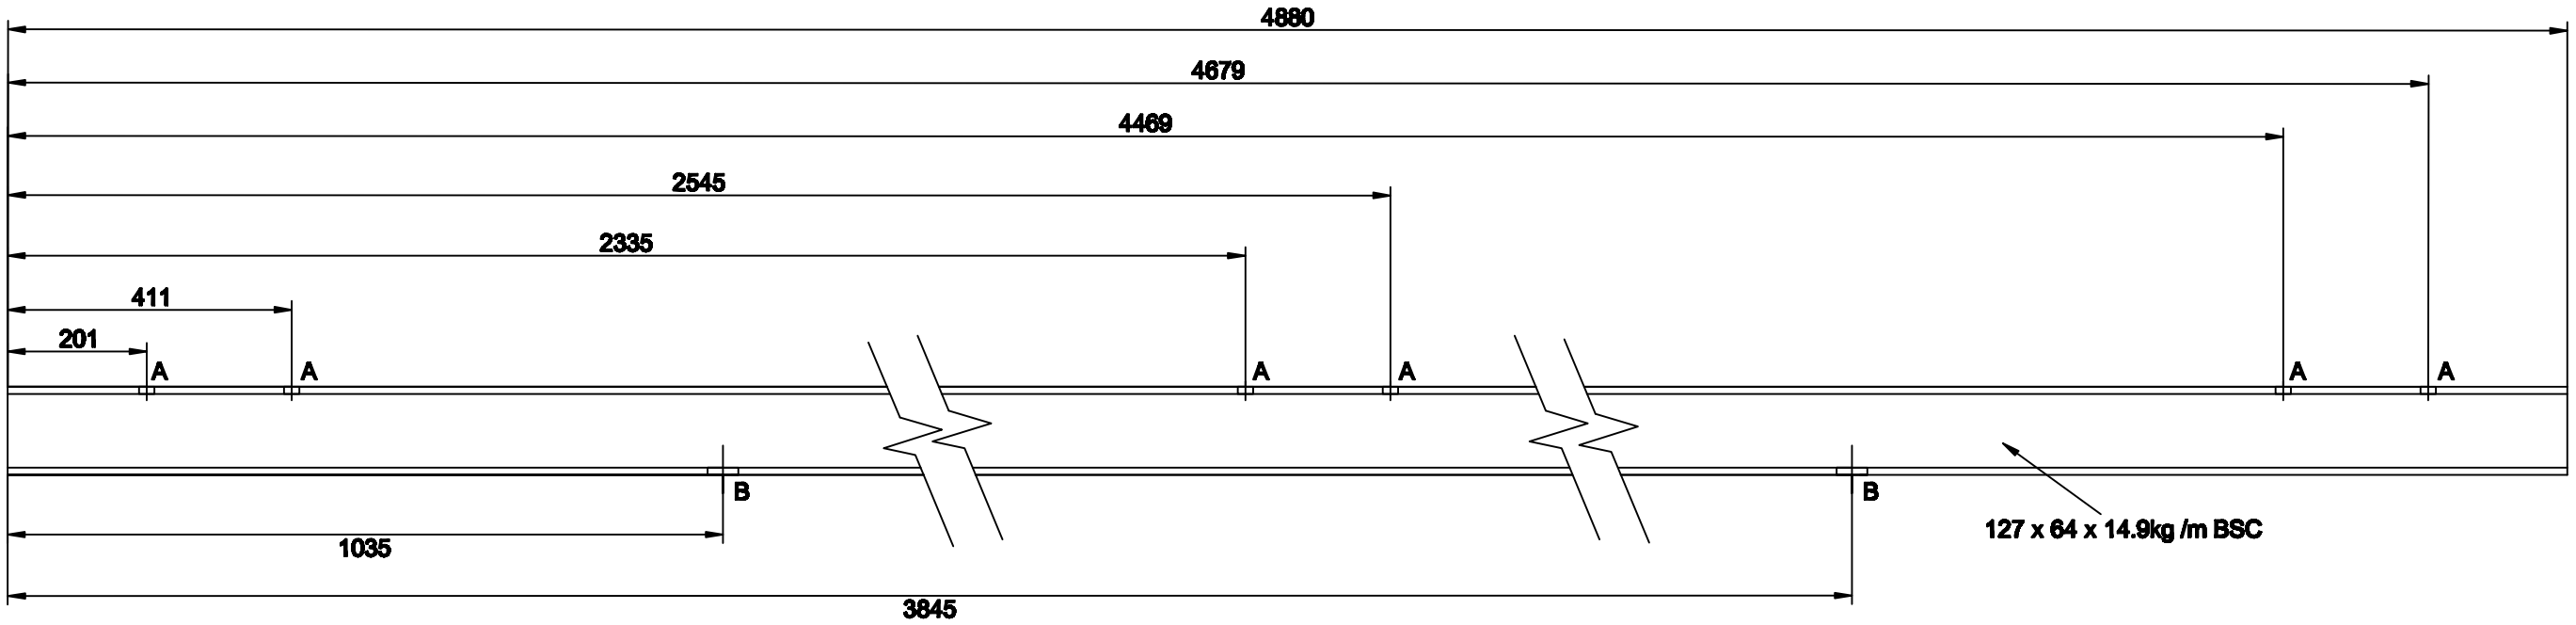



ITEM No 1
2 No REQUIRED

ELEVATION

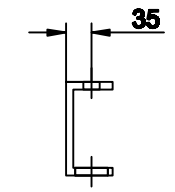


SIDE ELEVATION

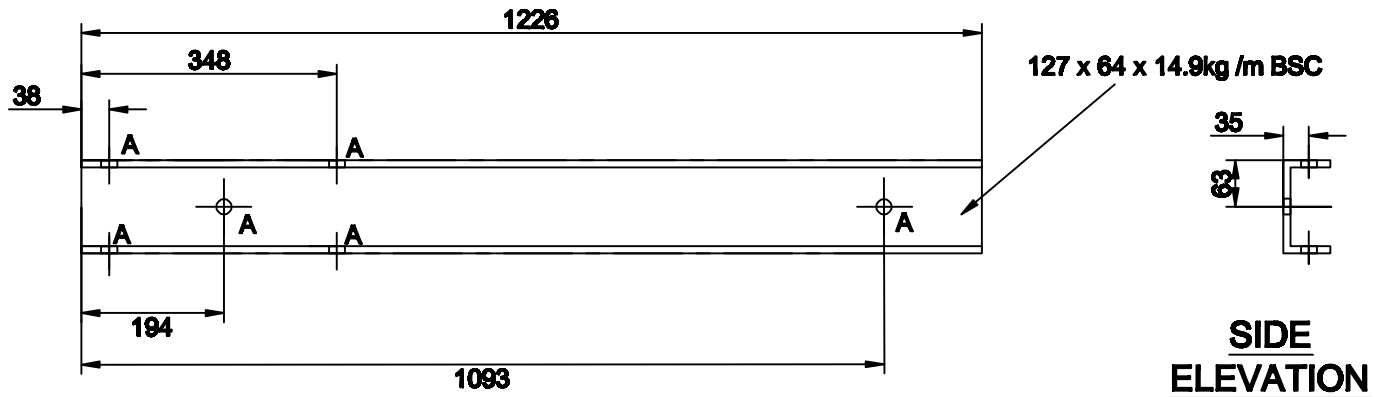



ELEVATION





SIDE ELEVATION

ITEM No 2
2 No REQUIRED

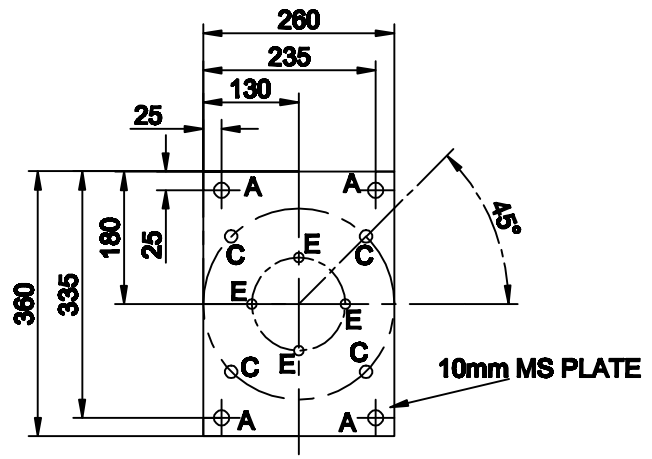


ITEM No 4
3 No REQUIRED

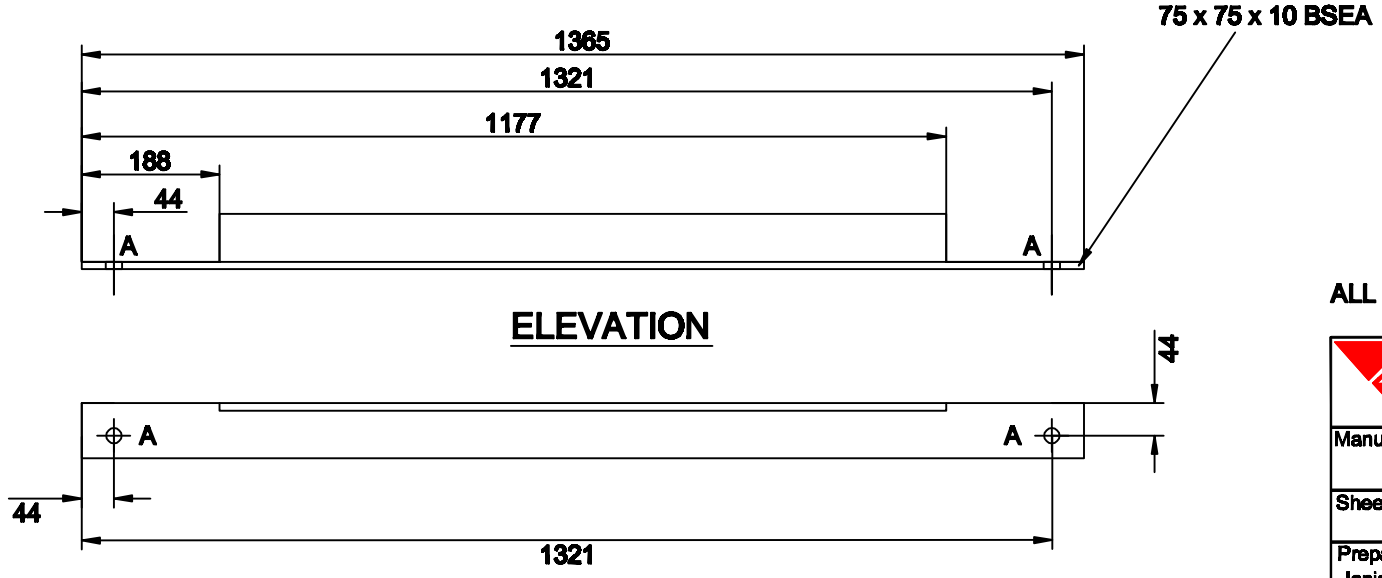


ELEVATION




PLAN

ITEM No 3
2 No REQUIRED

NOTES
1. HOLES MARKED 'A' 22 DIA
2. SLOTS MARKED 'B' 22 x 22 CENTRES
3. HOLES MARKED 'C' 18 DIA ON 210 PCD
   HOLES MARKED 'E' 14 DIA ON 127 PCD
4. ALL STEELWORK TO BS4848 PART 4 AND BS4360 GRADE 43A
5. GALVANISED IN ACCORDANCE WITH BS729

ALL DIMENSIONS SHOWN ARE IN MILLIMETRES UNLESS OTHERWISE STATED

| | | |
|---|---|---|
| CE Electric UK | | Lloyds Court, 78 Grey Street, Newcastle Upon Tyne, NE1 6AF |
| Manufacturer Details | | STEELWORK DETAIL FOR 66KV POLYMERIC CABLE TERMINATION AND PORCELAIN MB75 SURGE DIVERTOR PLATFORM CE/C/37 (M) |
| Sheet No. 1 | Scale 1:10 | |
| Prepared By Janis.Webb | | Type OVERHEAD LINES |
| Revised 15/05/07 | Grid Reference | Ref No. C948264 Historic Drg.No. Y204L0918 |
| Date Issued 10/05/07 | Checked By | Revision A Notes |