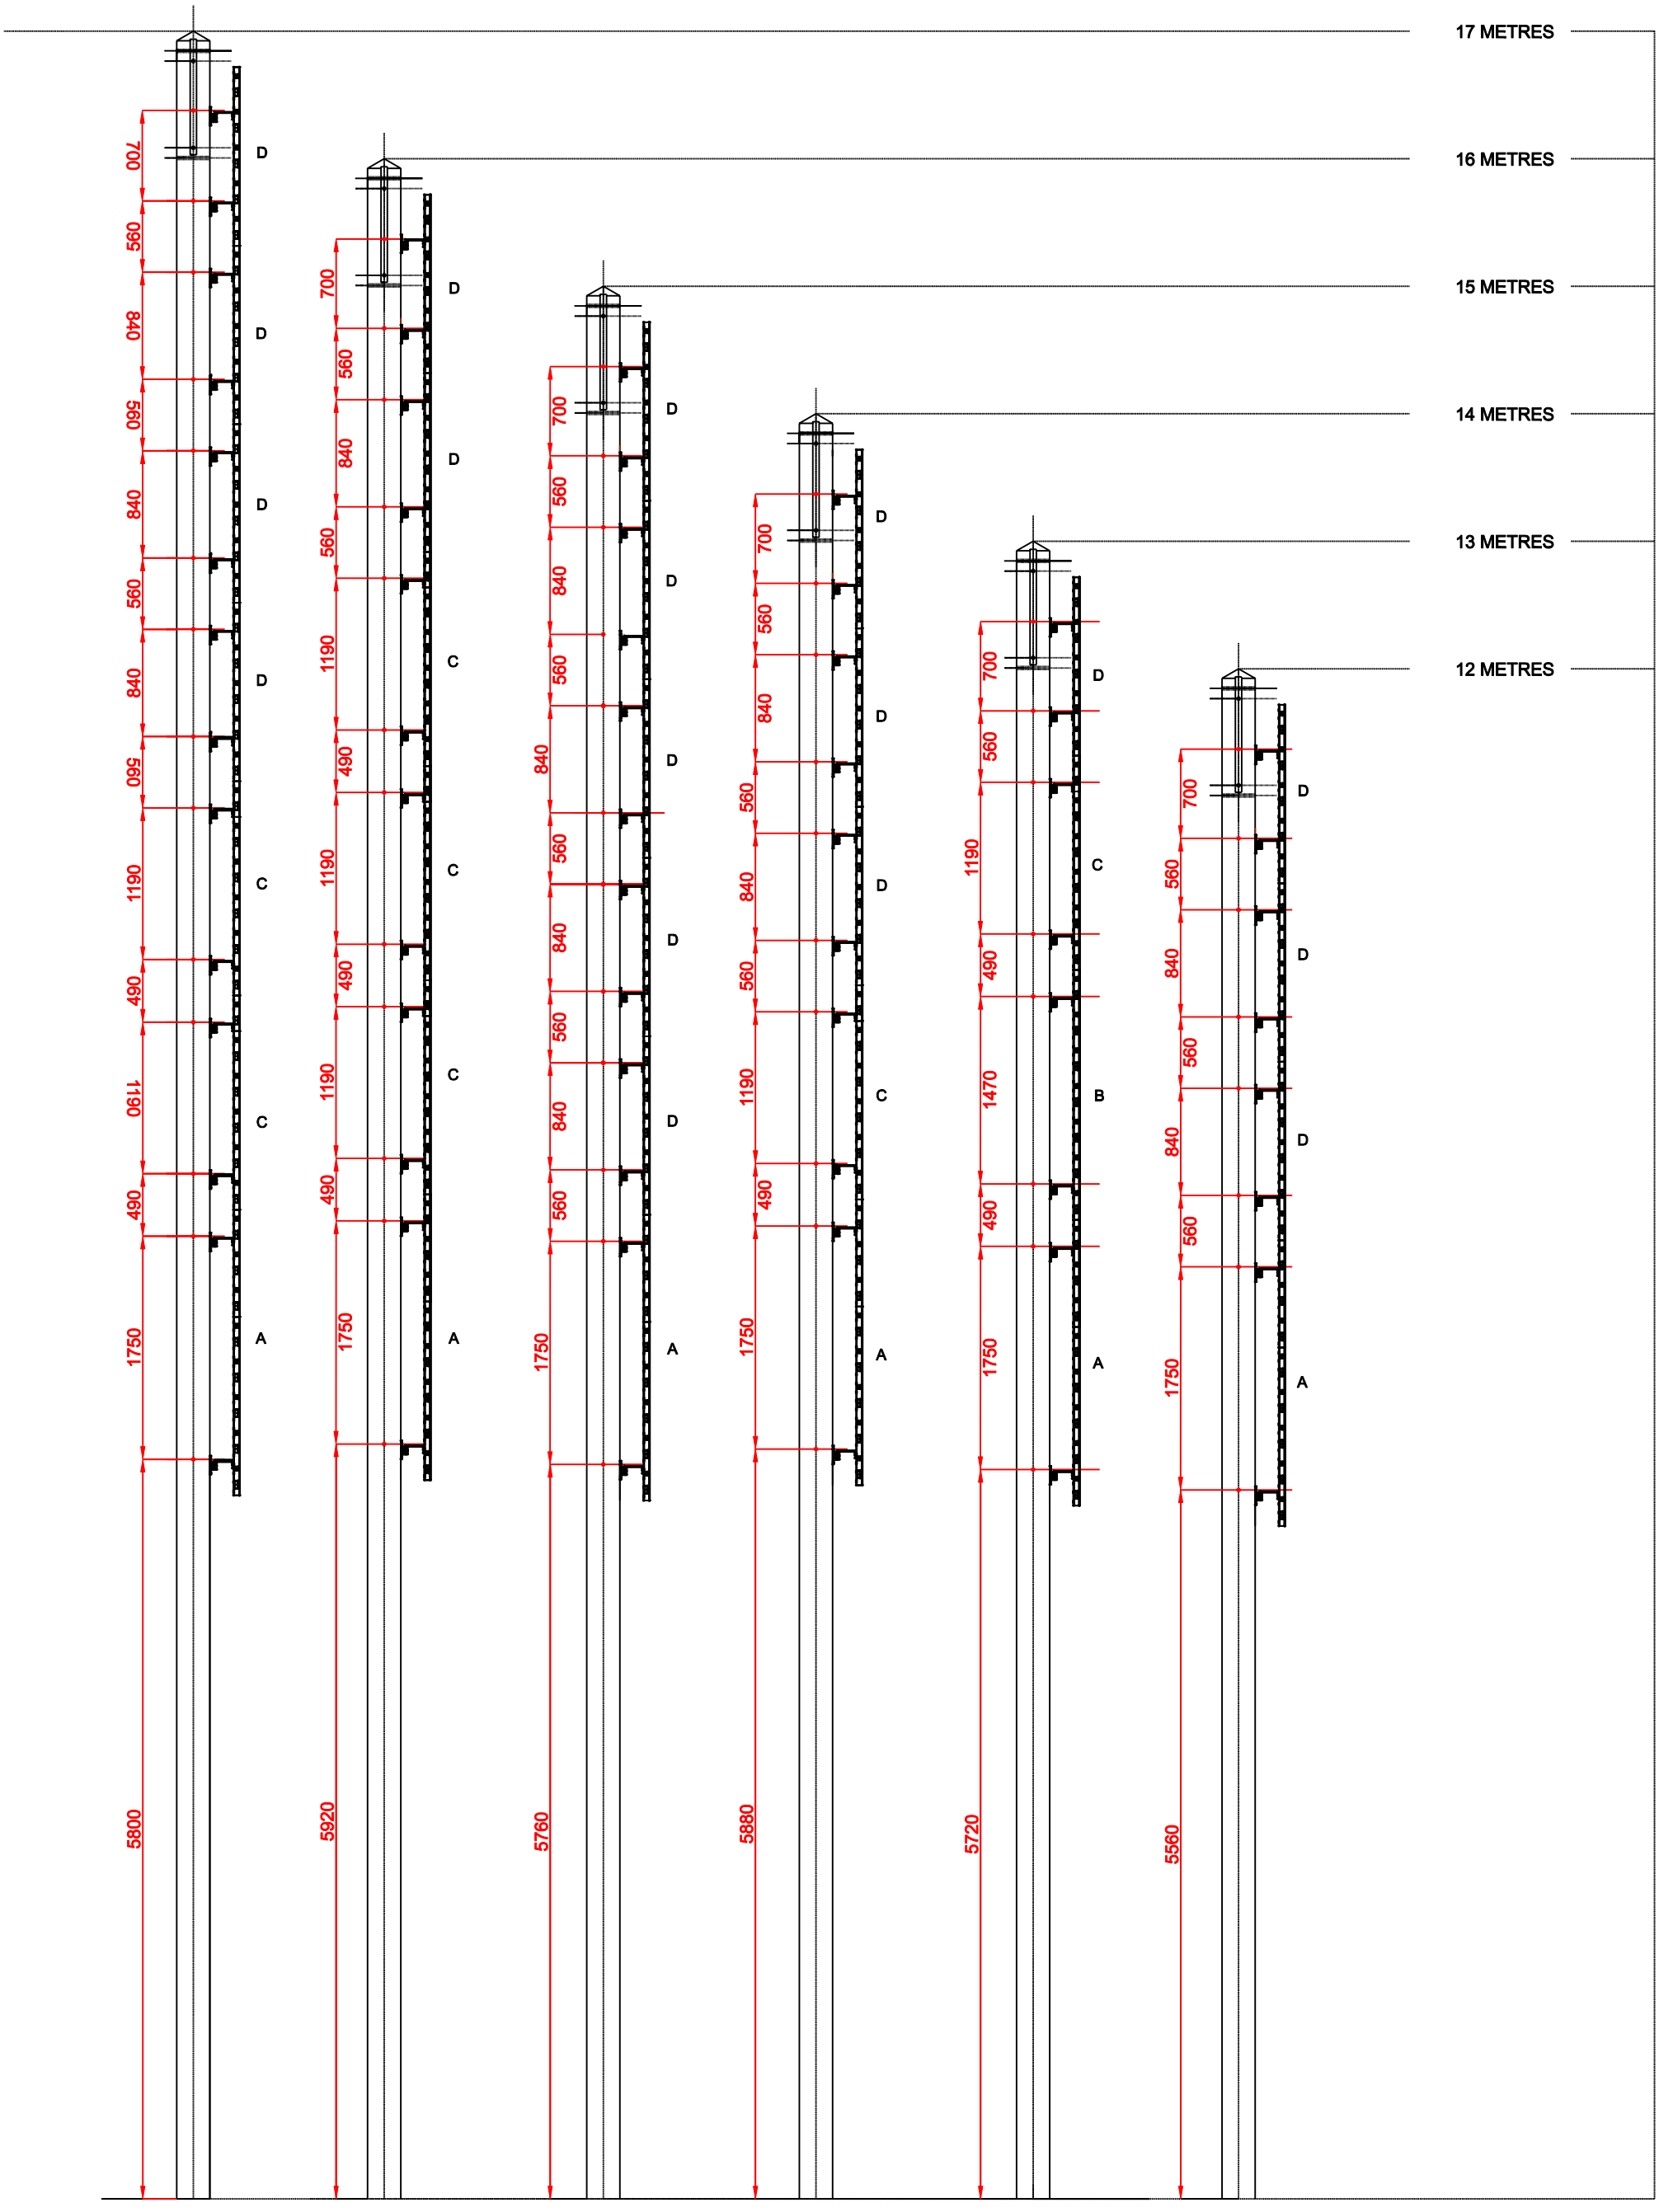



A = 2240R
B = 1960
C = 1680
D = 1400

CE Electric UK

Lloyds Court, 78 Grey Street, Newcastle Upon Tyne, NE1 6AF

Manufacturer Details

Sheet No. 3 | Scale 1:20

Prepared By Jamie.Webb

Revised 14/08/07 | Grid Reference

Date Issued 09/08/07 | Checked By G HAMMEL

ADDITIONAL FABRICATION DETAILS FOR THE ATTACHMENT OF THE HCL CLIMBING ACCESS SYSTEM TO DRAWING 1091390003 SHEET 2

Type OVERHEAD POLES

Ref No. C951143 | Historic Drg.No. 1091390003

Revision A | Notes

...\C951143 With ladder End and H 28/09/2007 11:57:26