



TYPICAL 17 METRE POLE SHOWN

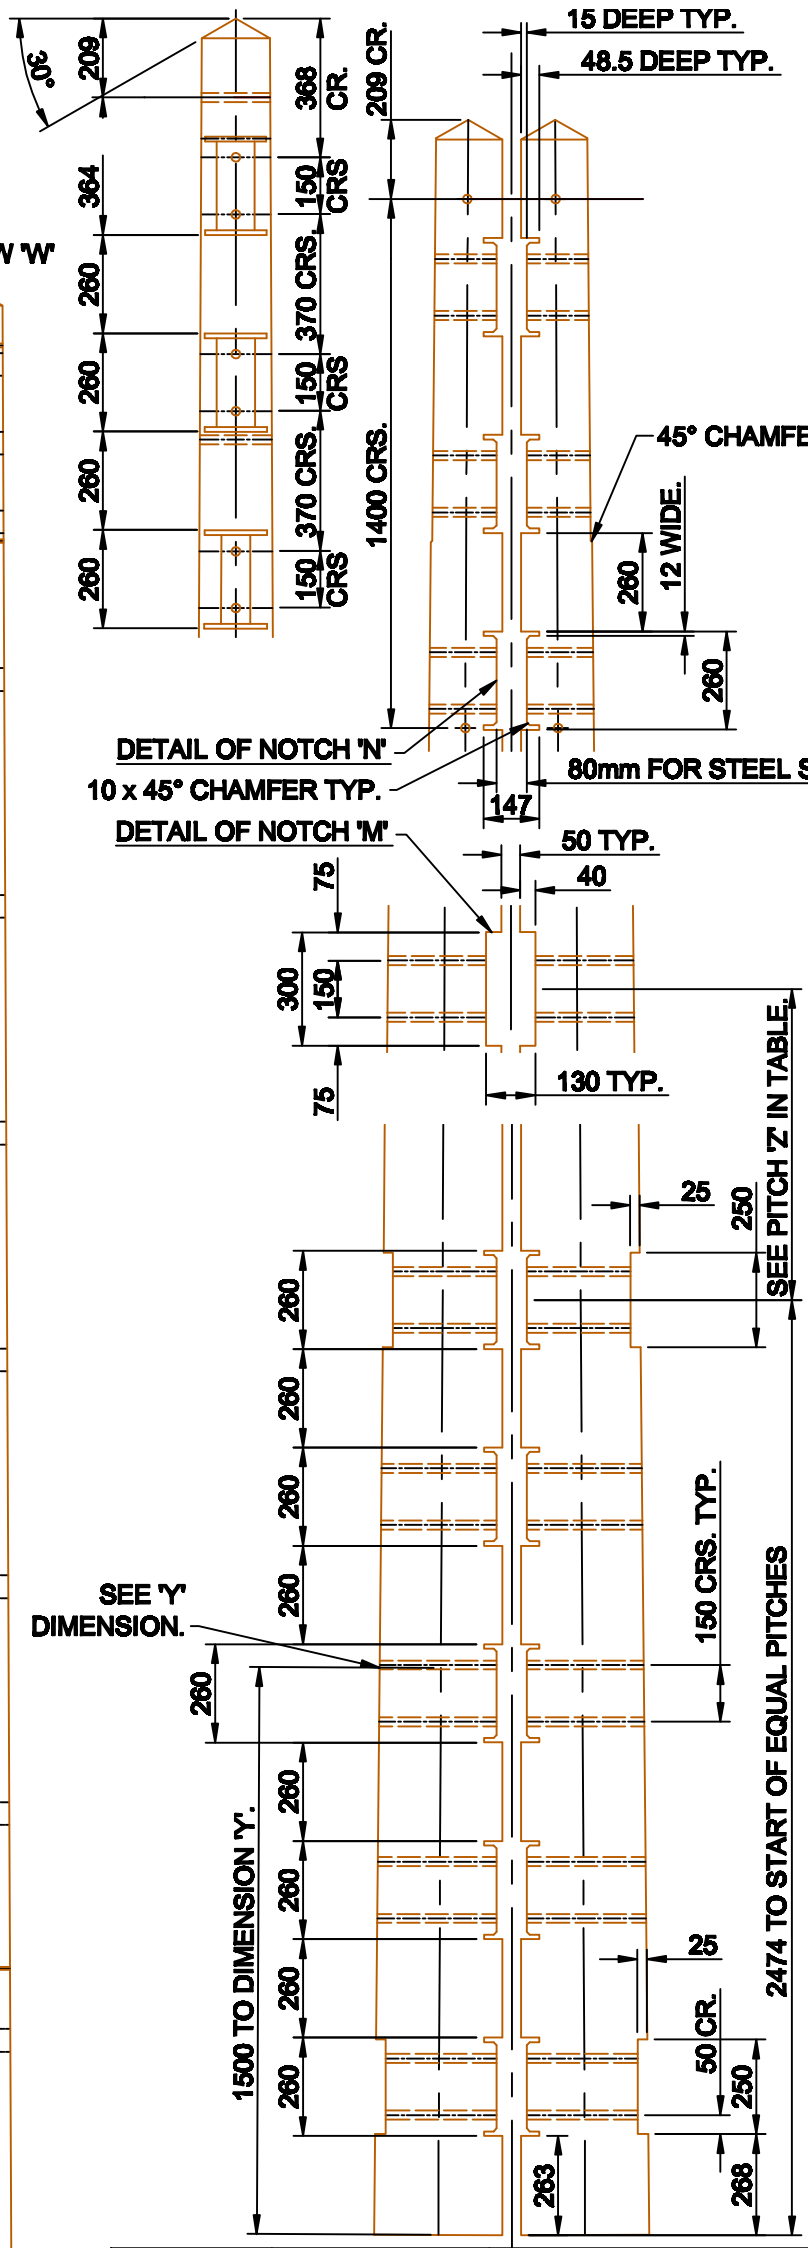

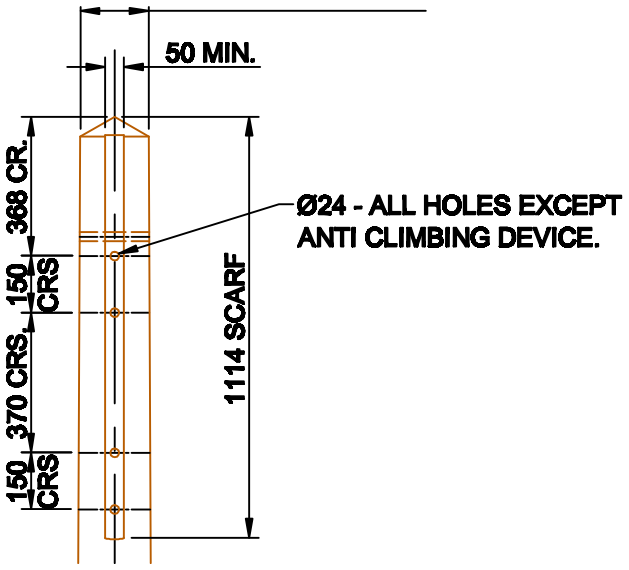

SCARFS AND HOLES ARE SYMMETRICAL ABOUT MAIN CENTRELINE.

SCALE 1:10

80mm FOR STEEL SHEAR BLOCK 1 09 101 0675 SHEET No.39

IMPORTANT NOTE

THE SCARF IS PARALLEL TO THE POLE EDGE & NOT THE POLE CENTRELINE.

SCARFING TO BE CUT TO GIVE A 50mm WIDE FLAT ON TWO DIAMETRICALLY OPPOSITE FACES WITH ENDS CHAMFERED AS SHOWN.

GENERAL NOTES

1. POLES TO BE SELECTED IN MATCHED PAIRS AND LAID OUT TO FACILITATE DRILLING SIMULTANEOUSLY.
2. CLASS OF POLE TO BE MEDIUM OR STOUT (SEE TABLE) IN ACCORDANCE WITH 1.09.101.0238 LENGTH & CLASS OF POLE TO BE IMPRESSED INTO EACH POLE BUTT.
3. POLE BUTT TO BE CUT AT RIGHT ANGLES TO AXIS OF POLE.
4. ALL HOLES EXCEPT WHERE STATED OTHERWISE TO BE 22mm DIA. DRILLED AT RIGHT ANGLES TO MAIN CENTRELINE OF POLE. ALL DRILLING & CUTTING TO BE DONE STRICTLY TO TEMPLATE PRIOR TO CREOSOTING.
5. SHEAR BLOCK NOTCHES SHOULD BE MARKED OFF SIMULTANEOUSLY ON PAIRED POLES & DRILLED TO ACCOMMODATE FIXINGS TOGETHER.
6. NOTCHES SHOWN (17 METRE POLE) ARE CUT FROM THE BASE AS A DATUM.

 FOR NOTCH 'M' & 'N' SEE DETAIL.
7. GAUGE MARKINGS TO BE IMPRESSED 4500mm FROM POLE BUTT, SEE 'GM'.
8. SEE SHEET 3 FOR HOLES OF CLIMBING SYSTEM

ITEM	POLE HEIGHT	DIMENSION 'X' (Min/ Max)	DIMENSION 'Y' (Min/ Max)	PITCH 'Z'	POLE CLASS
A MEDIUM	12000 mm	Ø150 mm - Ø190 mm	Ø250 mm - Ø305 mm	4 x 1400	MEDIUM
A STOUT	12000 mm	Ø190 mm - Ø224 mm	Ø305 mm - Ø337 mm	4 x 1400	STOUT
B MEDIUM	13000 mm	Ø160 mm - Ø195 mm	Ø260 mm - Ø320 mm	5 x 1350	MEDIUM
B STOUT	13000 mm	Ø195 mm - Ø230 mm	Ø320 mm - Ø353 mm	5 x 1350	STOUT
C MEDIUM	14000 mm	Ø160 mm - Ø195 mm	Ø275 mm - Ø335 mm	5 x 1500	MEDIUM
C STOUT	14000 mm	Ø195 mm - Ø230 mm	Ø335 mm - Ø368 mm	5 x 1500	STOUT
D MEDIUM	15000 mm	Ø165 mm - Ø195 mm	Ø290 mm - Ø350 mm	6 x 1450	MEDIUM
D STOUT	15000 mm	Ø195 mm - Ø230 mm	Ø350 mm - Ø386 mm	6 x 1450	STOUT
E MEDIUM	16000 mm	Ø170 mm - Ø200 mm	Ø305 mm - Ø365 mm	7 x 1400	MEDIUM
E STOUT	16000 mm	Ø200 mm - Ø236 mm	Ø365 mm - Ø402 mm	7 x 1400	STOUT
F MEDIUM	17000 mm	Ø180 mm - Ø200 mm	Ø320 mm - Ø375 mm	7 x 1500	MEDIUM
F STOUT	17000 mm	Ø200 mm - Ø236 mm	Ø375 mm - Ø412 mm	7 x 1500	STOUT

CE Electric UK

Lloyds Court, 78 Grey Street, Newcastle Upon Tyne, NE1 6AF

132KV OVERHEAD LINES DRILLING, SCARFING & MARKINGS FOR RUTTER TYPE MEDIUM & STOUT POLES FOR USE WITH TIMBER & HEAVY DUTY STEEL SHEAR BLOCKS

Manufacturer Details			
Sheet No. 2	Scale AS SHOWN		
Prepared By Janis.Webb		Type OVERHEAD	DOCUMENT_SUB_CLASS
Revised 21/08/07	Grid Reference	Ref No. C949714	Historic Drg.No. 1091390008
Date Issued	Checked By		