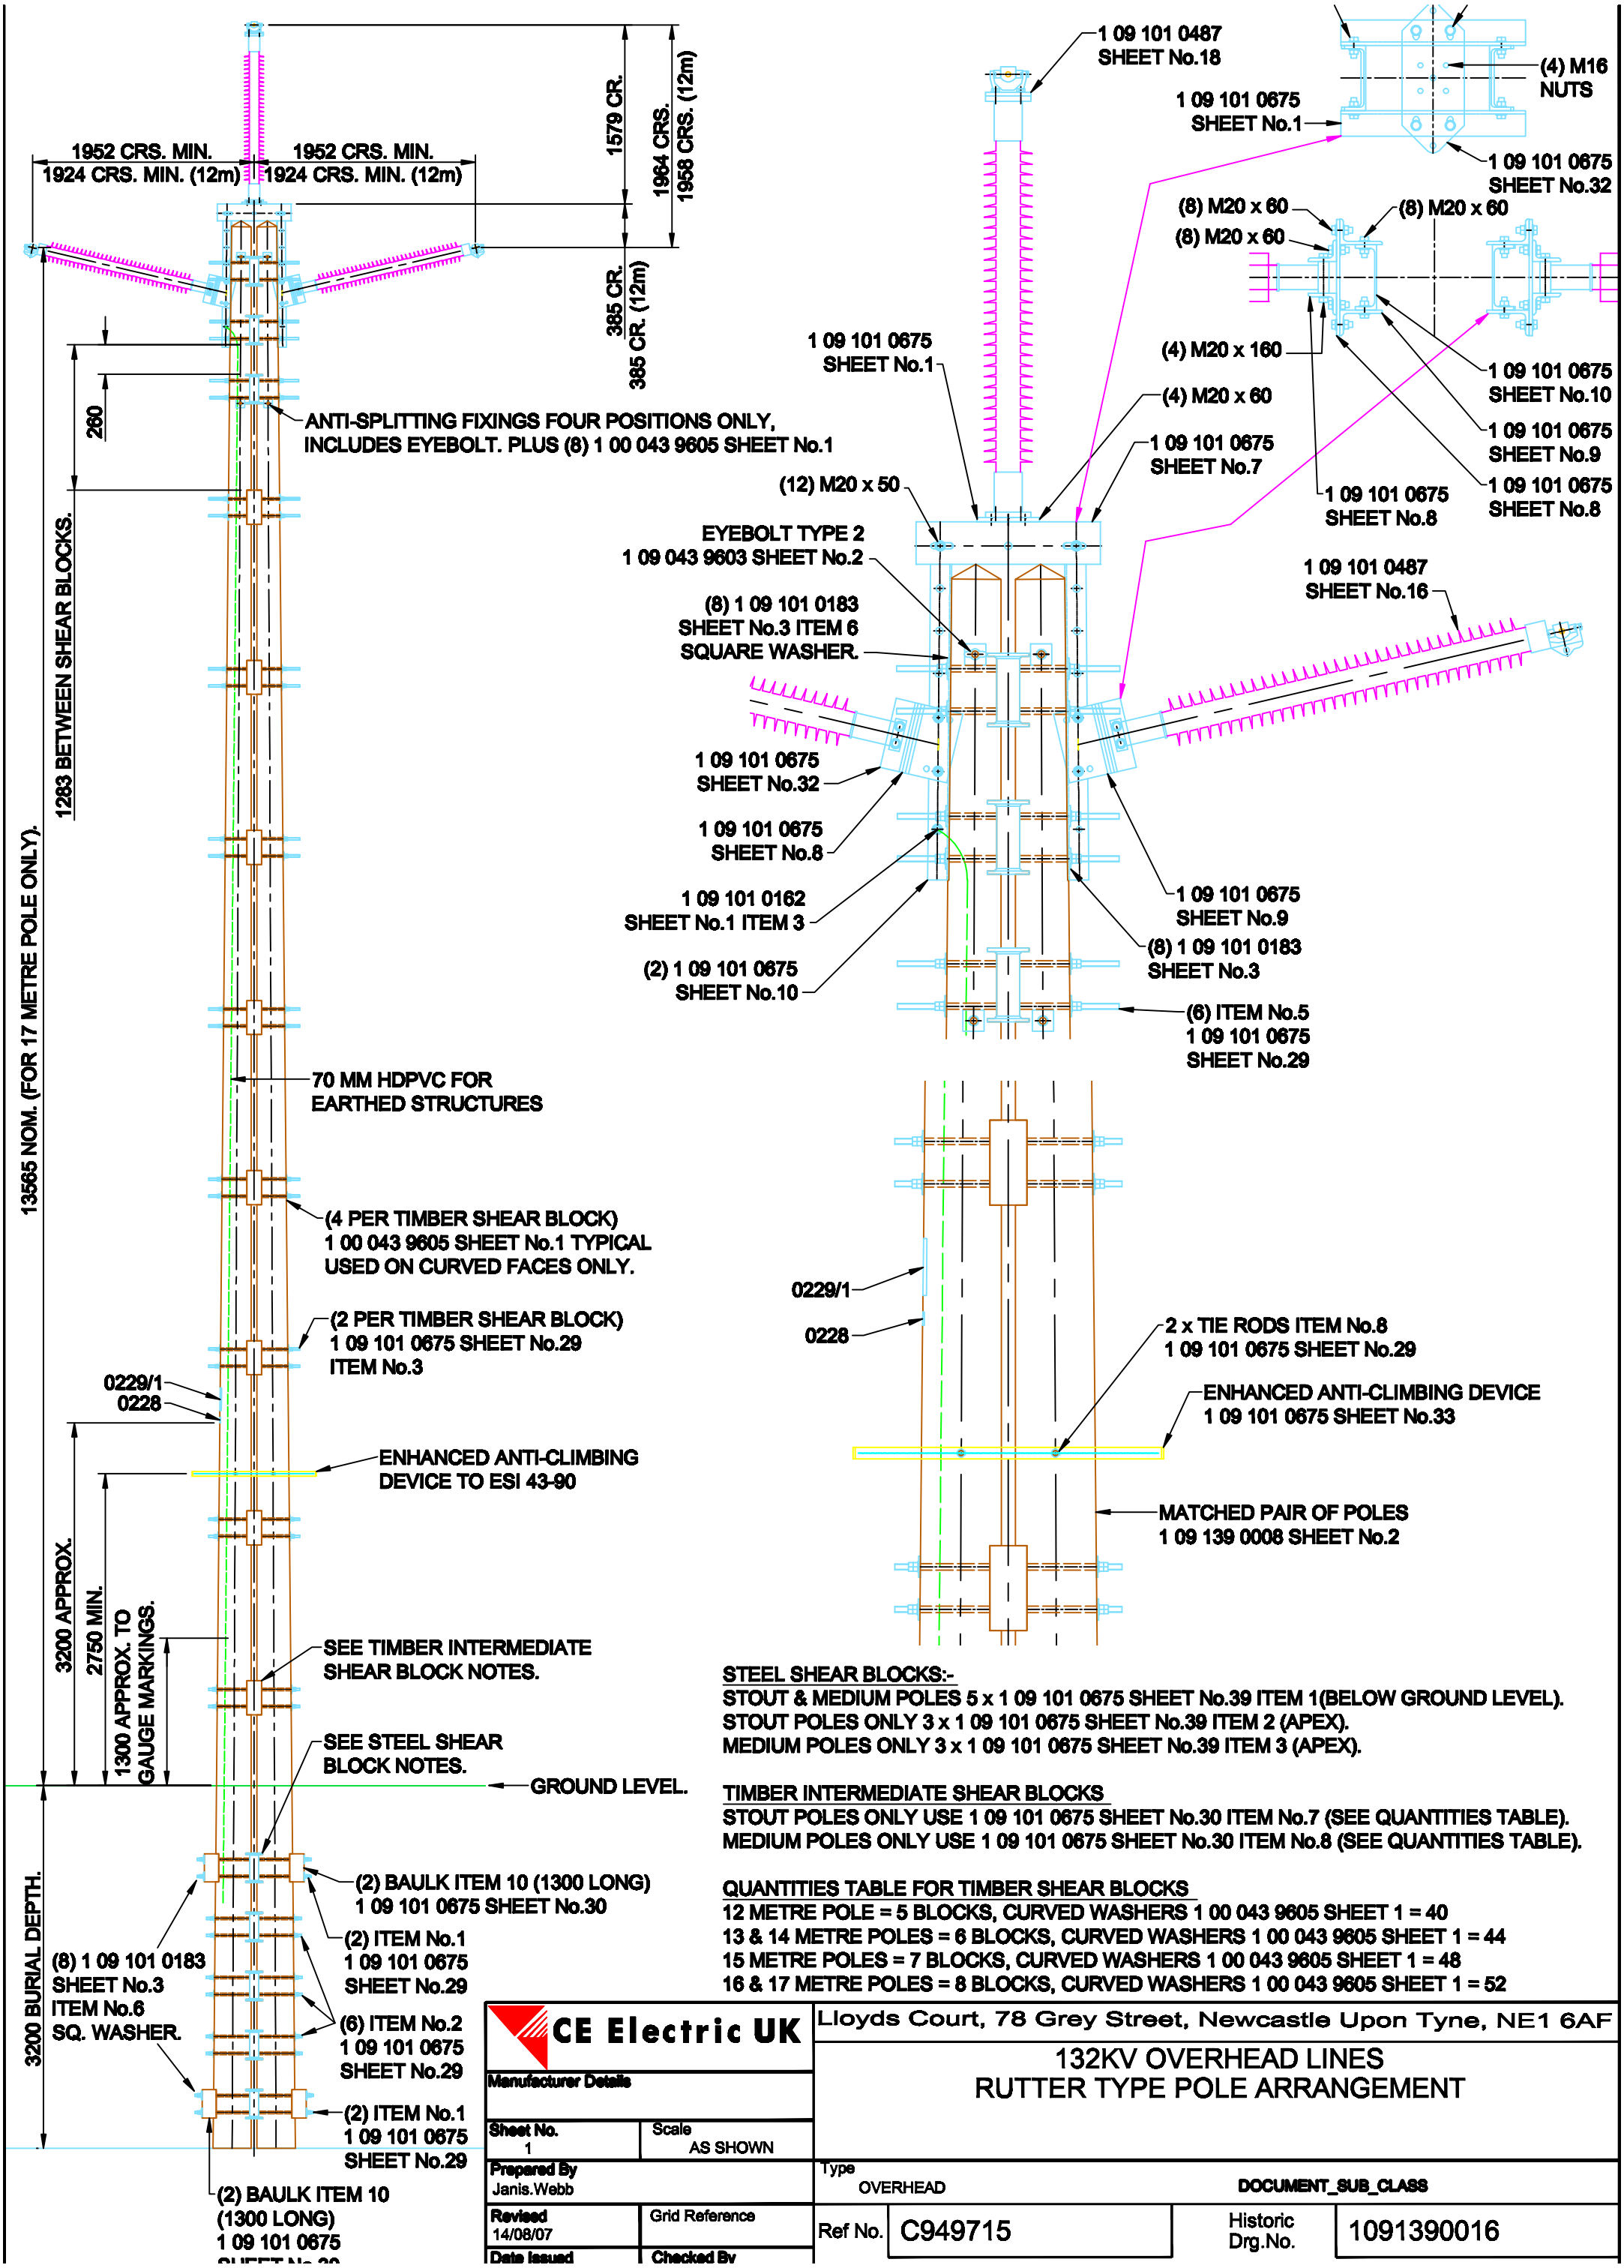


STEEL SHEAR BLOCKS:-
STOUT & MEDIUM POLES 5 x 1 09 101 0675 SHEET No.39 ITEM 1(BELOW GROUND LEVEL).
STOUT POLES ONLY 3 x 1 09 101 0675 SHEET No.39 ITEM 2 (APEX).
MEDIUM POLES ONLY 3 x 1 09 101 0675 SHEET No.39 ITEM 3 (APEX).

TIMBER INTERMEDIATE SHEAR BLOCKS
STOUT POLES ONLY USE 1 09 101 0675 SHEET No.30 ITEM No.7 (SEE QUANTITIES TABLE).
MEDIUM POLES ONLY USE 1 09 101 0675 SHEET No.30 ITEM No.8 (SEE QUANTITIES TABLE).

QUANTITIES TABLE FOR TIMBER SHEAR BLOCKS
12 METRE POLE = 5 BLOCKS, CURVED WASHERS 1 00 043 9605 SHEET 1 = 40
13 & 14 METRE POLES = 6 BLOCKS, CURVED WASHERS 1 00 043 9605 SHEET 1 = 44
15 METRE POLES = 7 BLOCKS, CURVED WASHERS 1 00 043 9605 SHEET 1 = 48
16 & 17 METRE POLES = 8 BLOCKS, CURVED WASHERS 1 00 043 9605 SHEET 1 = 52

CE Electric UK

Lloyds Court, 78 Grey Street, Newcastle Upon Tyne, NE1 6AF

132KV OVERHEAD LINES
RUTTER TYPE POLE ARRANGEMENT

Manufacturer Details			
Sheet No. 1	Scale AS SHOWN		
Prepared By Janis.Webb		Type OVERHEAD	DOCUMENT_SUB_CLASS
Revised 14/08/07	Grid Reference	Ref No. C949715	Historic Drg.No. 1091390016
Date Issued	Checked By		