

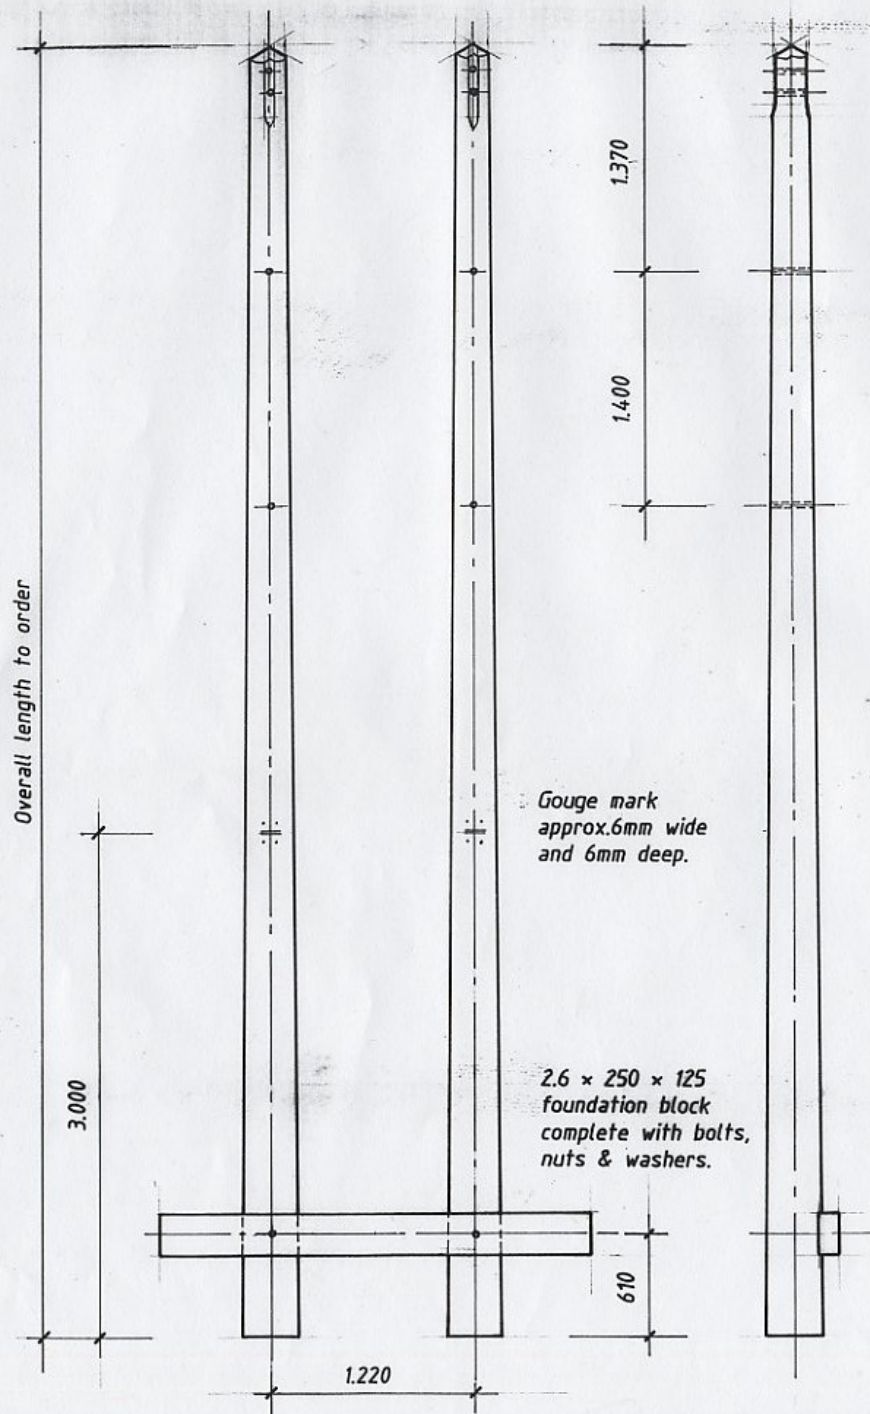


Overall length to order

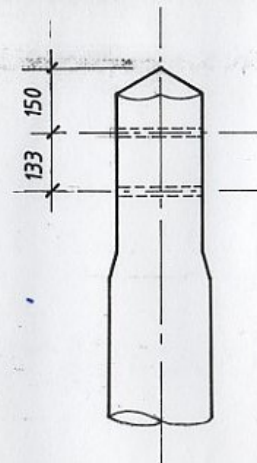

420 scarfing

355 flat

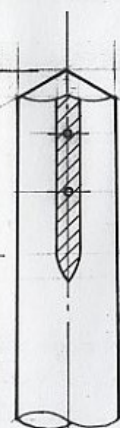


pole top detail

H POLES TO BE MATCHED


All drillings 22mm ϕ .

REFERENCE

11.5 - Length of pole (m)
 310 - Dia. of pole 1.5m from butt.
 I.F. - Imported rd fir.
 99 - Year of preservation.
 xyz - Suppliers name or mark.

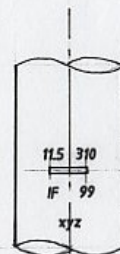

markings

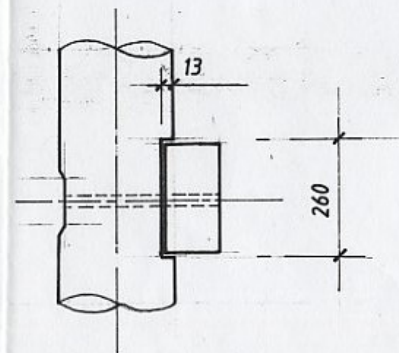

foundation block

REVISIONS

NORWEB plc
 Grid & Primary Systems

DRAWN d.j.m. TRACED

APPROVED DATE 27.04.00

Drilling & scarfing details
 for 33kV 'H' type
 terminal pole.
 OHL/HC/70M construction.
 with terminal crossarm.

SCALE n.t.s.

DRAWING NUMBER

SHEET

LD · A3 · 71993