


Elevation Front

Scale: 1 : 20

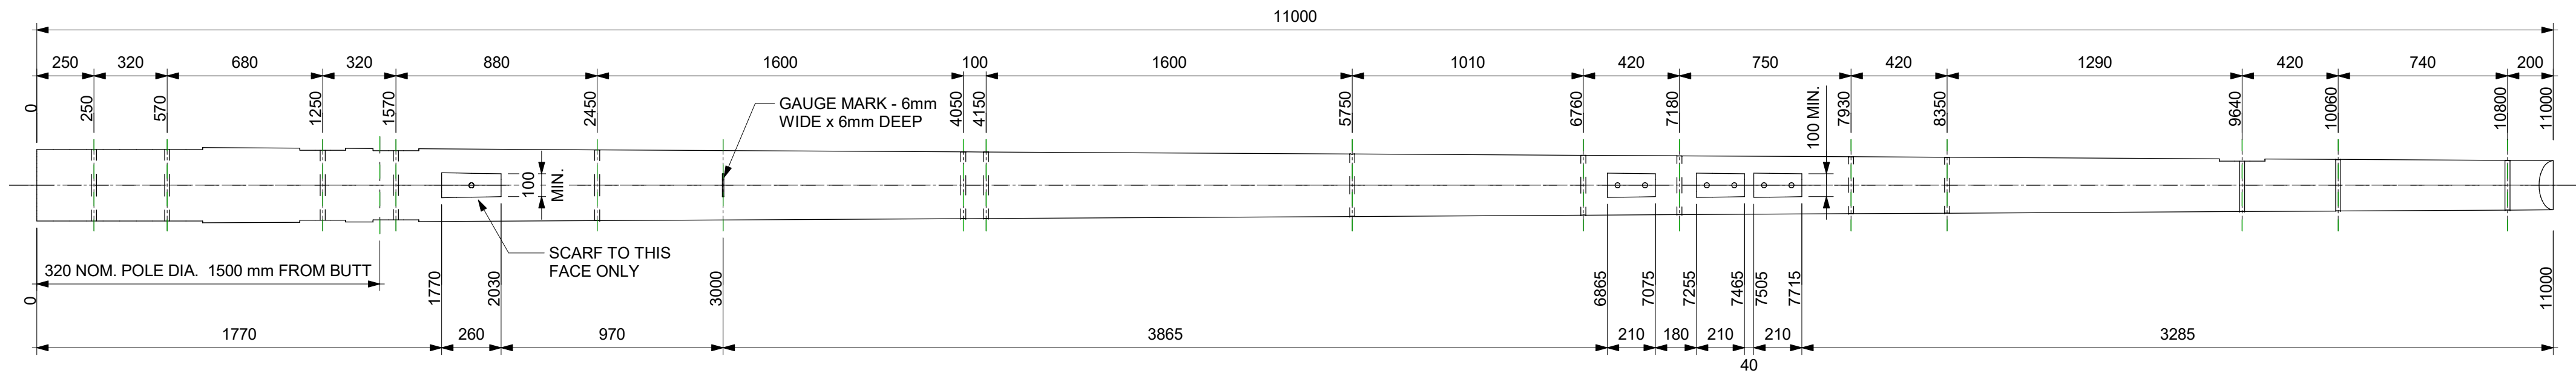

Elevation Side

Scale: 1 : 20

- 230mm MINIMUM NOMINAL POLE DIAMETER AT TIP
- ALL HOLES TO BE 22mm DIA. U.N.O.
- 11m LONG EXTRA STOUT WOOD POLE

0 100
This drawing may have been reduced original scale : 100mm

Reference Drawings Legend Notes

NOTES:-
1. ALL DIMENSIONS ARE IN MILLIMETRES (mm) U.N.O.
2. THIS DRAWING IS TO BE READ IN CONJUNCTION WITH DRAWING 20123S-BHK-0608-XX-DR-E-041153

THIS DRAWING TO BE PRINTED IN COLOUR

MORGAN SINDALL INFRASTRUCTURE

FOR ACCEPTANCE

FOR ACCEPTANCE		Drawn	Iss
01	Description	Date	11/03/21
Revisions		Checked	JN
		Approved	LGW



MORGAN
SINDALL
INFRASTRUCTURE

BakerHicks.

Project	PROJECT VISTA SLOY 132KV CABLE WORKS		
Title	AUXILLARY FRONT WOOD POLE SCARFING & DRILLING DETAILS		

Scale	As indicated	Drawn	MHJ	Checked	JN	Approved	LGW
(when plotted @ A1)	Date	11/03/21	Date	11/03/21	Date	11/03/21	
CAD Ref	S:\London\Projects\30001852-3 - SSEN VISTA 132KV Sloy & Falloch\10_CAD\03_BH08_hv\Sloy\Drawing & Model Information (WIP)\Revit\30001852-BH-SG-ZZ-403-E-0001.rvt						

BH Project number	30001852	Revision	01
-------------------	----------	----------	----

MS Project number	MS Drawing number
MS20123	20123S-BHK-0608-XX-DR-E-041155

SSEN Project number	SSEN Drawing number
LT186	0041-132kV-UGC SG1 SG2-DET-1110-1001-01