


Elevation Front

Scale: 1 : 20

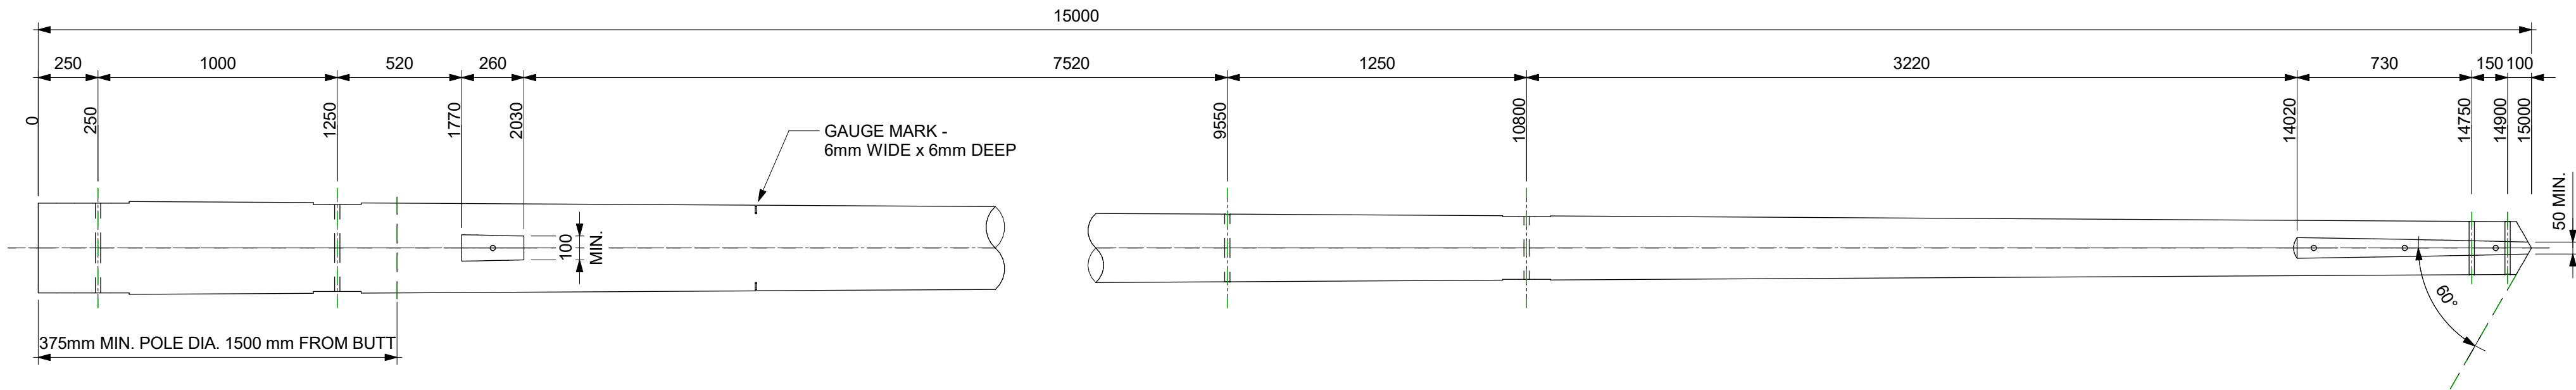

Elevation Side

Scale: 1 : 20

- 220mm MINIMUM NOMINAL POLE DIAMETER AT TIP.
- ALL HOLES TO BE 22mm DIA. U.N.O.
- 15m LONG EXTRA STOUT WOOD POLE



Reference Drawings	Legend	Notes
--------------------	--------	-------

- NOTES:-**
1. ALL DIMENSIONS ARE IN MILLIMETRES (mm) U.N.O.
 2. THIS DRAWING IS TO BE READ IN CONJUNCTION WITH DRAWING 20123S-BHK-0608-XX-DR-E-041153

THIS DRAWING TO BE PRINTED IN COLOUR

MORGAN SINDALL INFRASTRUCTURE

FOR ACCEPTANCE

FOR ACCEPTANCE		Drawn	Issd	Date	Checked	Approved
01	Description			11/03/21	JN	LGW
Revisions						



MORGAN SINDALL

INFRASTRUCTURE

BakerHicks.

Project	PROJECT VISTA SLOY 132KV CABLE WORKS		
Title	TERMINAL WOOD POLE SCARFING & DRILLING DETAILS		

Scale	As indicated	Drawn	MHJ	Checked	JN	Approved	LGW
(when plotted @ A1)	Date	11/03/21	Date	11/03/21	Date	11/03/21	
CAD Ref	S:\London\Projects\30001852-3 - SSEN VISTA 132KV Sloy & Falloch\10_CAD\03_BH08_Inv\Sloy\Drawing & Model Information (WIP)\Revit\30001852-BH-SG-ZZ-403-E-0001.rvt						

BH Project number	30001852	Revision	01
-------------------	----------	----------	----

MS Project number	MS20123	MS Drawing number	20123S-BHK-0608-XX-DR-E-041156
-------------------	---------	-------------------	--------------------------------

SSEN Project number	LT186	SSEN Drawing number	0041-132kV-UGC SG1 SG2-DET-1110-1002-01
---------------------	-------	---------------------	---