

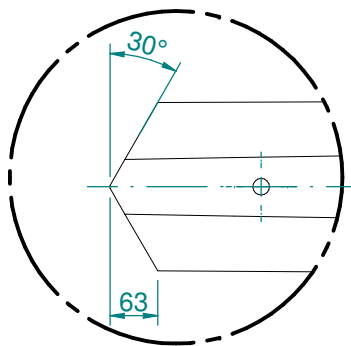



BAR MARK	SECTION SIZE / PLATE SIZE	MASS (kg)	COMMENTS / MATERIAL
435005	ENA TS 43-88 EXTRA STOUT	VARIES	EXTRA STOUT WOOD POLE ENA TS 43-88 Appendix A

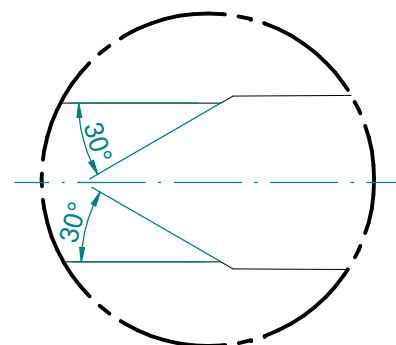

DETAIL A

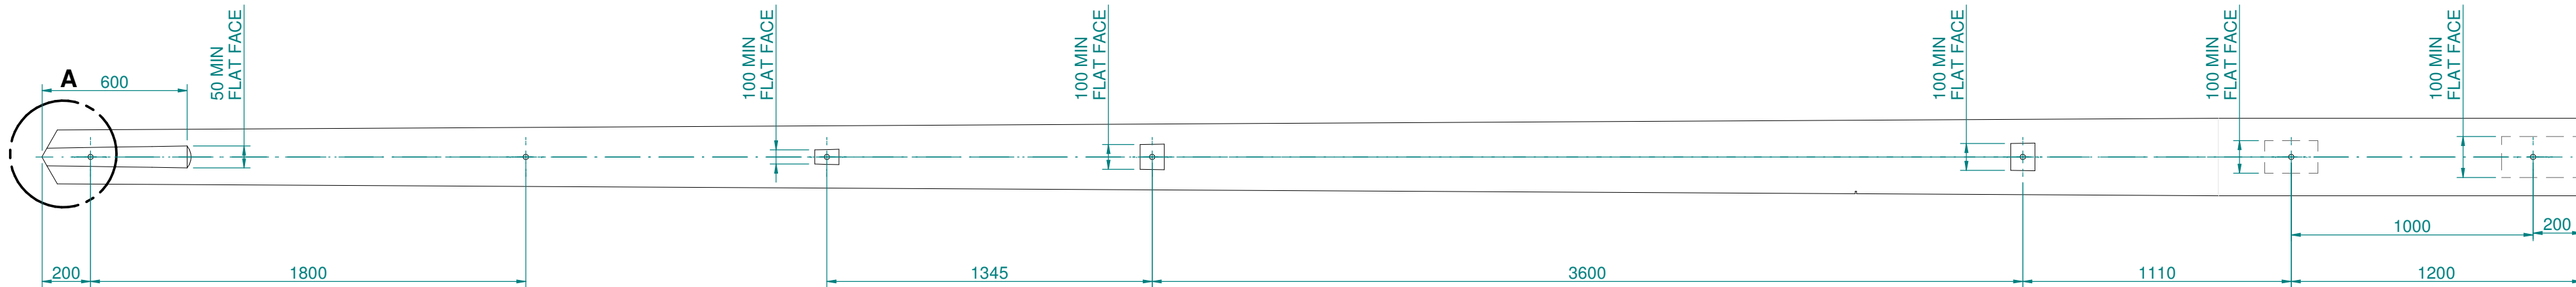

DETAIL C

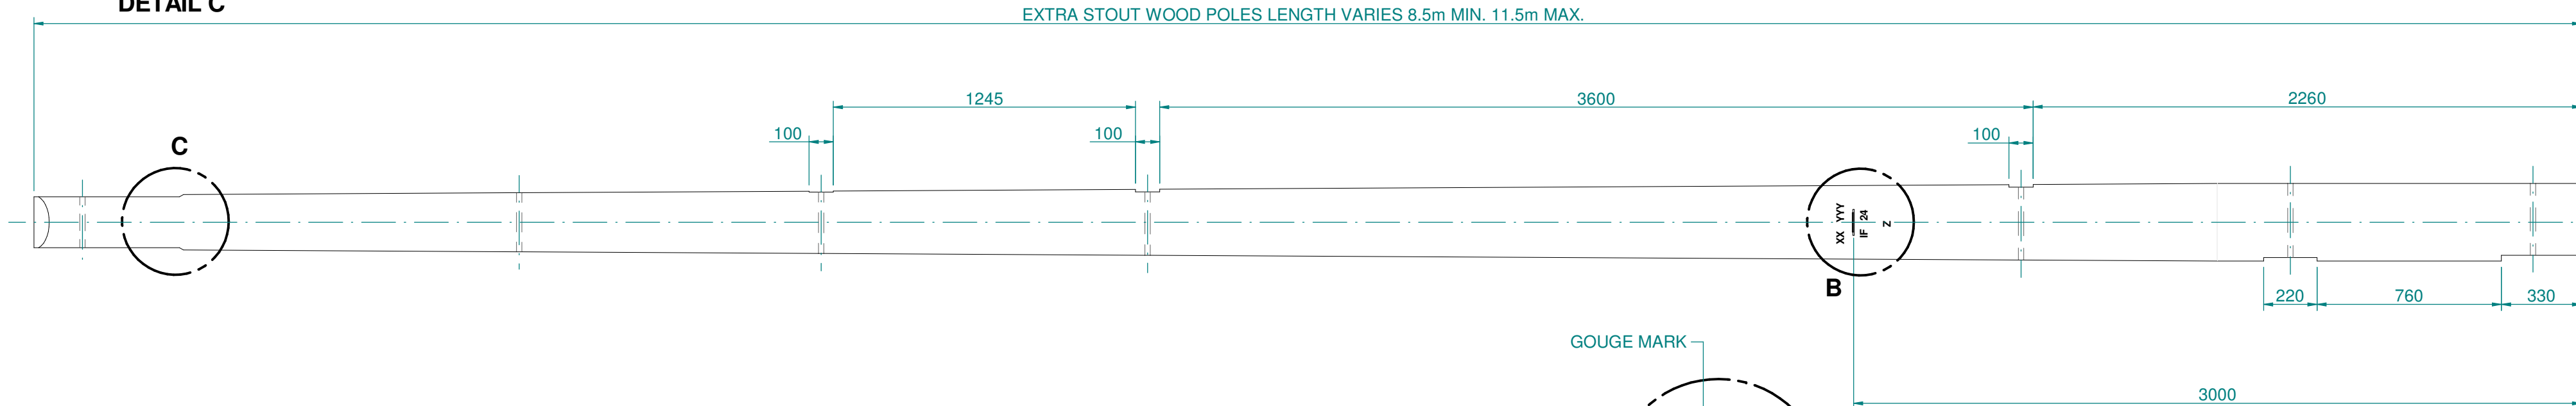


ALL HOLES TO BE Ø22mm
UNLESS NOTED OTHERWISE

EXTRA STOUT WOOD POLES LENGTH VARIES 8.5m MIN. 11.5m MAX.

POLE LENGTH
AND CLASS
TO BE
IMPRESSED
ON POLE BUTT

GENERAL NOTES:

- ALL DIMENSIONS ARE IN MILLIMETRES (mm).
- WOOD POLES SHALL BE FABRICATED IN ACCORDANCE WITH BS EN 14229 AND ENATS 43-88.
- ALL HOLES TO BE DRILLED AT RIGHT ANGLES TO THE CENTRE LINE OF THE POLE.
- ALL DRILLING AND CUTTING TO BE DONE STRICTLY TO TEMPLATE PRIOR TO PRESERVATION TREATMENT.
- POLE BUTT TO BE CUT AT RIGHT ANGLES TO AXIS OF POLE.

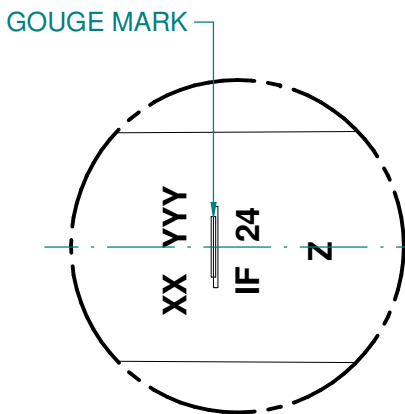

DETAIL B

GOUGE MARK REFERENCE DETAILS

XXm - POLE LENGTH
YYY - POLE DIAMETER @ 1.5m FROM BUTT
IF - IMPORTED FIR
24 - YEAR OF CREOSOTING
Z - SUPPLIERS MARK / NAME

GOUGE MARK 6mm WIDE x 6mm DEEP AT 3.0m FROM POLE BUTT

PLPC LTD

Issued for Construction

Date 05/06/25

REV	A	DATE	27/11/2024	BY	CM	CHKD	RF/MB	APPD	MA
DESCRIPTION									
FIRST ISSUE									
CDM RESIDUAL RISK ☐ DESIGN BASED HAZARDS ARE ACTIVELY ELIMINATED WHERE PRACTICAL. WHERE HAZARDS ARE NOT ELIMINATED THEY ARE IDENTIFIED BY THIS SYMBOL. ☐ HAZARDS / RISKS THAT SHOULD BE CONSIDERED BY A COMPETENT CONTRACTOR ARE NOT IDENTIFIED									
DESIGN NOTE ☐ FOCAL POINT OF DESIGN (EG. NEW STEELWORK, ADDITIONAL LINKS, ETC...) ARE IDENTIFIED BY THIS SYMBOL.									

LSTC GROUP http://www.lstc.co.uk Tel : 01377 253617	IF IN DOUBT ASK ENGINEER / DESIGN OFFICE		CLIENT PLPC LTD POWER LINE SPECIALISTS PROJECT MARKHILL - CHIRMORIE WF 132kV OHL CONNECTION	TITLE GENERIC SCARFING DETAIL CABLE TERMINAL AUXILIARY EXTRA STOUT WOOD POLE (ENATS 43-50)	SCALE 1:20	TOTAL No. OF SHEETS -	DESIGNED LSTC
	VIEW CONVENTION THIRD ANGLE				DATE 27/11/2024	CHECKED RF/MB	
	THIS DRAWING IS THE EXCLUSIVE PROPERTY OF THE CLIENT THE CONTENTS OF THE DRAWING MUST BE TREATED AS STRICTLY CONFIDENTIAL AND MUST NOT BE DISCLOSED TO ANY THIRD PARTY WITHOUT THE CLIENTS WRITTEN CONSENT. USE ONLY FOR THE PURPOSE FOR WHICH IT WAS LOANED. NO COPYING OR REPRODUCING. RETURN ON REQUEST.				DRAWN GC	APPROVED MA	
	LS TRANSMISSION CONSULTANCY LIMITED MAKES NO WARRANTIES, EXPRESS OR IMPLIED, THAT COMPLIANCE WITH THIS DRAWING, OR ANY OTHER DOCUMENT ISSUED BY LSTC, WOULD IN ITSELF BE SUFFICIENT TO ENSURE SAFE SYSTEMS OF WORK OR OPERATION. USERS ARE REMINDED OF THEIR OWN DUTIES UNDER HEALTH AND SAFETY LEGISLATION.				ORIGINAL SIZE A2	DRAWING NUMBER 18_220566_26	REV A