


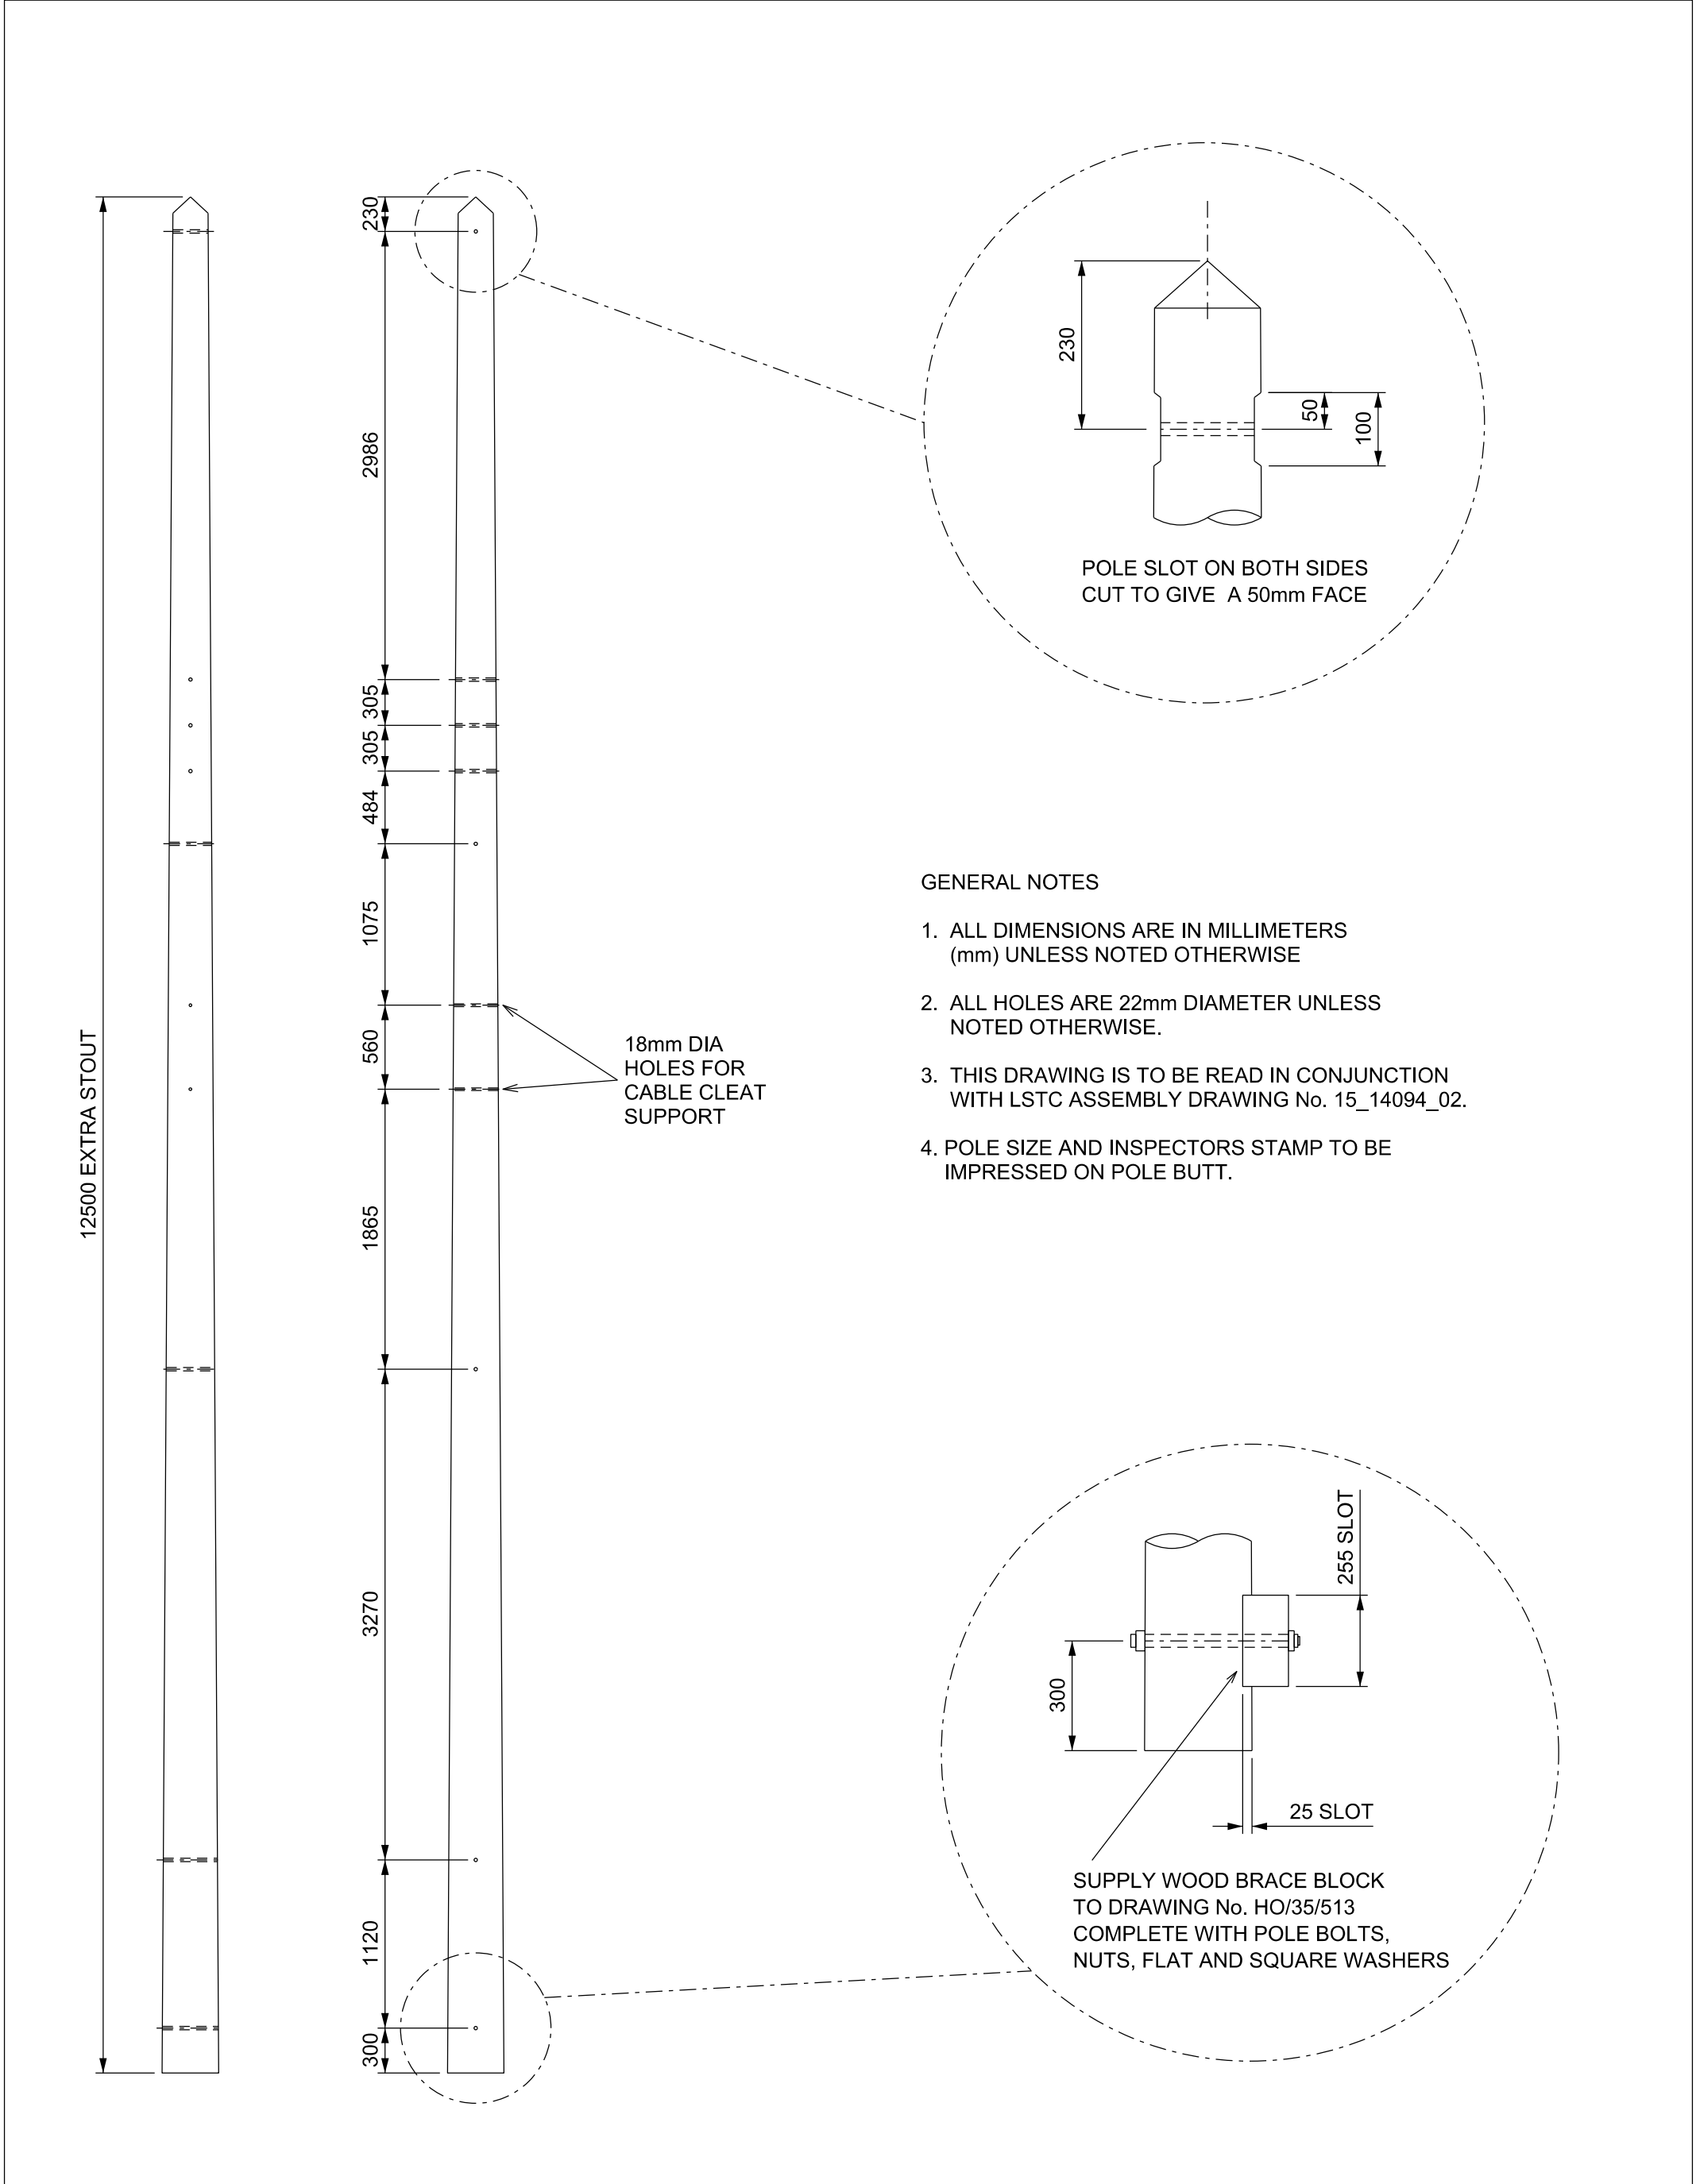

WARNING: DRAWING MAY BE REDUCED. DO NOT SCALE.

REV	Date	Drwn	Chkd	Appd	REV	Date	Drwn	Chkd	Appd	REV	Date	Drwn	Chkd	Appd	DATE	09_04_2014	Title			
A	FIRST ISSUE														SCALE	1:40 @ A3	POLE DRILLING, SCARFING AND MARKING FOR SPECIAL 33kV CABLE TERMINATION H-POLE			
REV	Date	Drwn	Chkd	Appd	REV	Date	Drwn	Chkd	Appd	REV	Date	Drwn	Chkd	Appd	DRAWN	SP	Location	LSTC Drawing Number	ShtNo	RevNo
															CHECKED	MA	WEDGEHILL	18_14094_03	1	A
															APPROVED					

Project Number		Drawing Status FOR APPROVAL	
Title		POLE DRILLING, SCARFING AND MARKING FOR SPECIAL 33kV CABLE TERMINATION H-POLE	
Location	LSTC Drawing Number	ShtNo	RevNo
WEDGEHILL	18_14094_03	1	A