

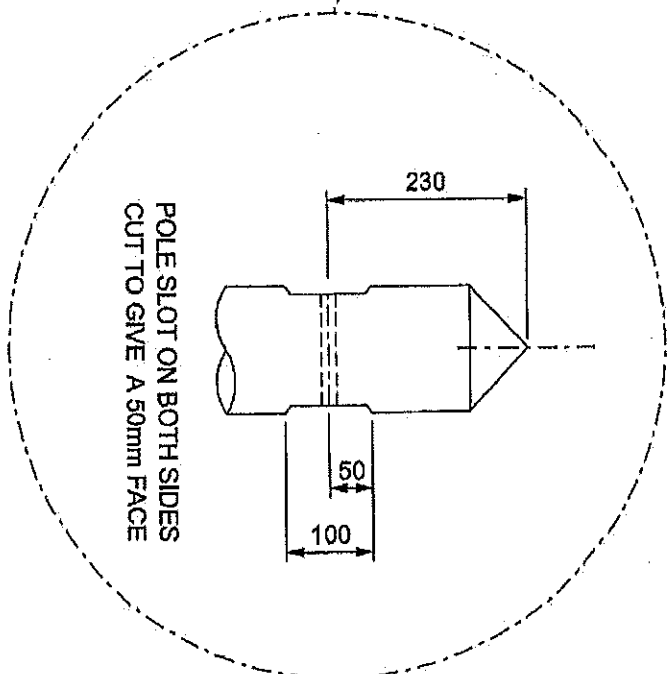


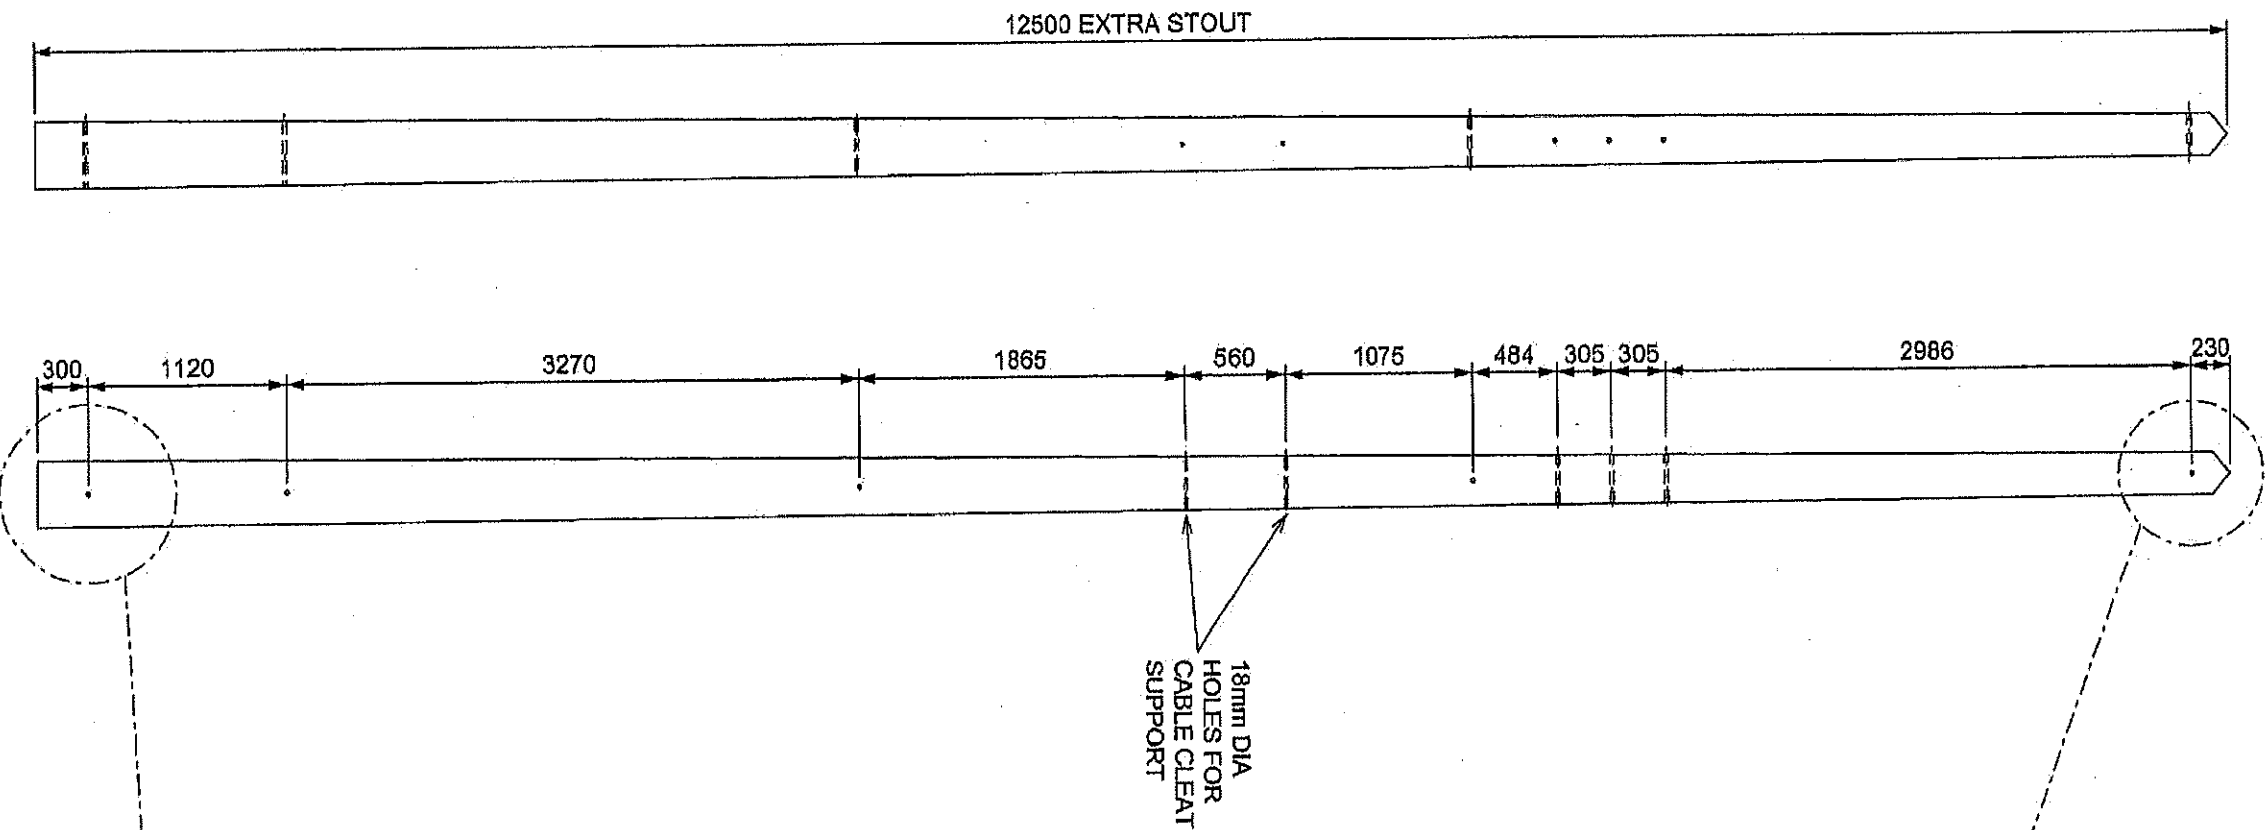

GENERAL NOTES

1. ALL DIMENSIONS ARE IN MILLIMETERS (mm) UNLESS NOTED OTHERWISE
2. ALL HOLES ARE 22mm DIAMETER UNLESS NOTED OTHERWISE.
3. THIS DRAWING IS TO BE READ IN CONJUNCTION WITH LSTC ASSEMBLY DRAWING NO. 15_14109_03.
4. POLE SIZE AND INSPECTORS STAMP TO BE IMPRESSED ON POLE BUTT.

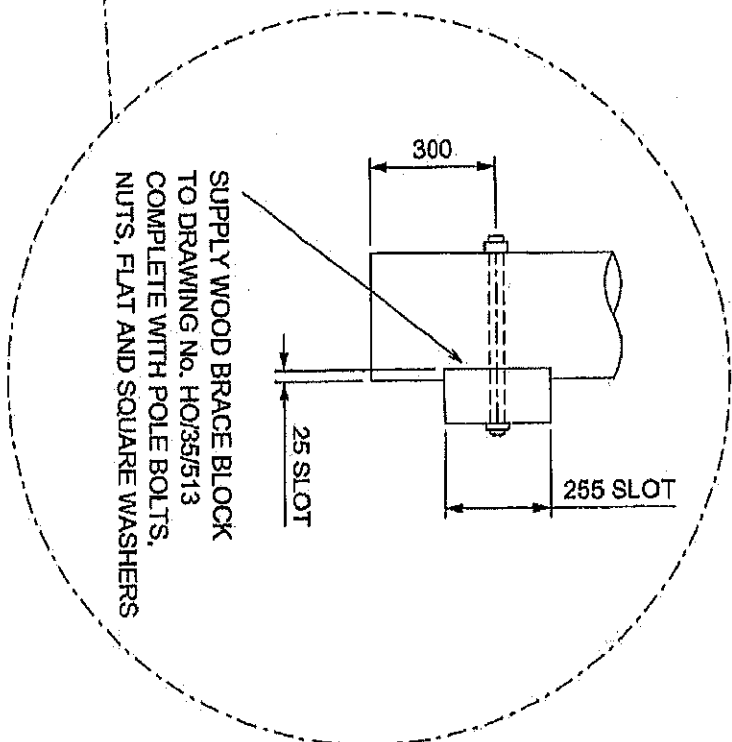

WARNING: DRAWING MAY BE REDUCED. DO NOT SCALE.

POLE DRILLING, SCARFING FOR SPECIAL 33kV CABLE TERMINATION H-POLE	
REV		Date		Drawn		SP		MA		Appd		REV		Date		Drawn		SP		MA		Appd		DATE		SCALE		DRAWN		CHECKED		APPROVED		Title													
A		12.05.14																								12.05.2014		1:40 @ A3		SP		MAS		Location VERWOOD		ISTC Drawing Number 18.14109.04		ShNo 1		RevNo A							
REV		Date		Drawn		SP		MA		Appd		REV		Date		Drawn		SP		MA		Appd		REV		Date		Drawn		SP		MA		Appd		DATE		SCALE		DRAWN		CHECKED		APPROVED		Title	
REV		Date		Drawn		SP		MA		Appd		REV		Date		Drawn		SP		MA		Appd		REV		Date		Drawn		SP		MA		Appd		DATE		SCALE		DRAWN		CHECKED		APPROVED		Title	



Project Number Drawing Status
FOR APPROVAL

Title
POLE DRILLING, SCARFING
FOR SPECIAL 33kV CABLE TERMINATION H-POLE