

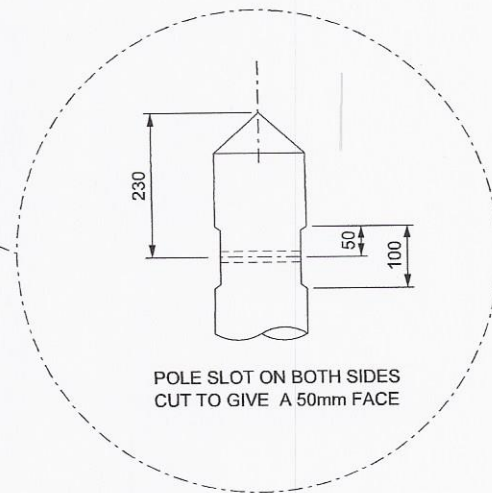
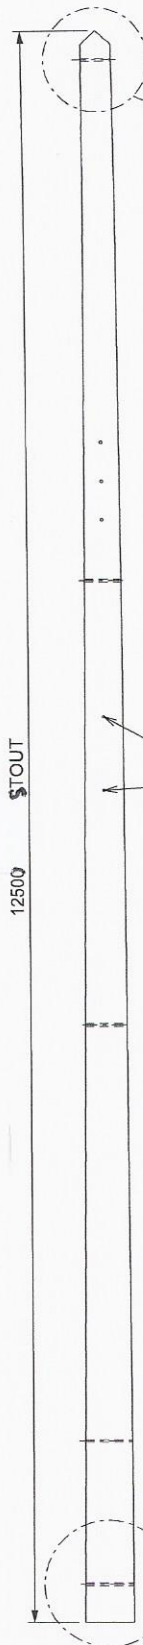


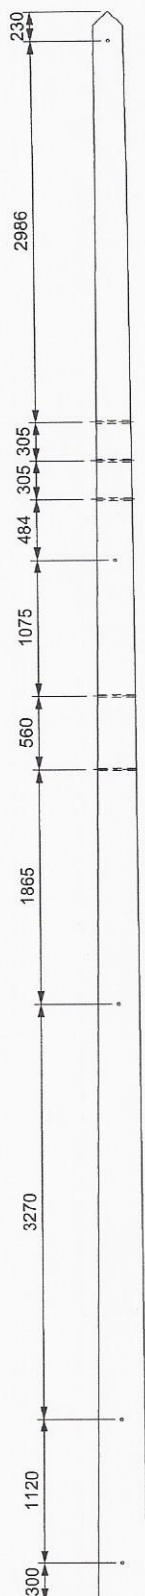

#### GENERAL NOTES

1. ALL DIMENSIONS ARE IN MILLIMETERS (mm) UNLESS NOTED OTHERWISE
2. ALL HOLES ARE 22mm DIAMETER UNLESS NOTED OTHERWISE.
3. THIS DRAWING IS TO BE READ IN CONJUNCTION WITH LSTC ASSEMBLY DRAWING No. 15\_14472\_03.
4. POLE SIZE AND INSPECTORS STAMP TO BE IMPRESSED ON POLE BUTT.

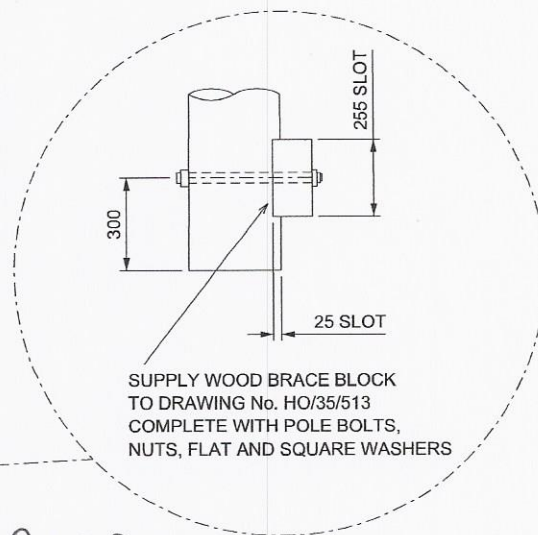

*DRAWING REVISED  
By S. COULDS 19/11/15  
12.5m STOUT REQUIRED.*

WARNING: DRAWING MAY BE REDUCED. DO NOT SCALE.

| REV         | Date     | Drawn | Chkd | Appd | SP  | REV  | Date  | Drawn | Chkd | Appd | REV  | Date  | Drawn | Chkd | Appd | DATE            |
|-------------|----------|-------|------|------|-----|------|-------|-------|------|------|------|-------|-------|------|------|-----------------|
| A           | 17/10/14 | MA    | RF   |      |     |      |       |       |      |      |      |       |       |      |      | 17/10/2014      |
| FIRST ISSUE |          |       |      |      |     |      |       |       |      |      |      |       |       |      |      | SCALE 1:40 @ A3 |
| REV         | Date     | Drawn | Chkd | Appd | REV | Date | Drawn | Chkd  | Appd | REV  | Date | Drawn | Chkd  | Appd |      | DRAWN MA        |
|             |          |       |      |      |     |      |       |       |      |      |      |       |       |      |      | CHECKED RF      |
|             |          |       |      |      |     |      |       |       |      |      |      |       |       |      |      | APPROVED SP     |

|                                 |  |                                                                               |         |
|---------------------------------|--|-------------------------------------------------------------------------------|---------|
|                                 |  | Drawing Status FOR APPROVAL                                                   |         |
| Project Number                  |  | Title                                                                         |         |
|                                 |  | POLE DRILLING, SCARFING AND MARKING FOR SPECIAL 33kV CABLE TERMINATION H-POLE |         |
| LSTC Drawing Number 18.14472.04 |  | ShtNo 1                                                                       | RevNo A |