


POLE SCARFED ON BOTH SIDES TO GIVE
A MINIMUM 50mm WIDE FLAT FACE

PARALLEL WITHIN LIMITS OF
TYPE 2, 200 - 280mm
SECTION & LONG SPAN INTERMEDIATE

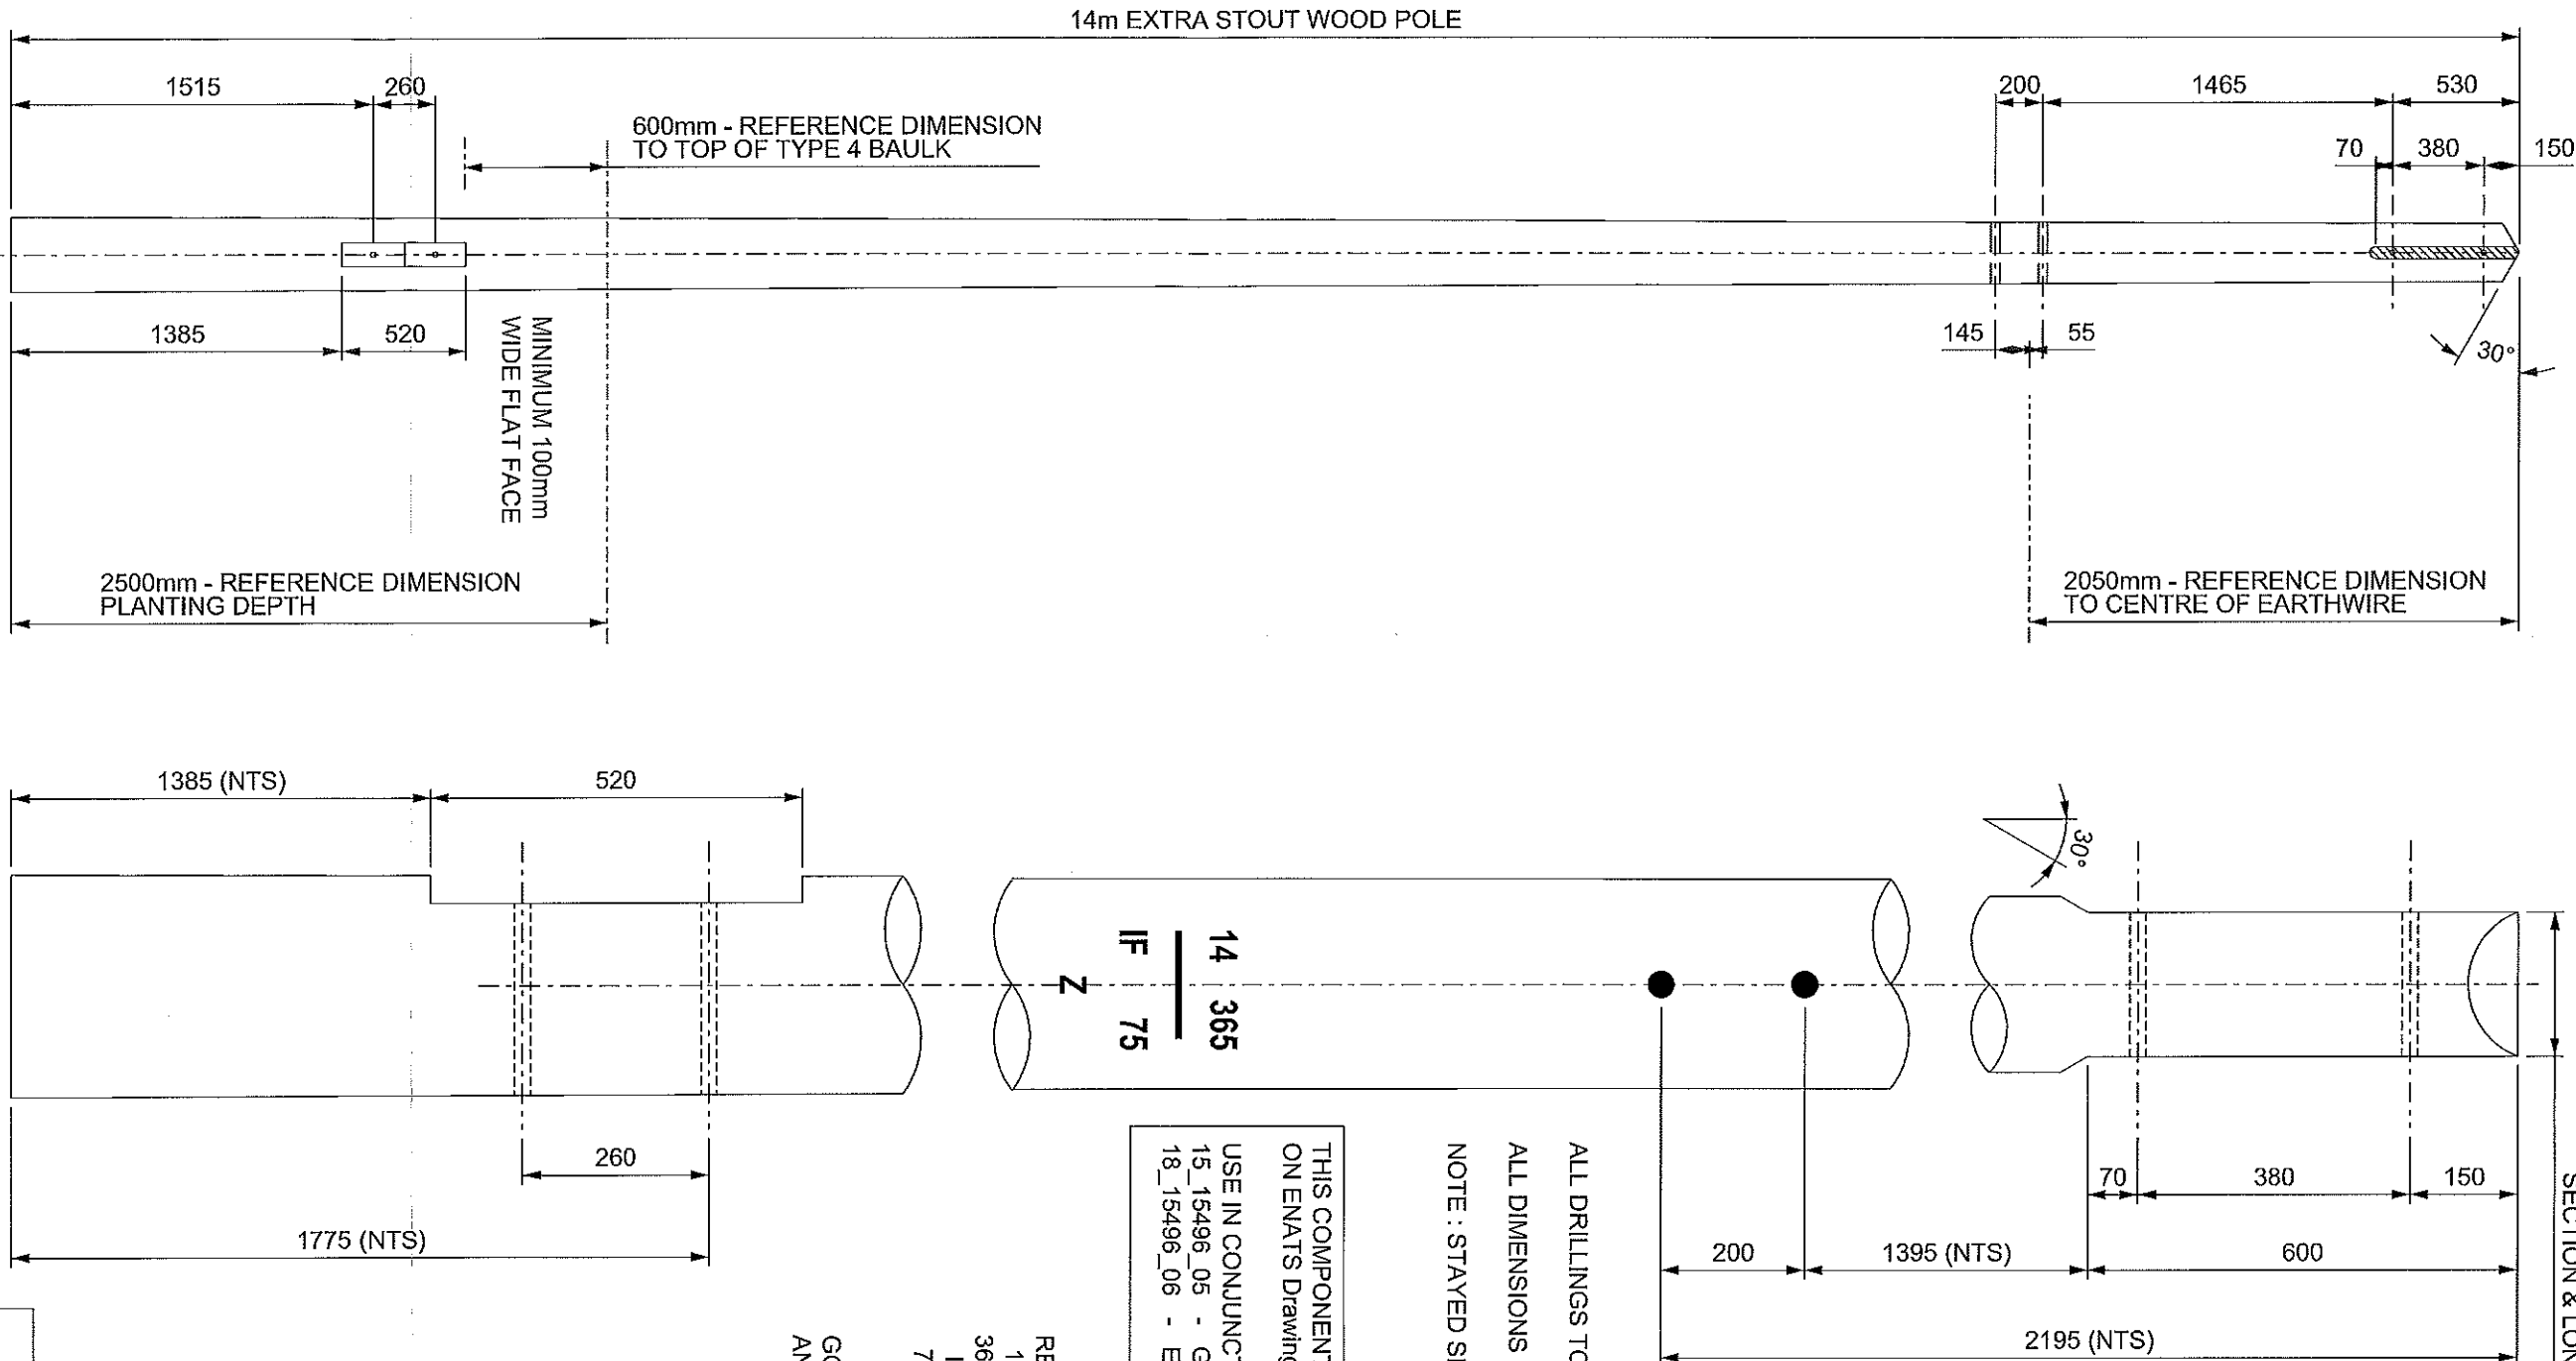

ALL DRILLINGS TO BE 22mm DIAMETER
ALL DIMENSIONS IN MILLIMETRES (U.N.O)
NOTE : STAYED SECTION POLE PLANTING DEPTH 2.5m

THIS COMPONENT TO REPLACE ITEM 9
ON ENATS Drawing 435009

USE IN CONJUNCTION WITH LSTC DRAWINGS
15_15496_05 - GENERAL ARRANGEMENT / ERECTION DETAILS
18_15496_06 - EARTHIRE ATTACHMENT BRACKET STEELWORK

REFERENCE
14 - POLE LENGTH (m)
365 - POLE DIAMETER 1.5m FROM BUTT
IF - IMPORTED FIR
75 - YEAR OF CREOSOTING
Z - SUPPLIERS NAME OR MARK
GOUGE MARK 6mm WIDE x 6mm DEEP
AND 3m FROM POLE BUTT

WARNING: DRAWING MAY BE REDUCED. DO NOT SCALE.

POLE SIZE TO BE IMPRESSED ON BUTT

REV	Date	Drwn	Chkd	Appd	REV	Date	Drwn	Chkd	Appd	REV	Date	Drwn	Chkd	Appd

		Project Number		Drawing Status	
15-496		FOR APPROVAL		Title	
14m EXTRA STOUT WOOD POLE		Location		SSE Drawing Number	
SCARFING AND DRILLING DETAILS		EAST CLAYDON		18_15496_07	
				ShIno	
				RevNo	
				A	