
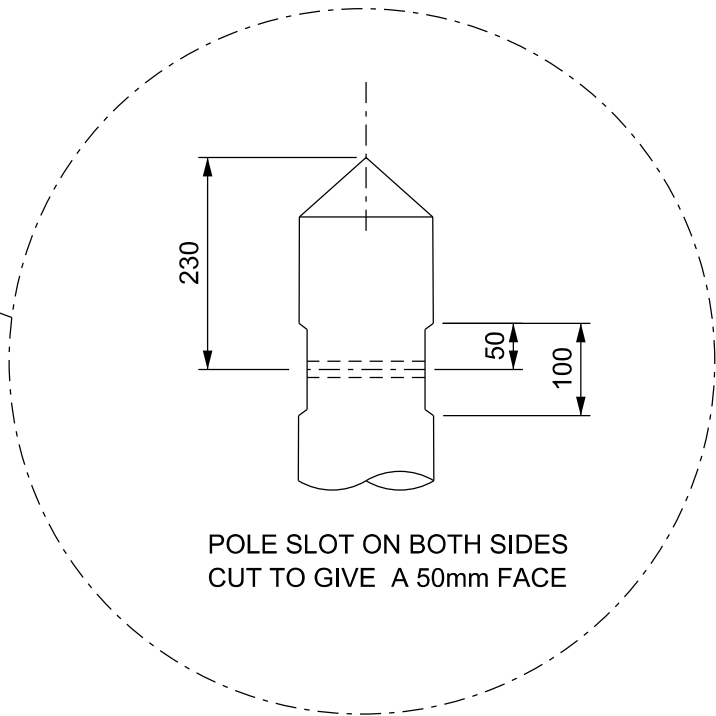



12500 EXTRA STOUT

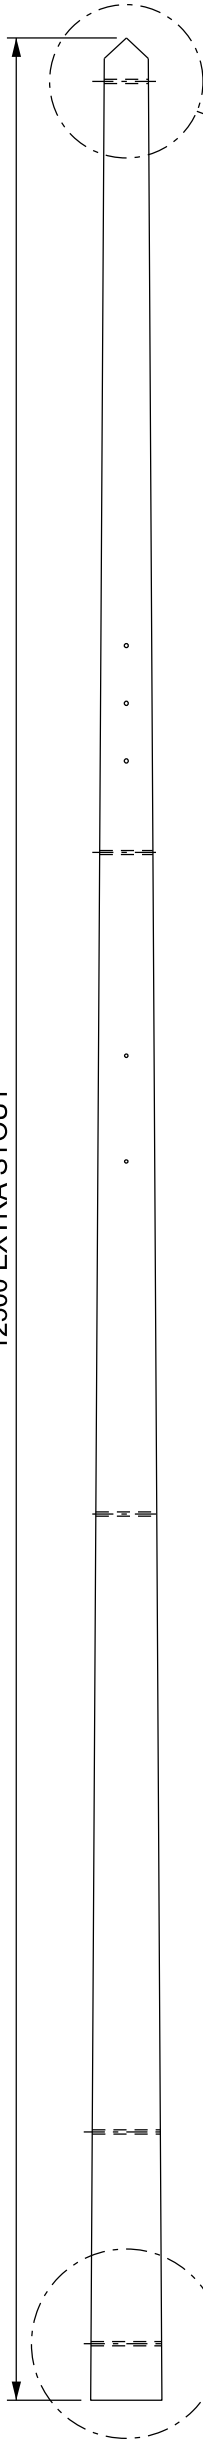

POLE SLOT ON BOTH SIDES
CUT TO GIVE A 50mm FACE

GENERAL NOTES

1. ALL DIMENSIONS ARE IN MILLIMETRES (mm) UNLESS NOTED OTHERWISE
2. ALL HOLES ARE 22mm DIAMETER UNLESS NOTED OTHERWISE.
3. THIS DRAWING IS TO BE READ IN CONJUNCTION WITH LSTC ASSEMBLY DRAWING No. 15_14383_03.
4. POLE SIZE AND INSPECTORS STAMP TO BE IMPRESSED ON POLE BUTT.

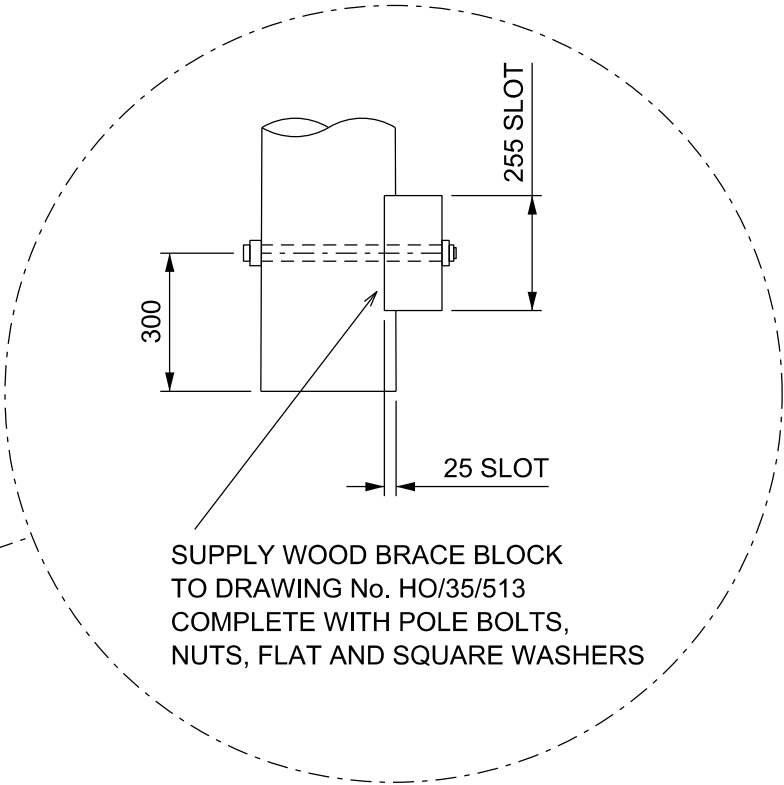

SUPPLY WOOD BRACE BLOCK
TO DRAWING No. HO/35/513
COMPLETE WITH POLE BOLTS,
NUTS, FLAT AND SQUARE WASHERS

WARNING: DRAWING MAY BE REDUCED. DO NOT SCALE.

REV	Date	Drwn	Chkd	Appd	REV	Date	Drwn	Chkd	Appd	REV	Date	Drwn	Chkd	Appd	DATE	24/09/2014	Title POLE DRILLING, SCARFING AND MARKING FOR SPECIAL 33kV CABLE TERMINATION H-POLE			
A	24/09/14	DEC	RF	SP	B	26/06/15	JDH	SP	SP						SCALE	1:40 @ A3				
															DRAWN	DEC				
															CHECKED	RF				
REV	Date	Drwn	Chkd	Appd	REV	Date	Drwn	Chkd	Appd	REV	Date	Drwn	Chkd	Appd	APPROVED	SP	Location	LSTC Drawing Number	ShtNo	RevNo
																	BERRY COURT	18_14383_04	1	B



Project Number Drawing Status
FOR APPROVAL