




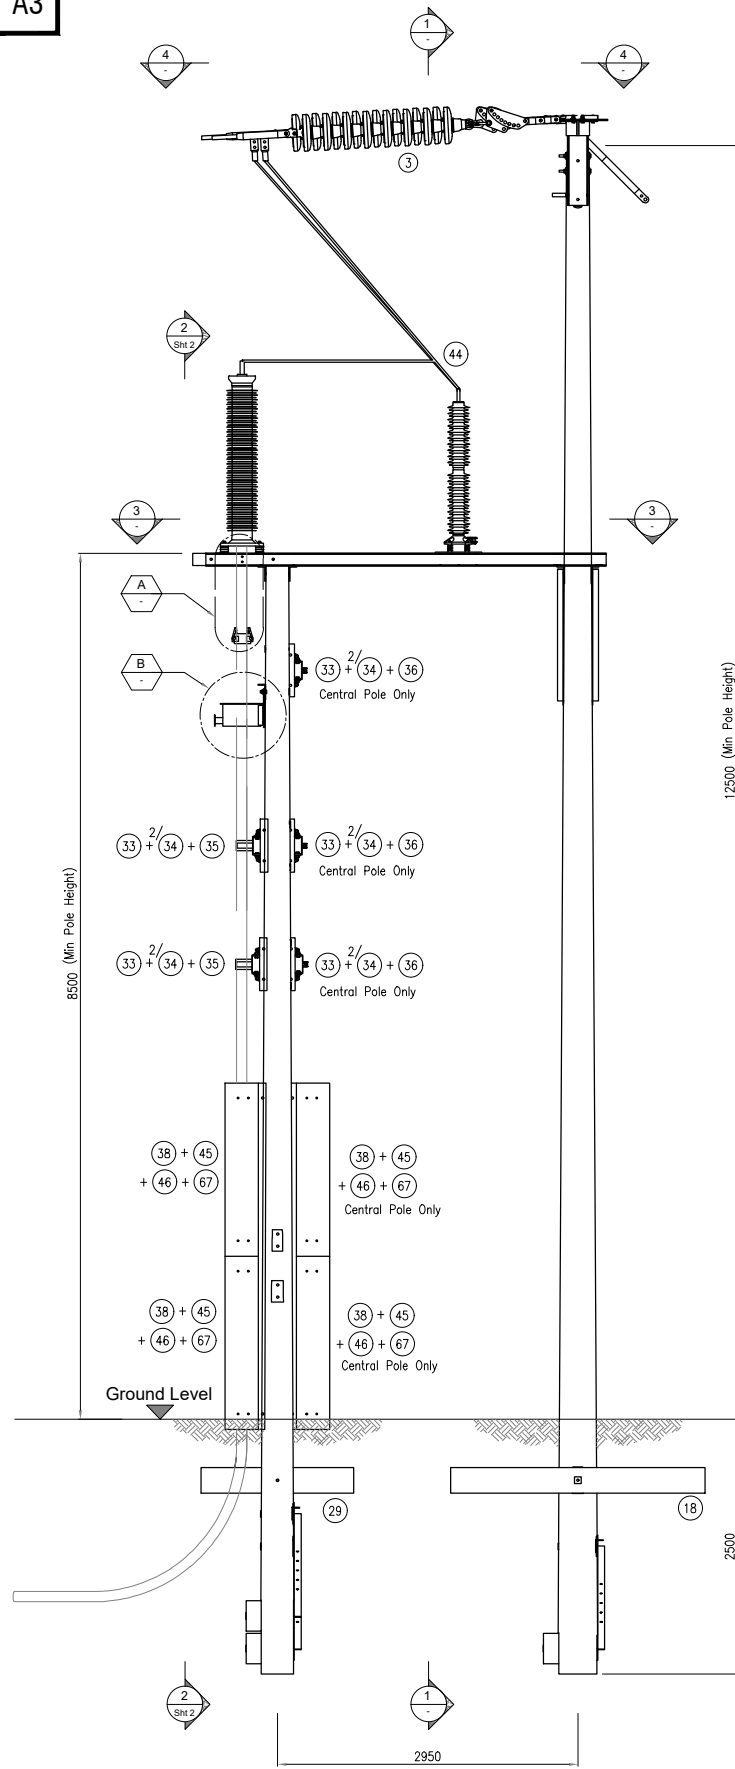


SIDE ELEVATION

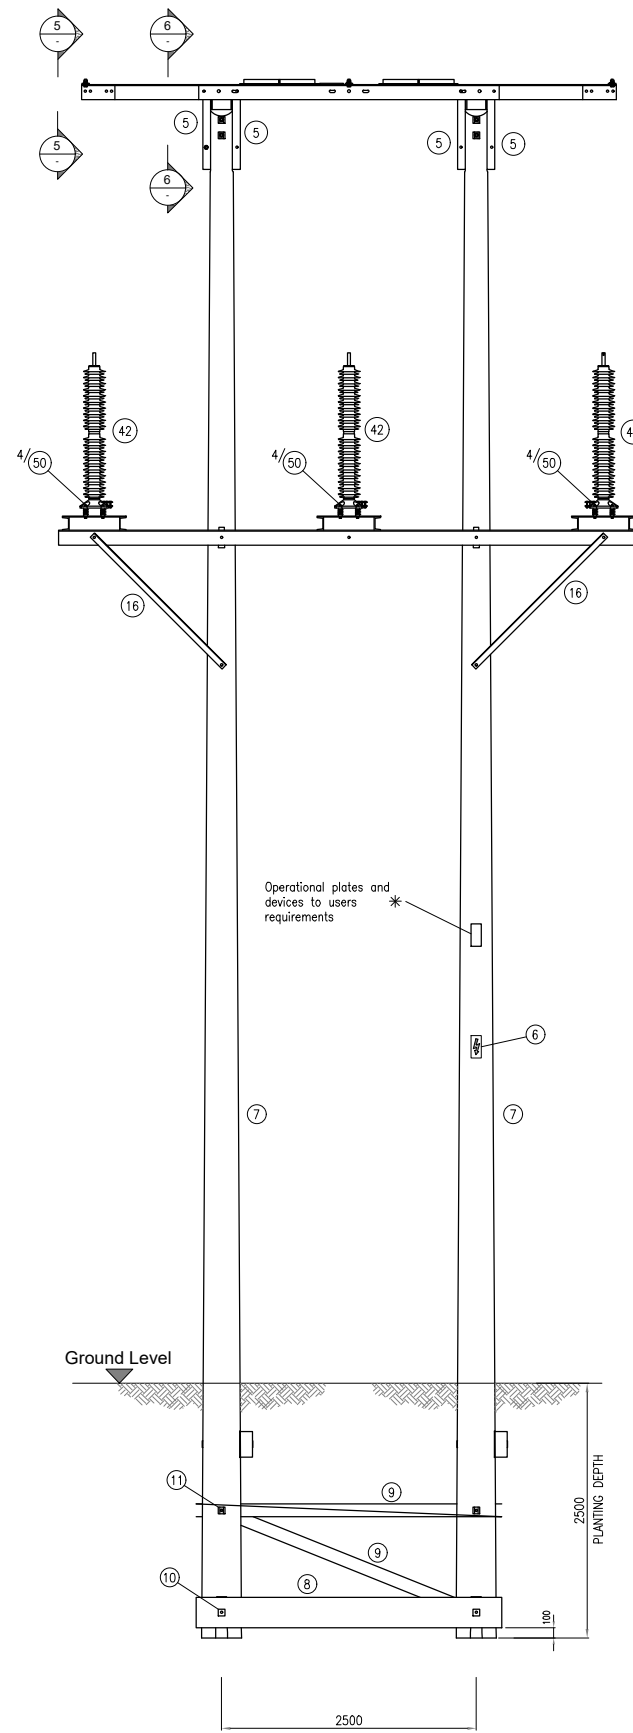


SECTION 1
Scale 1:35

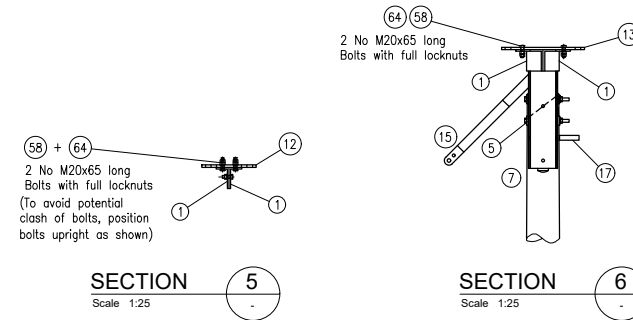

SECTION 5
Scale 1:25

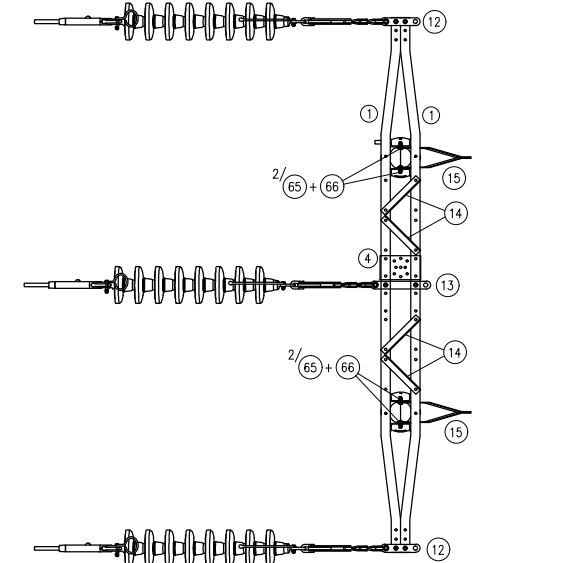

SECTION 4
Scale 1:35

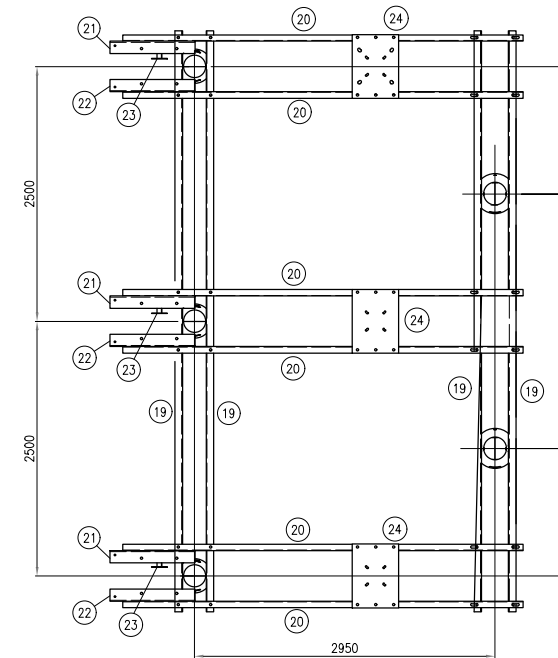


SECTION 3

LIST OF ALL RELEVANT DRAWINGS OR DOCUMENTS THAT DIRECTLY
RELATE TO THE CURRENT REVISION OF THE DRAWING

DOCUMENT REFERENCE:

NOTES:-

1. ALL DIMENSIONS GIVEN IN MILLIMETRES (mm) U.N.O.
2. THIS DRAWING TO BE READ IN CONJUNCTION WITH DRAWINGS
200_1109_0035 SHT02,0037,0038 & 0039
3. THIS DRAWING IS BASED ON THE FOLLOWING:
POLE MOUNTED TERMINAL ASSEMBLY ENATS 4350. DWG REF: 435011
& 435012.
4. ALL BOLTED CONNECTIONS ABOVE GROUND LEVEL SHALL BE FITTED
WITH A LOCK NUT.
5. ALL UNUSED POLE DRILLINGS SHALL BE SEALED WITH A HARDWOOD
PLUG (ENA TS 43-88 ANNEX C)

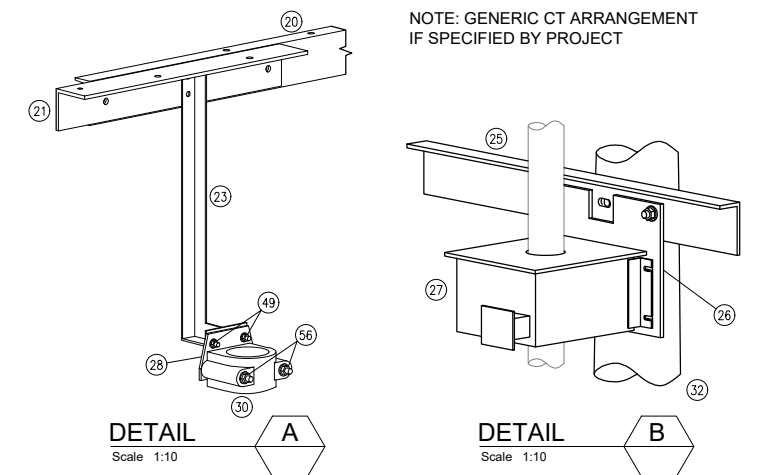

DETAIL

Scale 1:10

A

DETAIL
Scale 1:10

Rev:	Drawn: PF	Approved: SA	Description: ISSUED FOR INFORMATION
01	Checked: DB	Date: 18-09-20	



SSE Inverlmond House, 200 Dunkeld Road
Perth, PH1 3AQ, UK www.sse.com

Project:
SSEN APPROACH 1 DESIGN

Project Number:	VARIOUS	Location:	VARIOUS
------------------------	---------	------------------	---------

Title:
TERMINAL POLE ASSEMBLY : STRUCTURAL ARRANGEMENT
132kV WOOD POLE OHL

Drawing Status:	For Information	Drawn:	PF
------------------------	-----------------	---------------	----

Scale: NTS	Checked: DB
-------------------	--------------------

Date: 12.01.20	Approved: SA
-----------------------	---------------------

Drawing Number: 200 1109 0035	Sheet No: 01	Revision No: 01
---	------------------------	---------------------------