


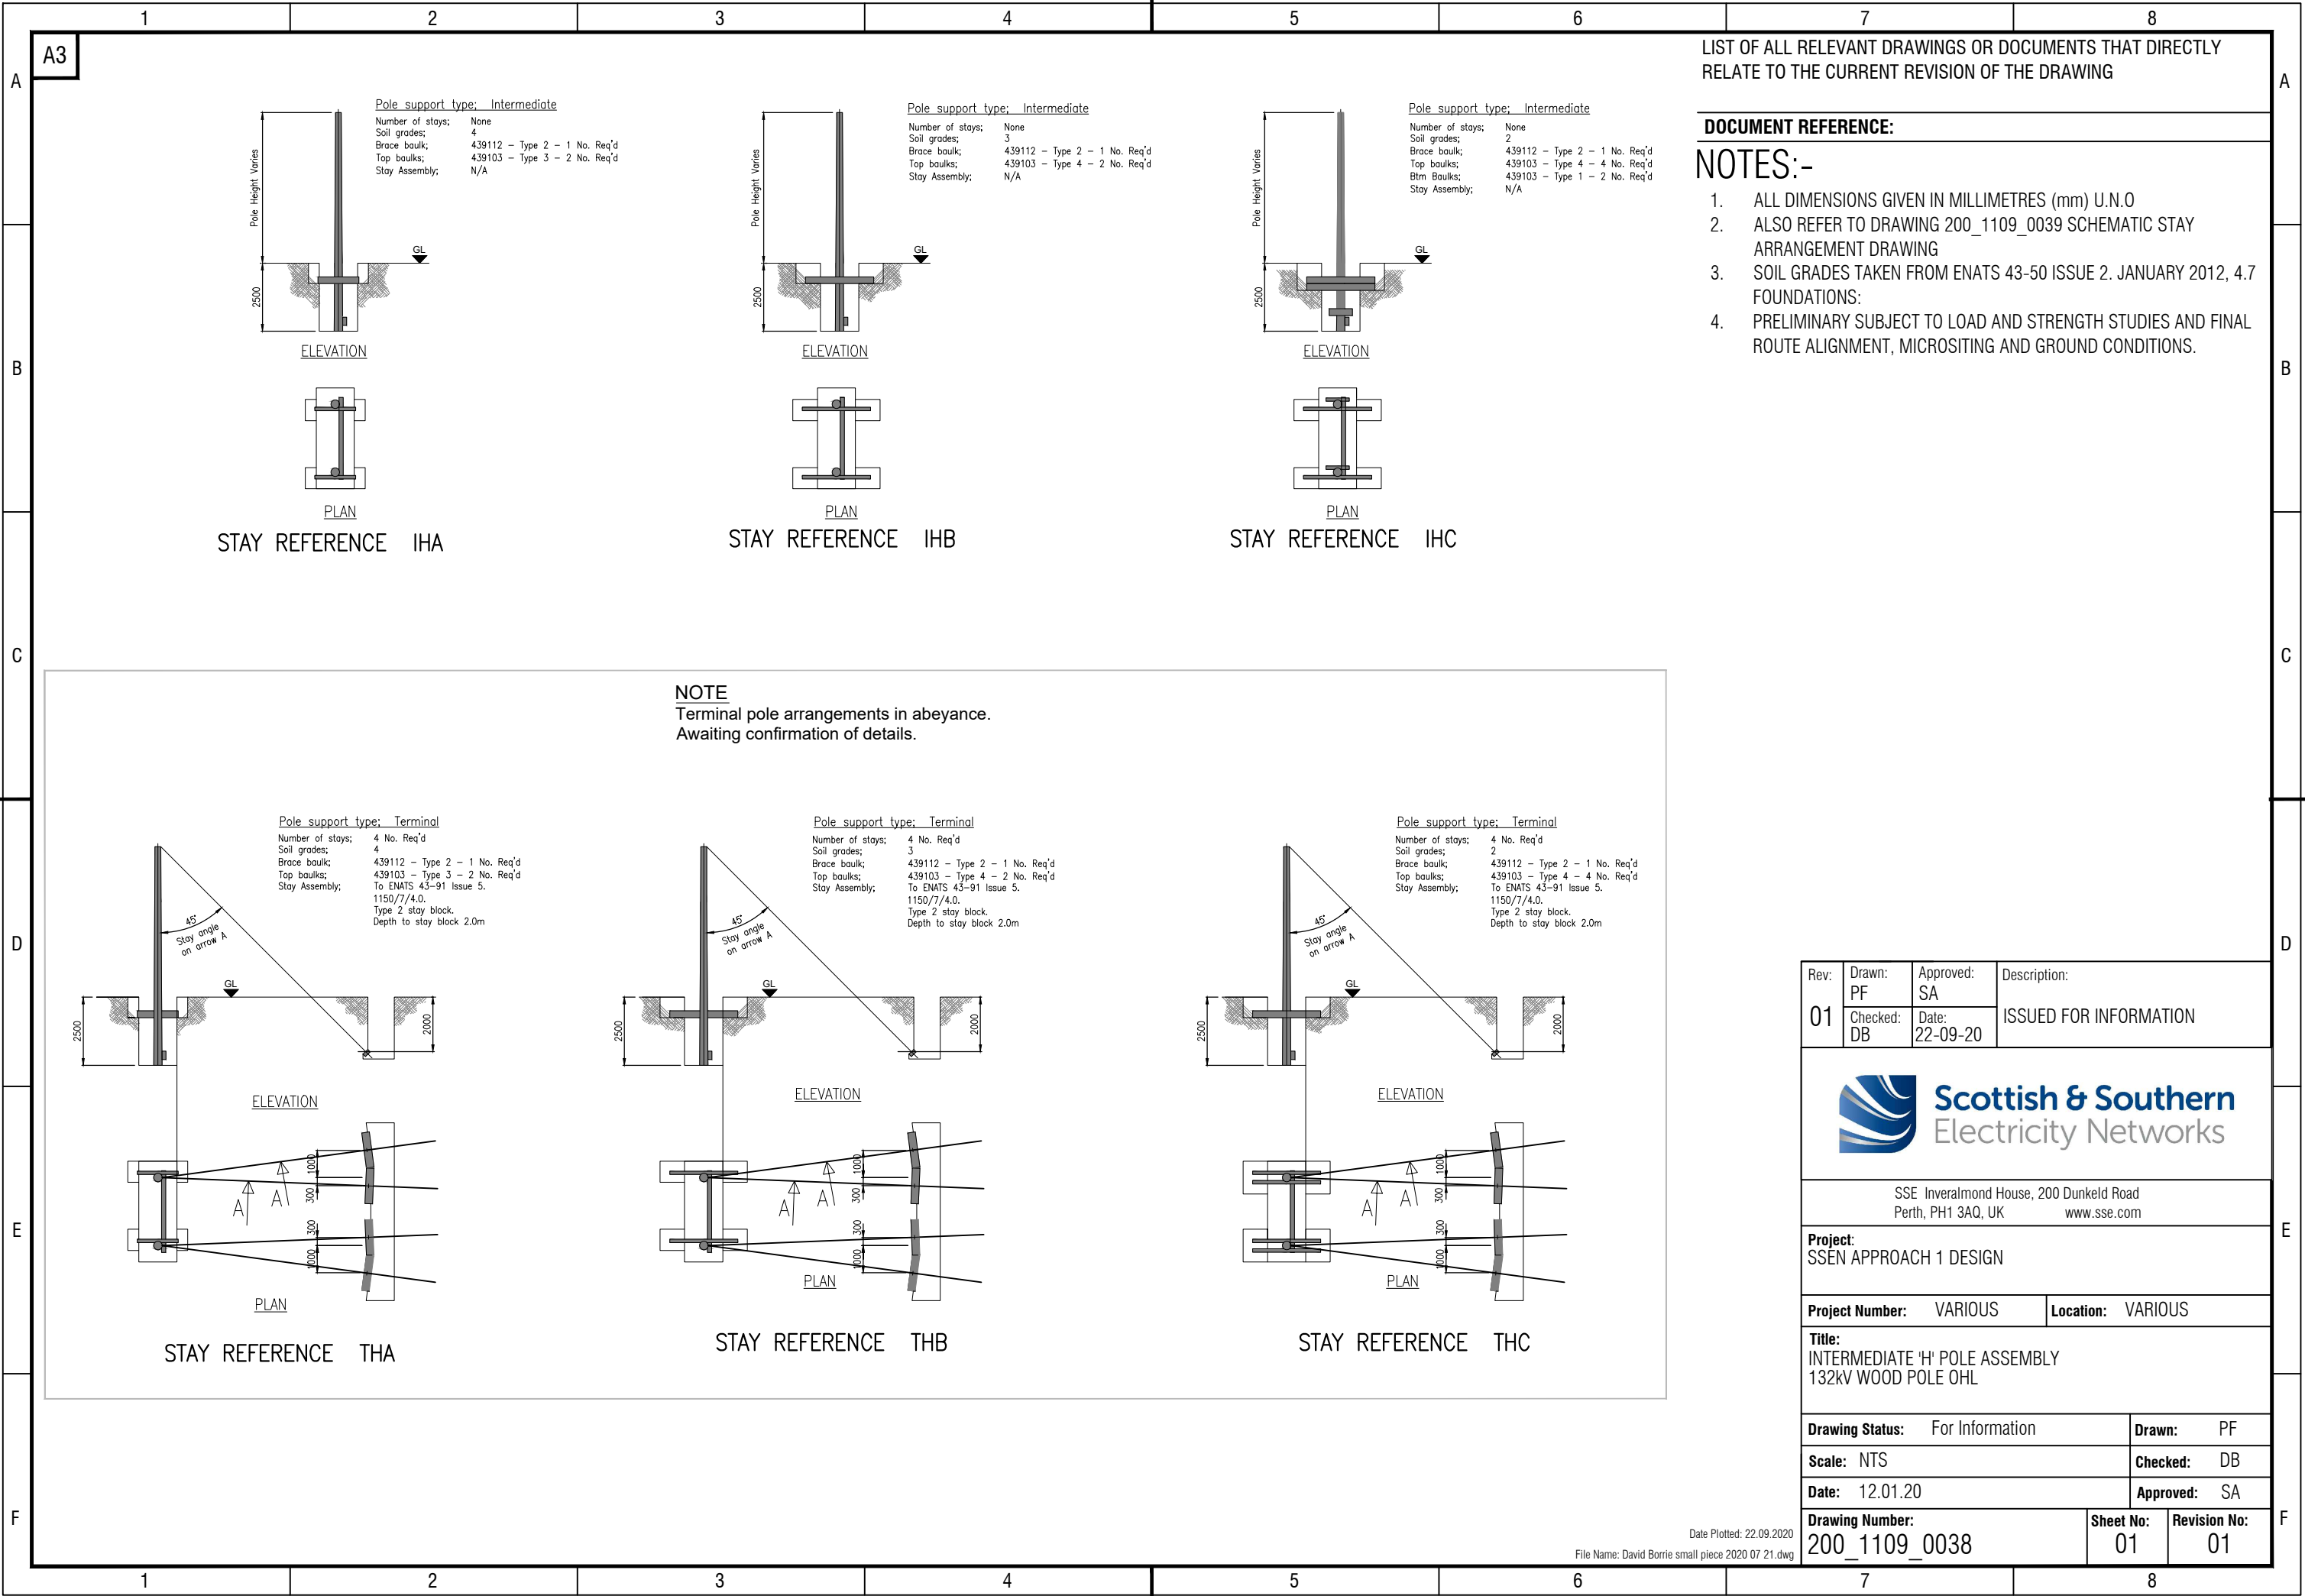

LIST OF ALL RELEVANT DRAWINGS OR DOCUMENTS THAT DIRECTLY RELATE TO THE CURRENT REVISION OF THE DRAWING

DOCUMENT REFERENCE:

NOTES:-

- 1. ALL DIMENSIONS GIVEN IN MILLIMETRES (mm) U.N.O
- 2. ALSO REFER TO DRAWING 200_1109_0039 SCHEMATIC STAY ARRANGEMENT DRAWING
- 3. SOIL GRADES TAKEN FROM ENATS 43-50 ISSUE 2. JANUARY 2012, 4.7 FOUNDATIONS:
- 4. PRELIMINARY SUBJECT TO LOAD AND STRENGTH STUDIES AND FINAL ROUTE ALIGNMENT, MICROSITING AND GROUND CONDITIONS.

Rev: 01	Drawn: PF	Approved: SA	Description: ISSUED FOR INFORMATION
	Checked: DB	Date: 22-09-20	
 Scottish & Southern Electricity Networks			
SSE Inveralmond House, 200 Dunkeld Road Perth, PH1 3AQ, UK www.sse.com			
Project: SSEN APPROACH 1 DESIGN			
Project Number: VARIOUS		Location: VARIOUS	
Title: INTERMEDIATE 'H' POLE ASSEMBLY 132KV WOOD POLE OHL			
Drawing Status: For Information			Drawn: PF
Scale: NTS			Checked: DB
Date: 12.01.20			Approved: SA
Drawing Number: 200_1109_0038			Sheet No: 01
			Revision No: 01