


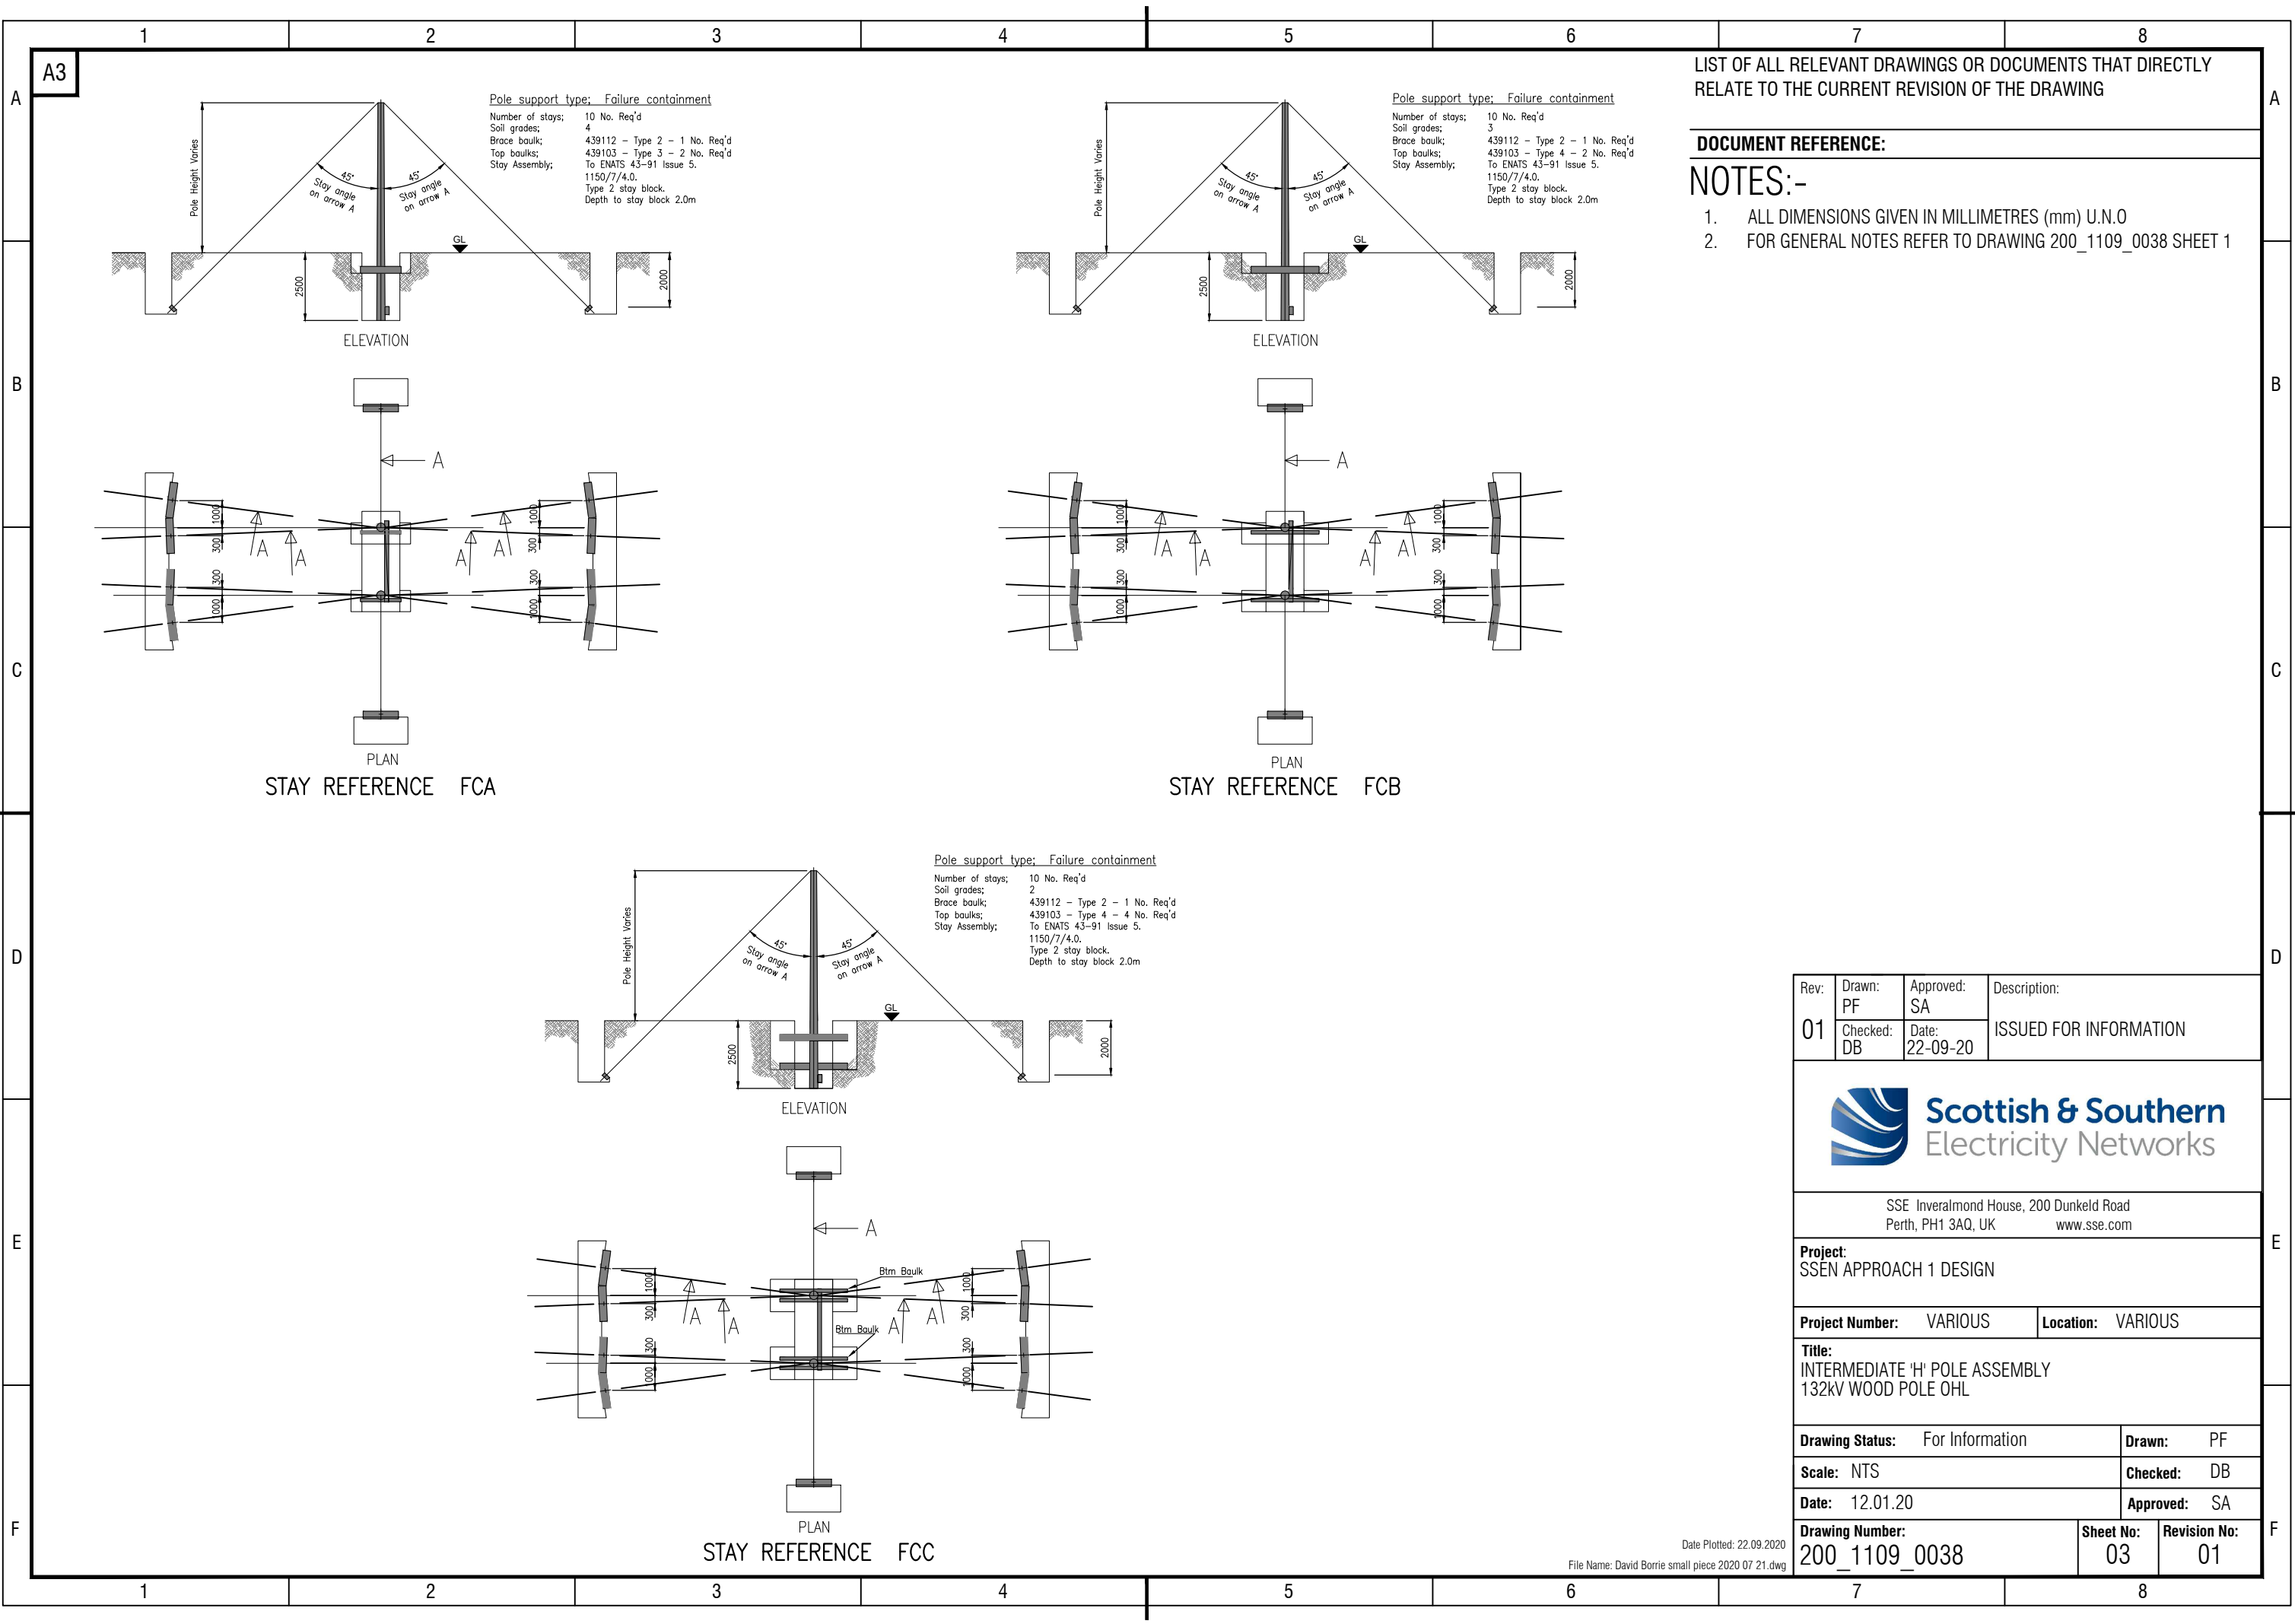

LIST OF ALL RELEVANT DRAWINGS OR DOCUMENTS THAT DIRECTLY RELATE TO THE CURRENT REVISION OF THE DRAWING

DOCUMENT REFERENCE:

NOTES:-

- 1. ALL DIMENSIONS GIVEN IN MILLIMETRES (mm) U.N.O
- 2. FOR GENERAL NOTES REFER TO DRAWING 200_1109_0038 SHEET 1

Rev:	Drawn:	Approved:	Description:
01	PF	SA	ISSUED FOR INFORMATION
	Checked:	Date:	
	DB	22-09-20	



Scottish & Southern
Electricity Networks

SSE Inverlmond House, 200 Dunkeld Road
Perth, PH1 3AQ, UKwww.sse.com

Project:
SSEN APPROACH 1 DESIGN

Project Number:	VARIOUS	Location:	VARIOUS
------------------------	---------	------------------	---------

Title:
INTERMEDIATE 'H' POLE ASSEMBLY
132kV WOOD POLE OHL

Drawing Status:	For Information	Drawn:	PF
Scale:	NTS	Checked:	DB
Date:	12.01.20	Approved:	SA

Drawing Number: 200_1109_0038	Sheet No: 03	Revision No: 01
---	------------------------	---------------------------