


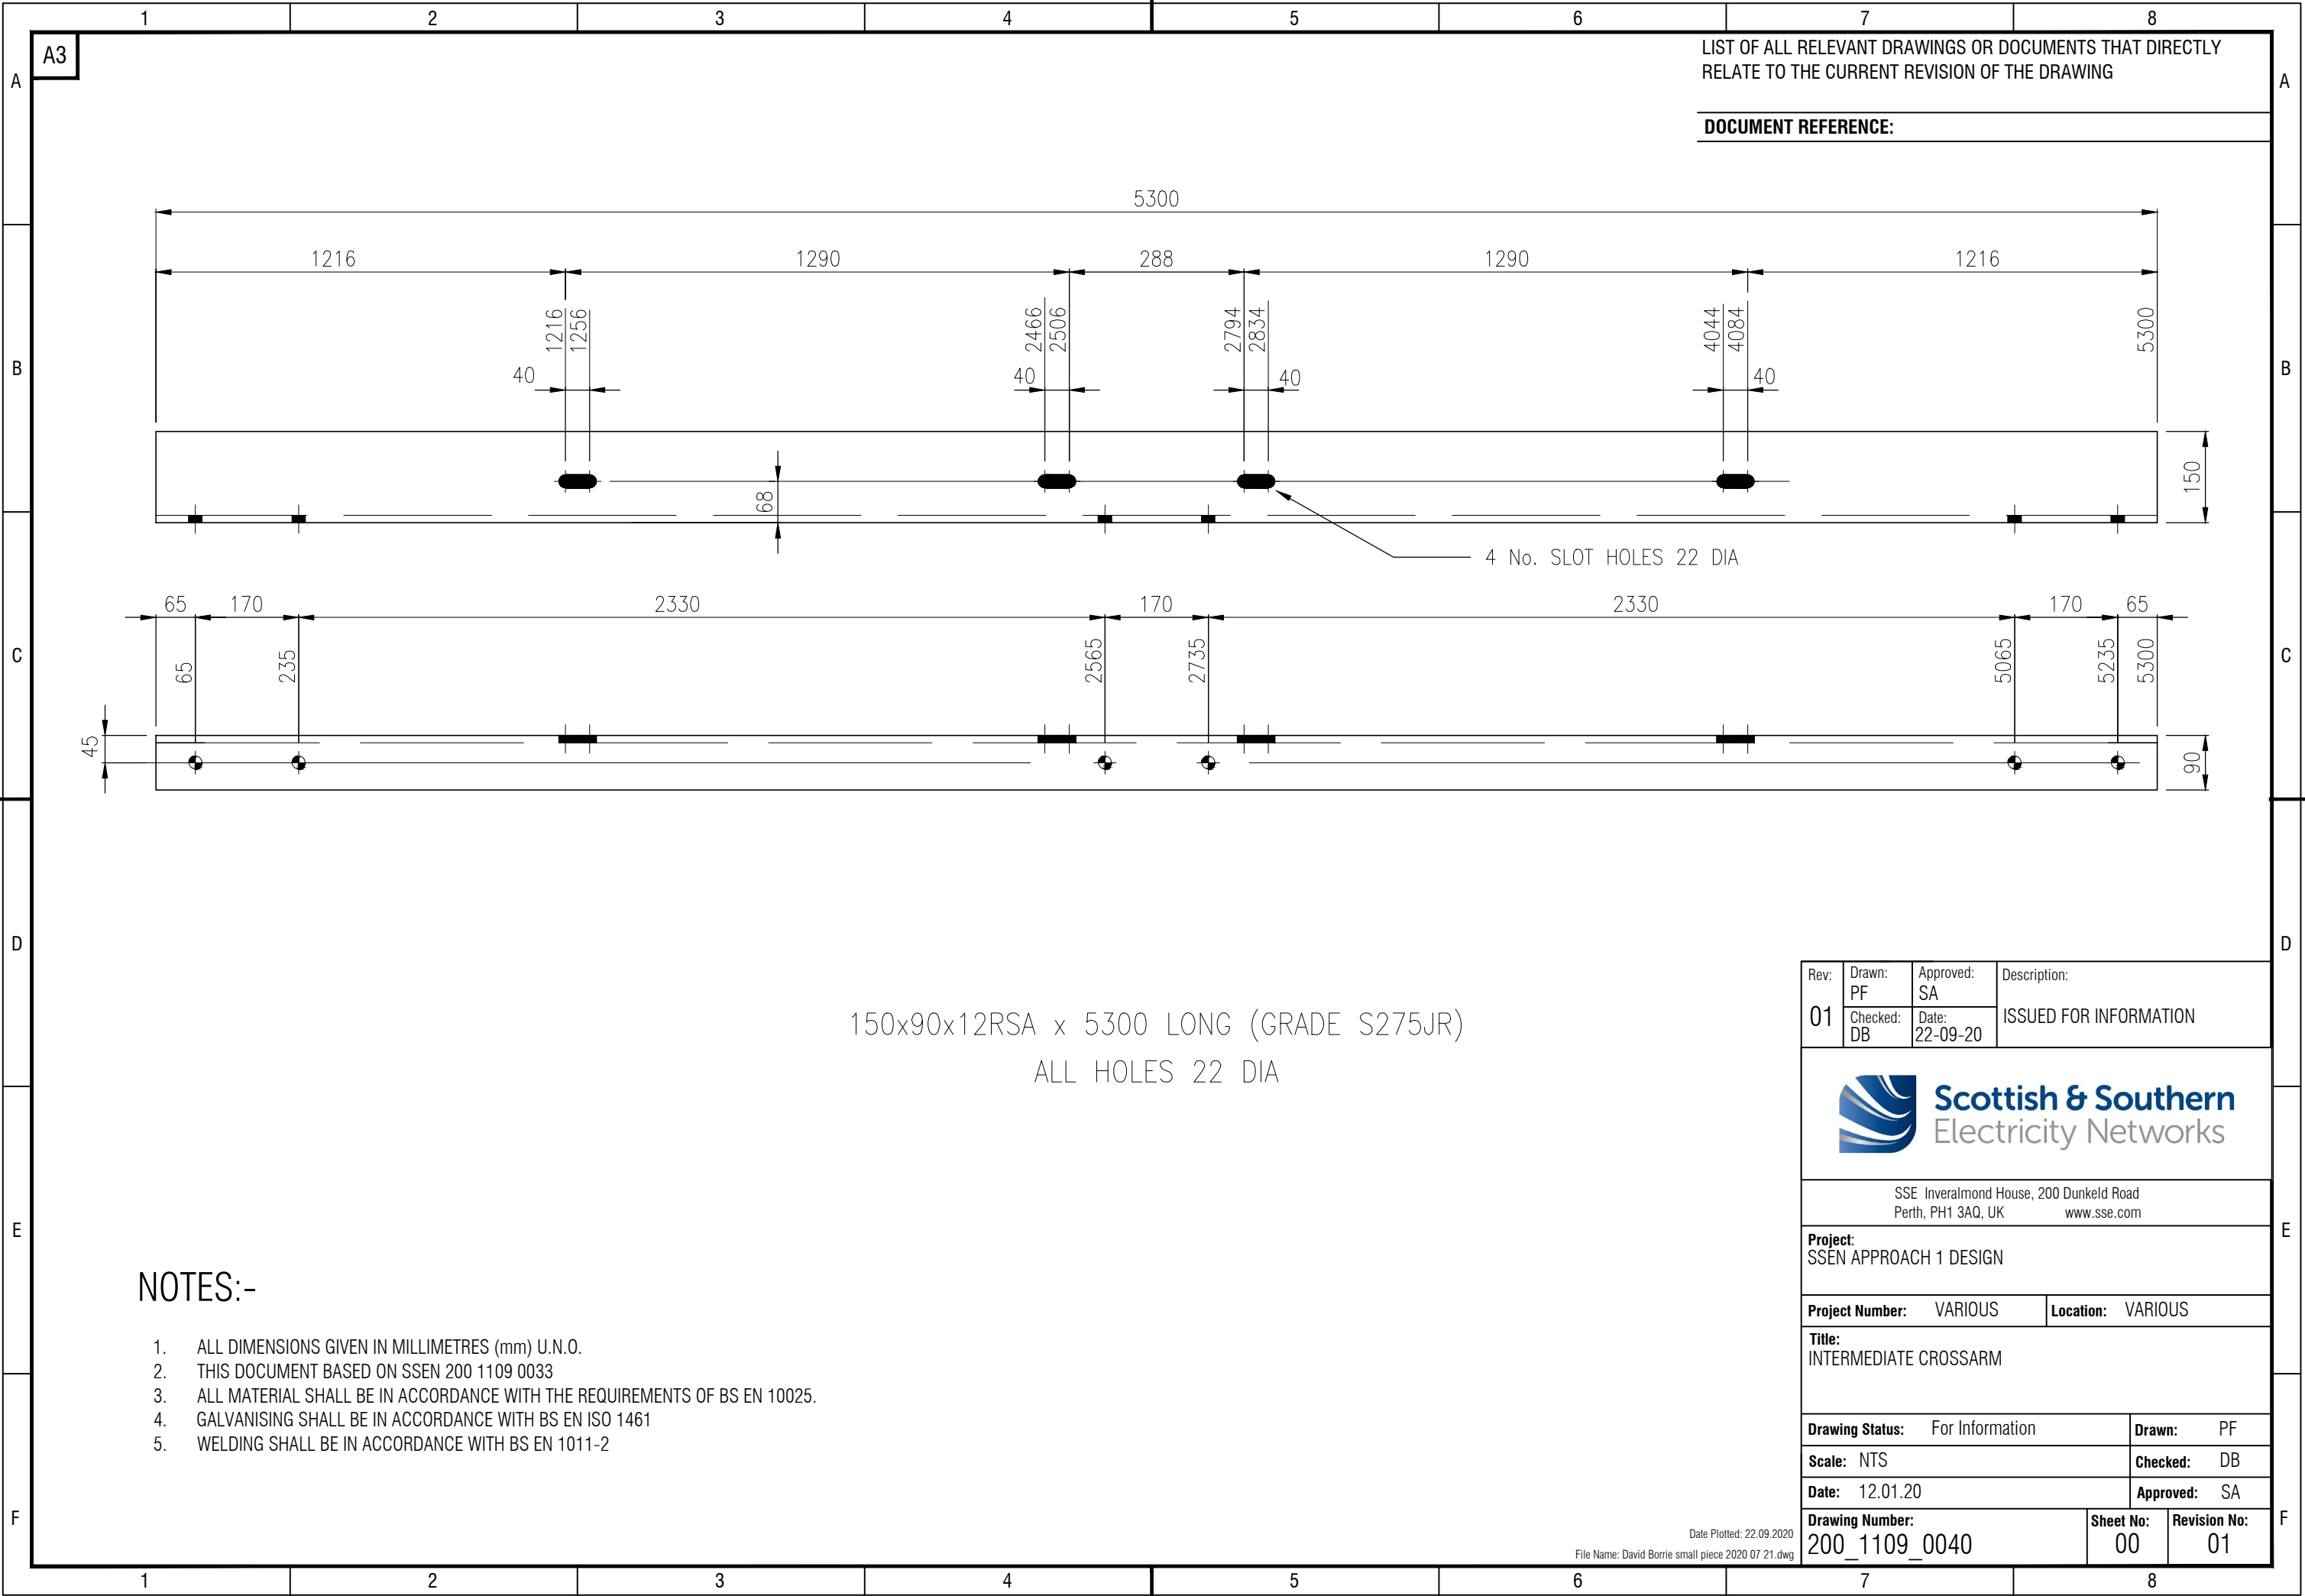

150x90x12RSA x 5300 LONG (GRADE S275JR)
ALL HOLES 22 DIA

LIST OF ALL RELEVANT DRAWINGS OR DOCUMENTS THAT DIRECTLY
RELATE TO THE CURRENT REVISION OF THE DRAWING

DOCUMENT REFERENCE:

NOTES:-

- 1. ALL DIMENSIONS GIVEN IN MILLIMETRES (mm) U.N.O.
- 2. THIS DOCUMENT BASED ON SSEN 200 1109 0033
- 3. ALL MATERIAL SHALL BE IN ACCORDANCE WITH THE REQUIREMENTS OF BS EN 10025.
- 4. GALVANISING SHALL BE IN ACCORDANCE WITH BS EN ISO 1461
- 5. WELDING SHALL BE IN ACCORDANCE WITH BS EN 1011-2

Rev:	Drawn: PF	Approved: SA	Description:
01	Checked: DB	Date: 22-09-20	ISSUED FOR INFORMATION

SSE Inveralmond House, 200 Dunkeld Road
Perth, PH1 3AQ, UK www.sse.com

Project:
SSEN APPROACH 1 DESIGN

Project Number: VARIOUS	Location: VARIOUS
--------------------------------	--------------------------

Title:
INTERMEDIATE CROSSARM

Drawing Status: For Information	Drawn: PF
Scale: NTS	Checked: DB
Date: 12.01.20	Approved: SA

Drawing Number: 200_1109_0040	Sheet No: 00	Revision No: 01
---	------------------------	---------------------------