



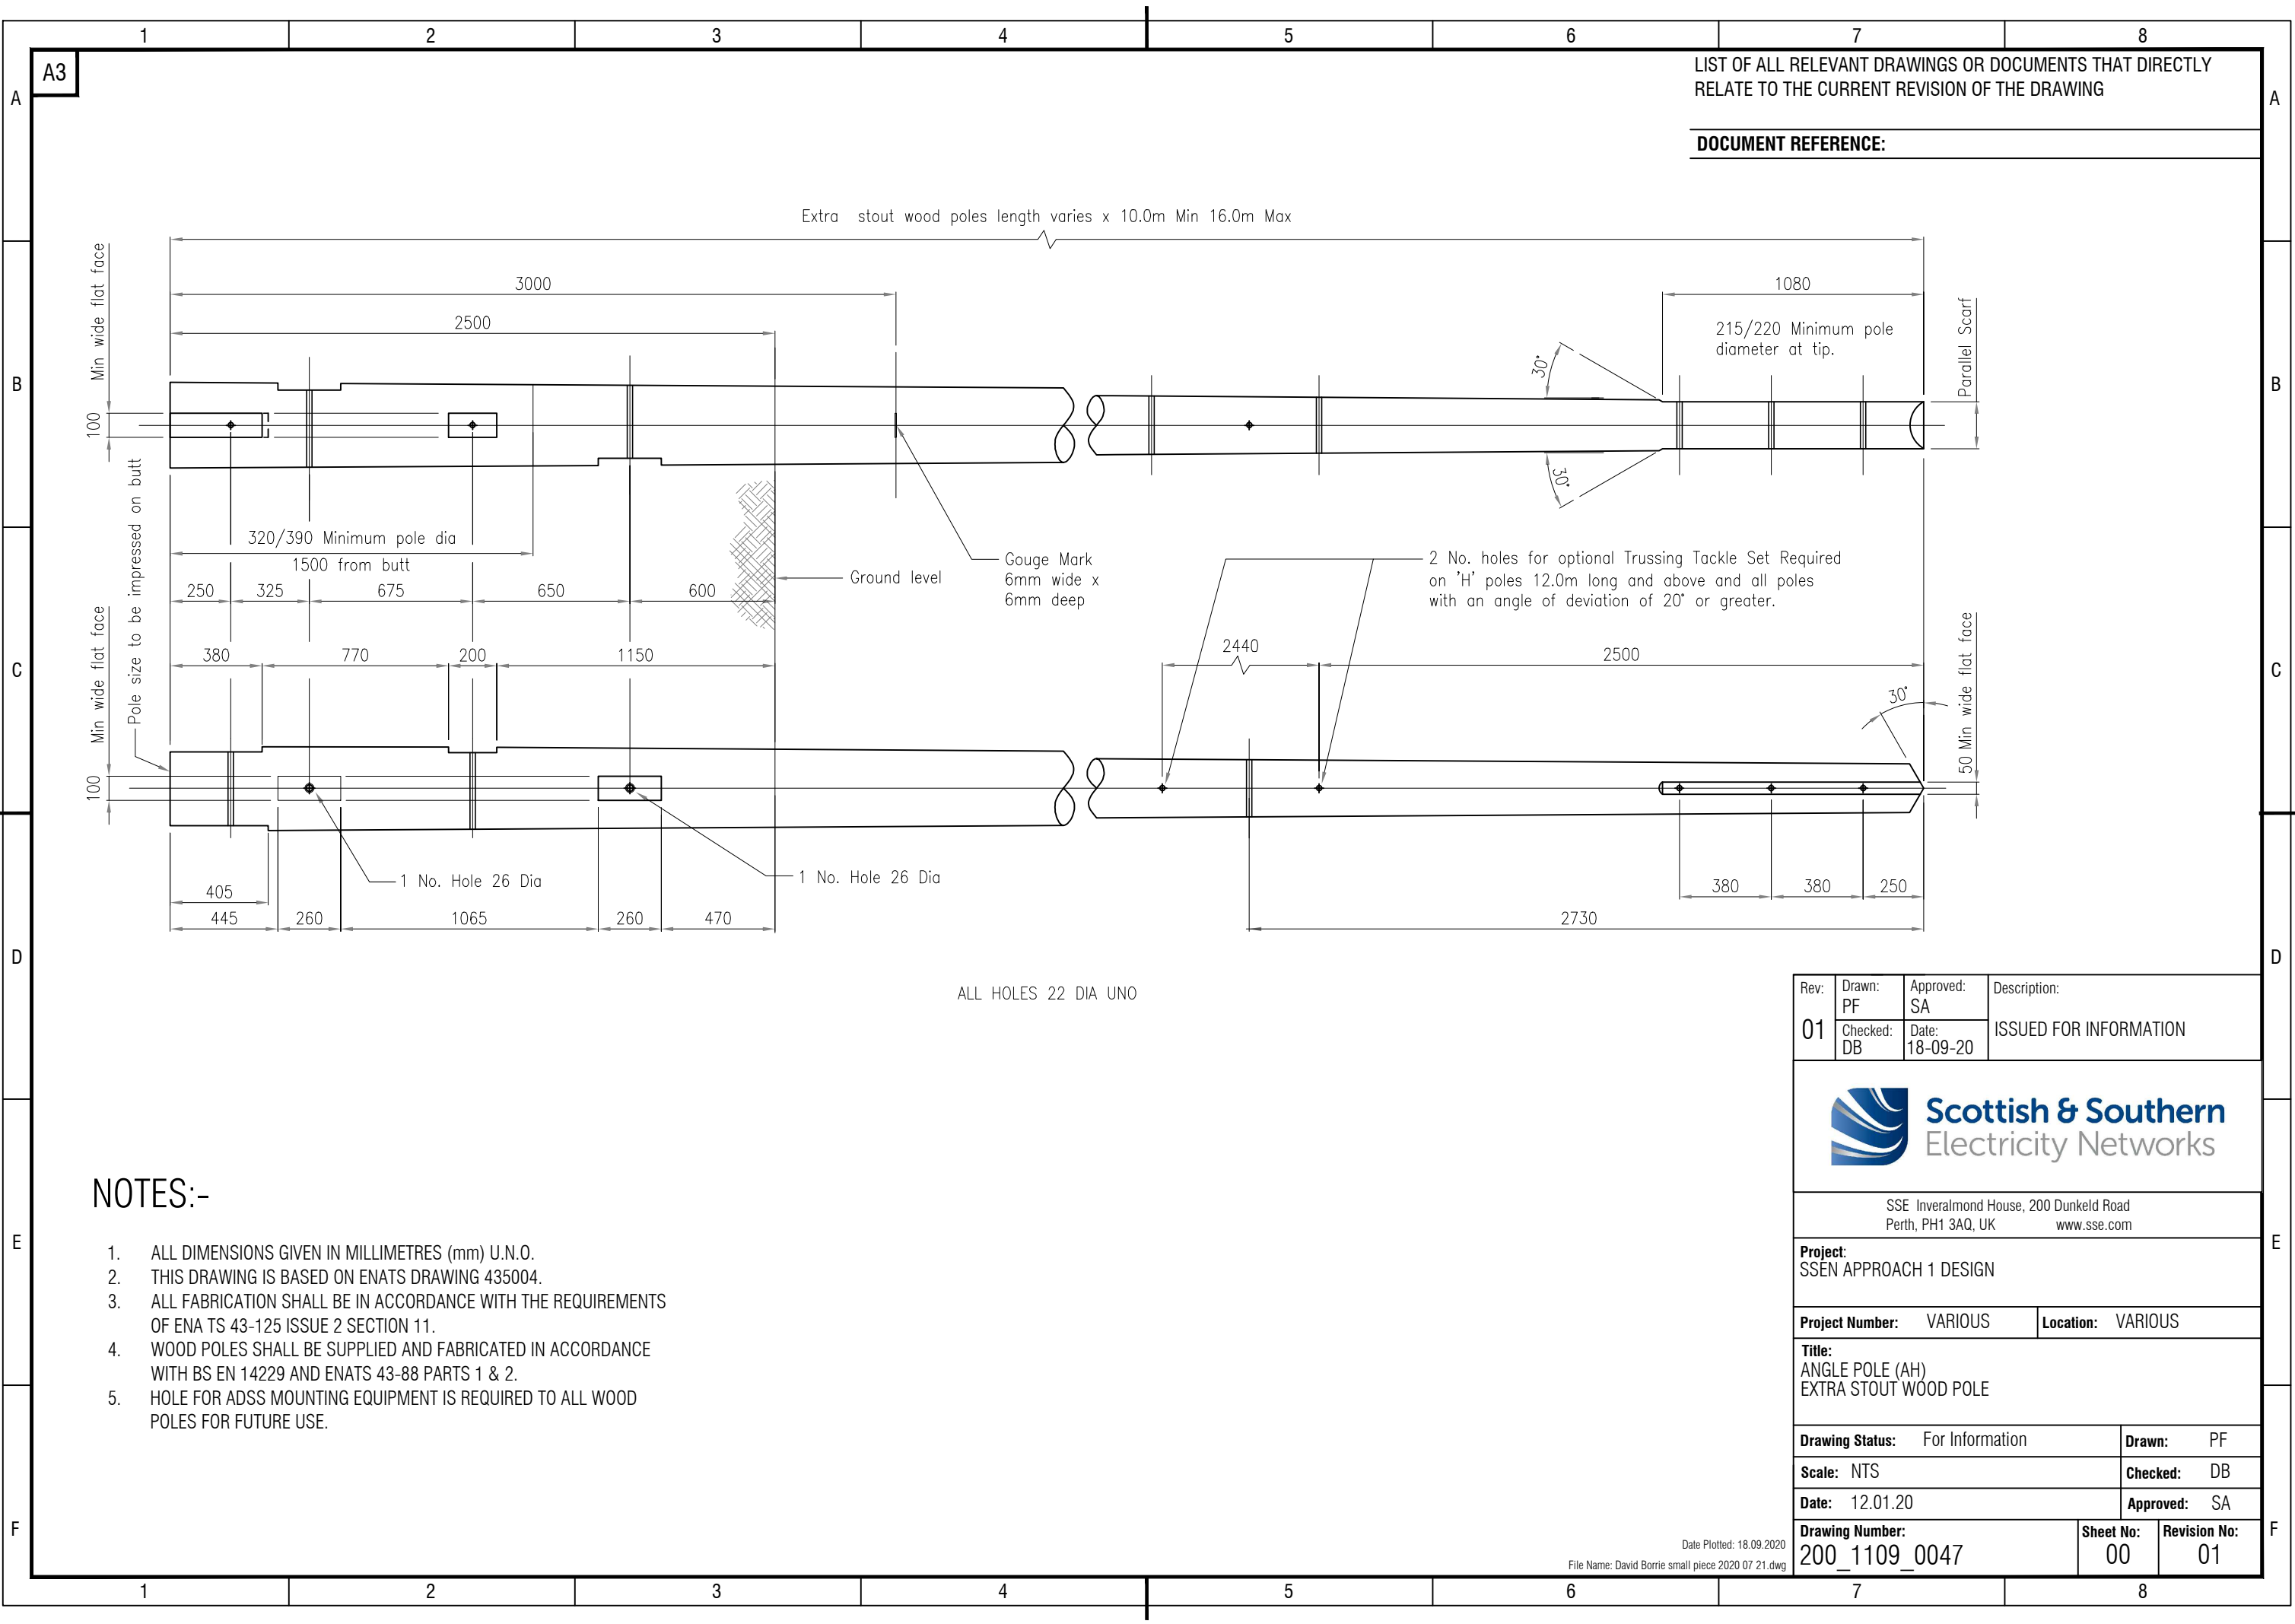

LIST OF ALL RELEVANT DRAWINGS OR DOCUMENTS THAT DIRECTLY RELATE TO THE CURRENT REVISION OF THE DRAWING

DOCUMENT REFERENCE:

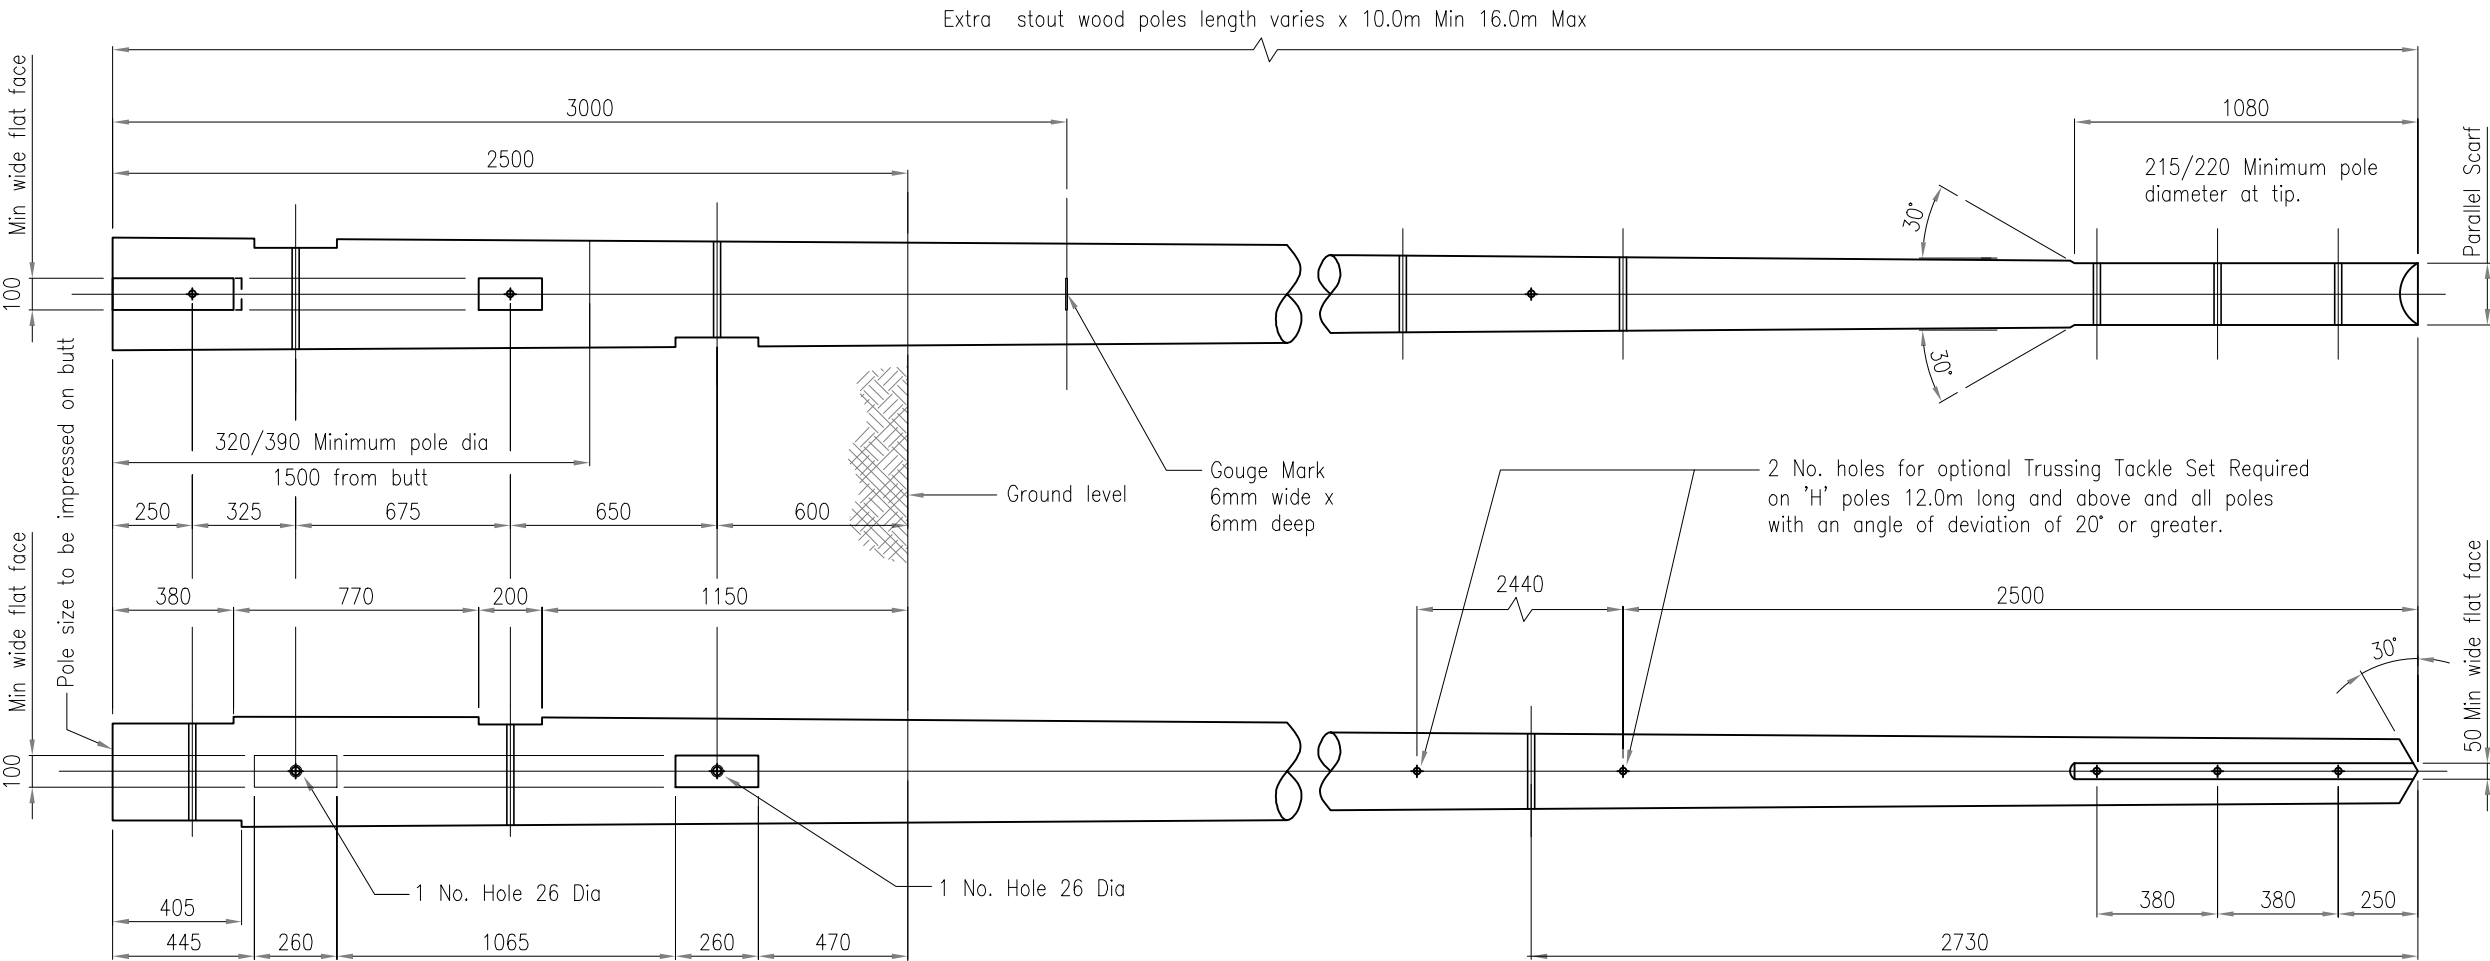

NOTES:-

1. ALL DIMENSIONS GIVEN IN MILLIMETRES (mm) U.N.O.
2. THIS DRAWING IS BASED ON ENATS DRAWING 435004.
3. ALL FABRICATION SHALL BE IN ACCORDANCE WITH THE REQUIREMENTS OF ENA TS 43-125 ISSUE 2 SECTION 11.
4. WOOD POLES SHALL BE SUPPLIED AND FABRICATED IN ACCORDANCE WITH BS EN 14229 AND ENATS 43-88 PARTS 1 & 2.
5. HOLE FOR ADSS MOUNTING EQUIPMENT IS REQUIRED TO ALL WOOD POLES FOR FUTURE USE.

Rev:	Drawn: PF	Approved: SA	Description:
01	Checked: DB	Date: 18-09-20	ISSUED FOR INFORMATION



SSE Inveralmond House, 200 Dunkeld Road
Perth, PH1 3AQ, UK www.sse.com

Project:
SSEN APPROACH 1 DESIGN

Project Number: VARIOUS **Location:** VARIOUS

Title:
ANGLE POLE (AH)
EXTRA STOUT WOOD POLE

Drawing Status: For Information **Drawn:** PF

Scale: NTS **Checked:** DB

Date: 12.01.20 **Approved:** SA

Drawing Number: 200_1109_0047 **Sheet No:** 00 **Revision No:** 01

Date Plotted: 18.09.2020

File Name: David Borrie small piece 2020 07 21.dwg