


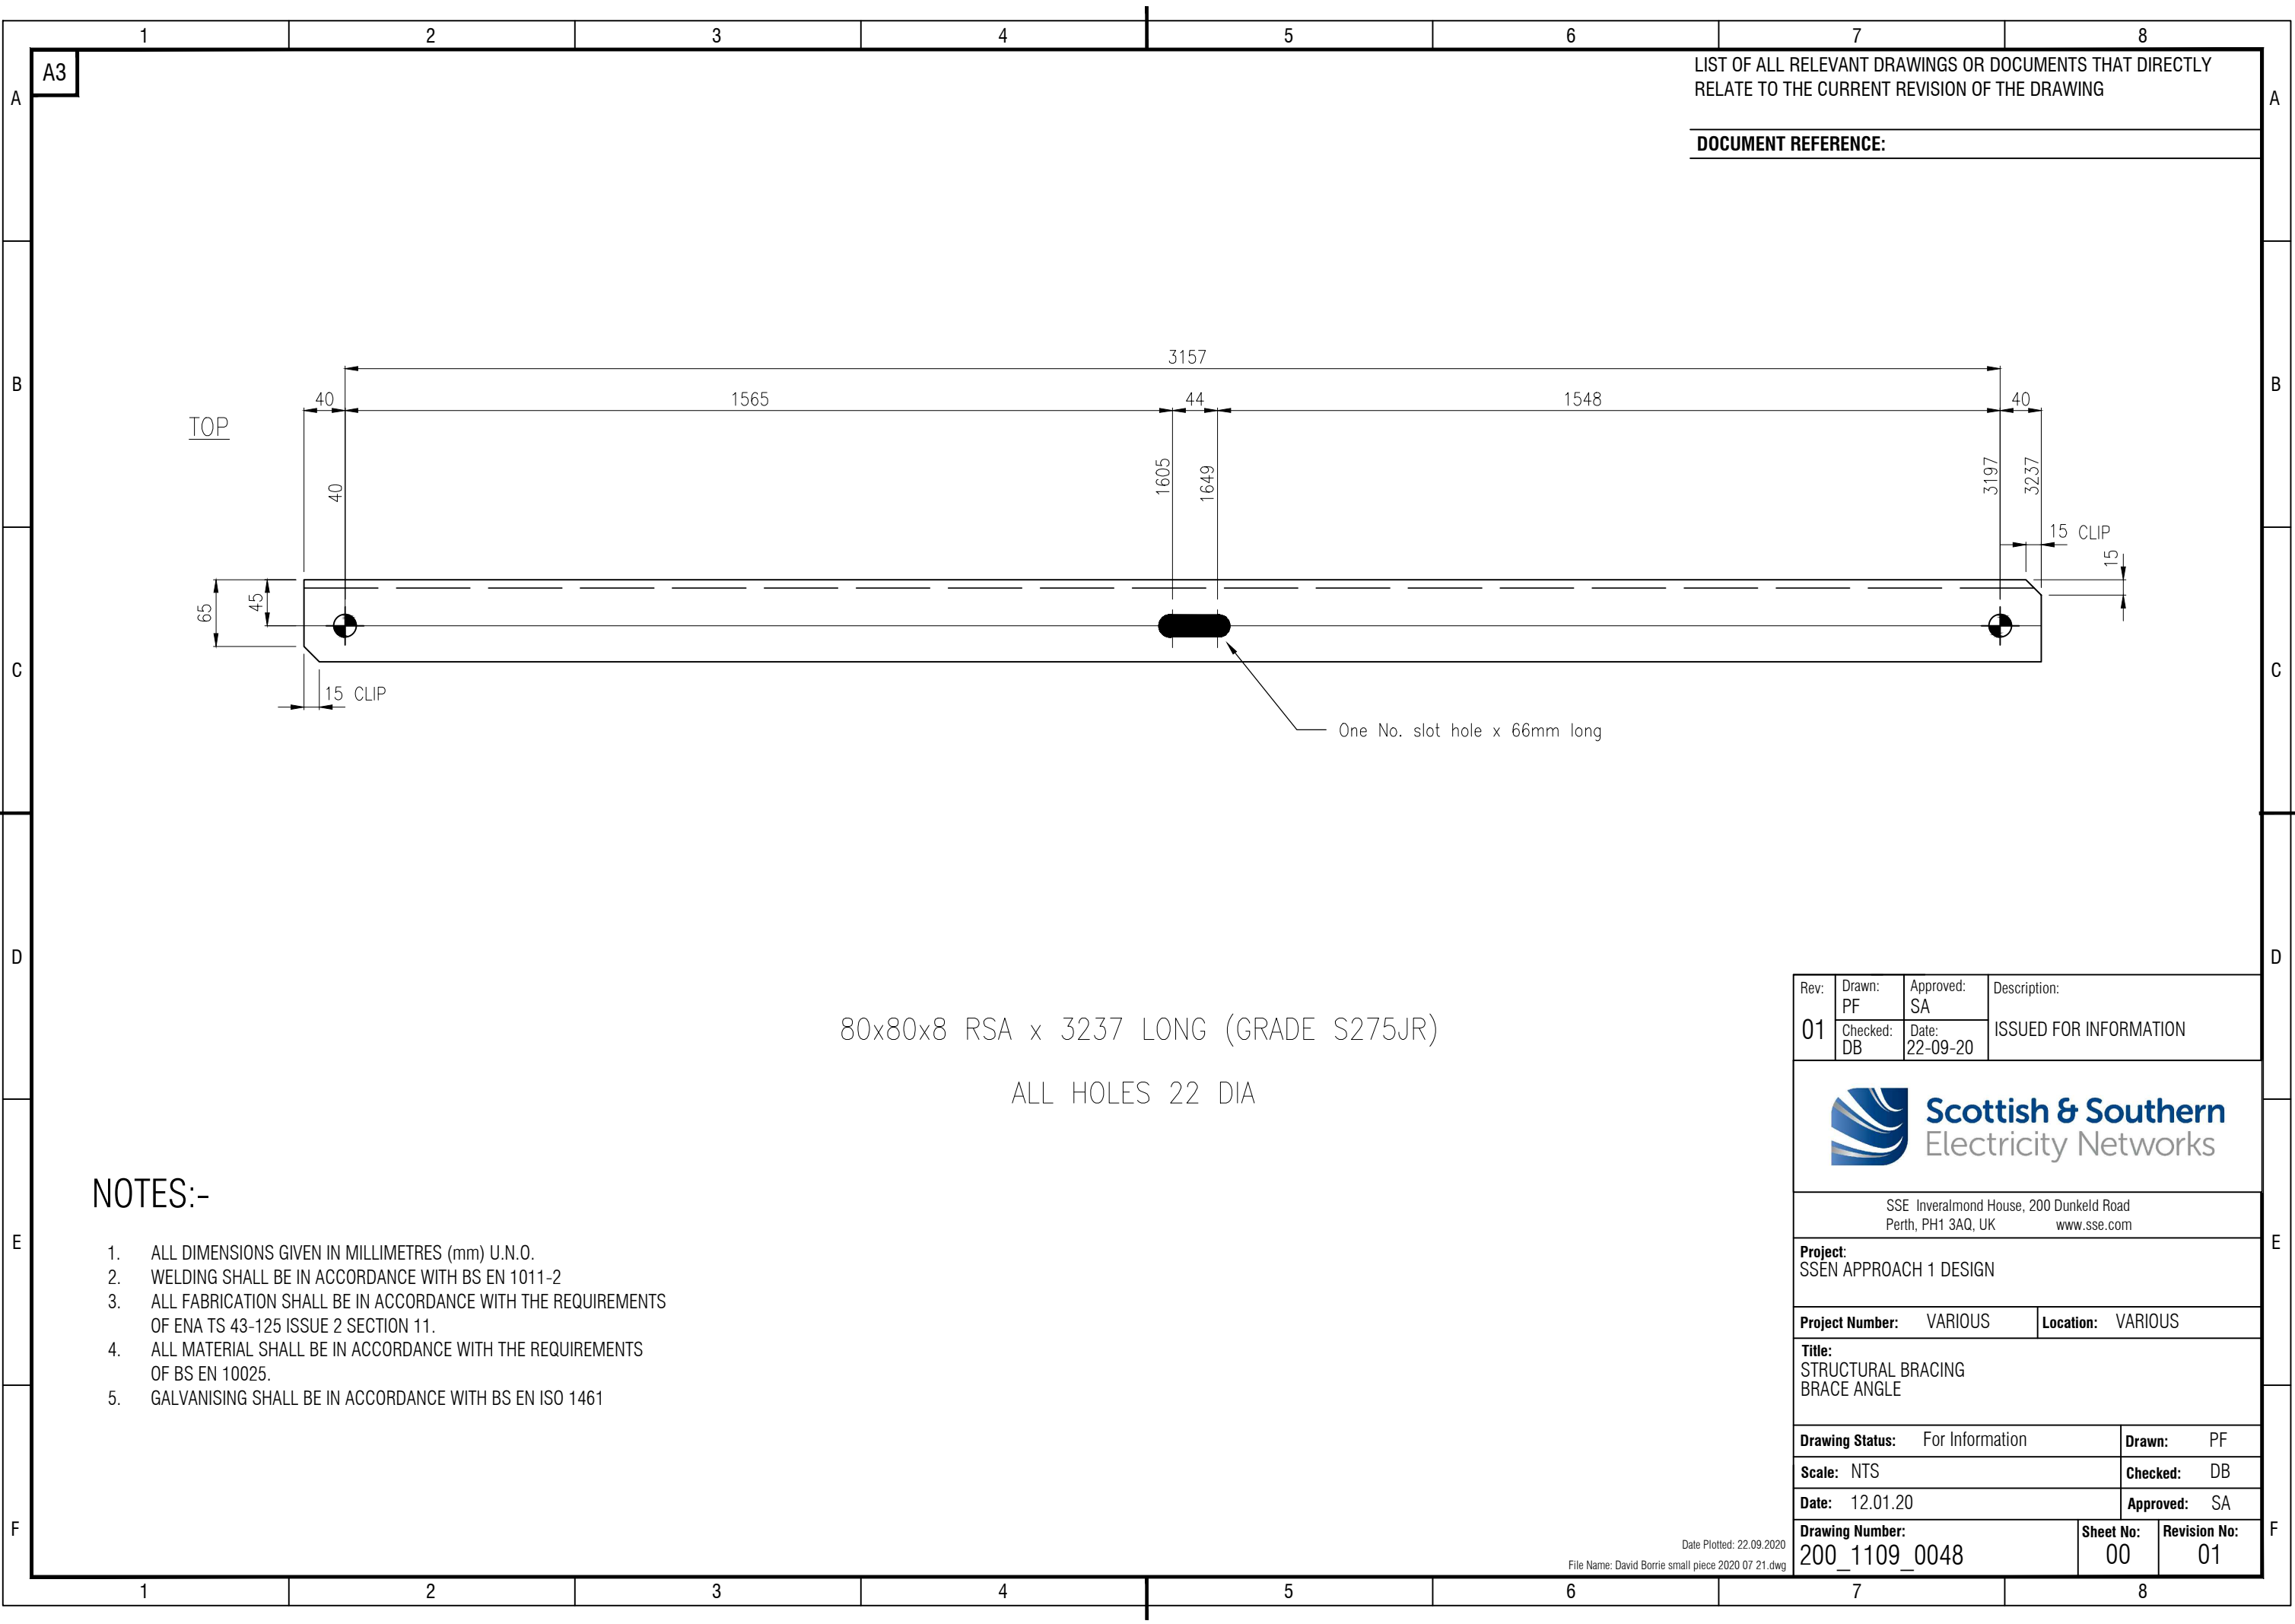

LIST OF ALL RELEVANT DRAWINGS OR DOCUMENTS THAT DIRECTLY
RELATE TO THE CURRENT REVISION OF THE DRAWING

DOCUMENT REFERENCE:

80x80x8 RSA x 3237 LONG (GRADE S275JR)
ALL HOLES 22 DIA

NOTES:-

1. ALL DIMENSIONS GIVEN IN MILLIMETRES (mm) U.N.O.
2. WELDING SHALL BE IN ACCORDANCE WITH BS EN 1011-2
3. ALL FABRICATION SHALL BE IN ACCORDANCE WITH THE REQUIREMENTS OF ENA TS 43-125 ISSUE 2 SECTION 11.
4. ALL MATERIAL SHALL BE IN ACCORDANCE WITH THE REQUIREMENTS OF BS EN 10025.
5. GALVANISING SHALL BE IN ACCORDANCE WITH BS EN ISO 1461

Rev:	Drawn:	Approved:	Description:
01	PF	SA	ISSUED FOR INFORMATION
	Checked: DB	Date: 22-09-20	

			
Scottish & Southern Electricity Networks			

SSE Inveralmond House, 200 Dunkeld Road Perth, PH1 3AQ, UK www.sse.com			
--	--	--	--

Project: SSEN APPROACH 1 DESIGN			
---	--	--	--

Project Number: VARIOUS		Location: VARIOUS	
--------------------------------	--	--------------------------	--

Title: STRUCTURAL BRACING BRACE ANGLE			
--	--	--	--

Drawing Status: For Information		Drawn: PF	
Scale: NTS		Checked: DB	
Date: 12.01.20		Approved: SA	
Drawing Number: 200_1109_0048		Sheet No: 00	Revision No: 01