


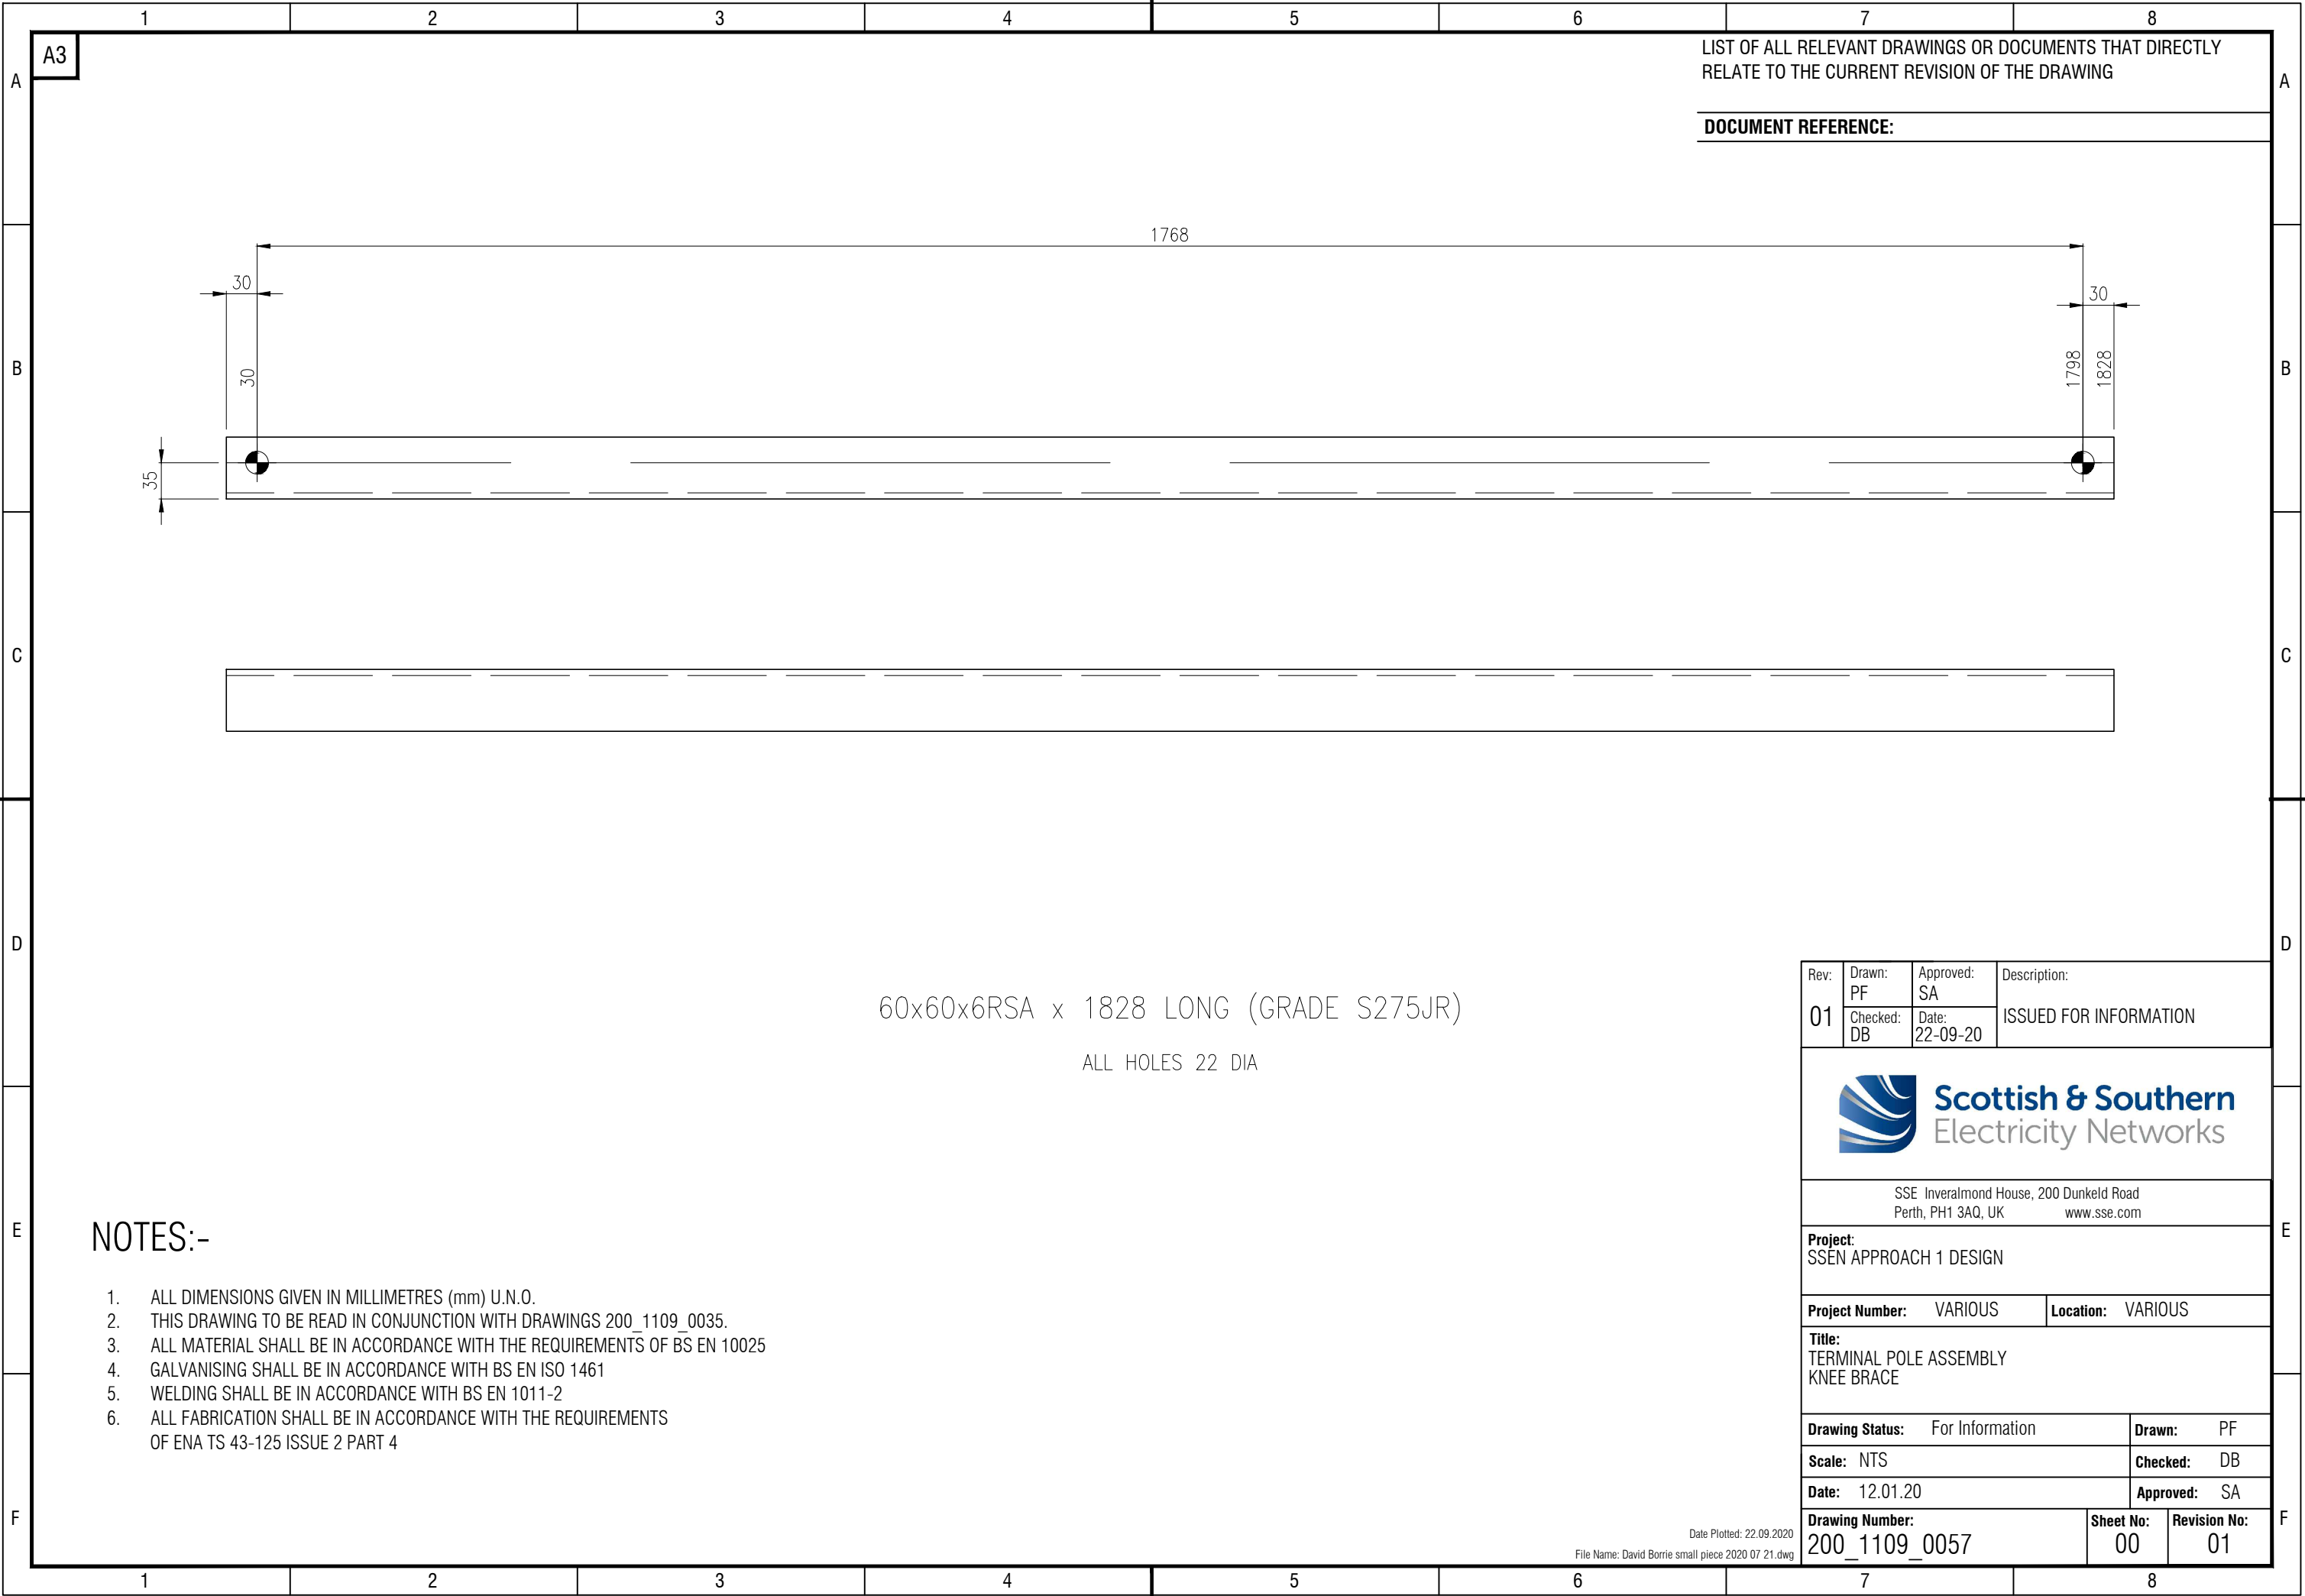

LIST OF ALL RELEVANT DRAWINGS OR DOCUMENTS THAT DIRECTLY RELATE TO THE CURRENT REVISION OF THE DRAWING

DOCUMENT REFERENCE:

60x60x6RSA x 1828 LONG (GRADE S275JR)
ALL HOLES 22 DIA

NOTES:-

- 1. ALL DIMENSIONS GIVEN IN MILLIMETRES (mm) U.N.O.
- 2. THIS DRAWING TO BE READ IN CONJUNCTION WITH DRAWINGS 200_1109_0035.
- 3. ALL MATERIAL SHALL BE IN ACCORDANCE WITH THE REQUIREMENTS OF BS EN 10025
- 4. GALVANISING SHALL BE IN ACCORDANCE WITH BS EN ISO 1461
- 5. WELDING SHALL BE IN ACCORDANCE WITH BS EN 1011-2
- 6. ALL FABRICATION SHALL BE IN ACCORDANCE WITH THE REQUIREMENTS OF ENA TS 43-125 ISSUE 2 PART 4

Rev: 01	Drawn: PF	Approved: SA	Description: ISSUED FOR INFORMATION
	Checked: DB	Date: 22-09-20	



Scottish & Southern
Electricity Networks

SSE Inveralmond House, 200 Dunkeld Road
Perth, PH1 3AQ, UKwww.sse.com

Project: SSEN APPROACH 1 DESIGN

Project Number: VARIOUS	Location: VARIOUS
-------------------------	-------------------

Title: TERMINAL POLE ASSEMBLY
KNEE BRACE

Drawing Status: For Information	Drawn: PF
Scale: NTS	Checked: DB
Date: 12.01.20	Approved: SA

Drawing Number: 200_1109_0057	Sheet No: 00	Revision No: 01
-------------------------------	--------------	-----------------