


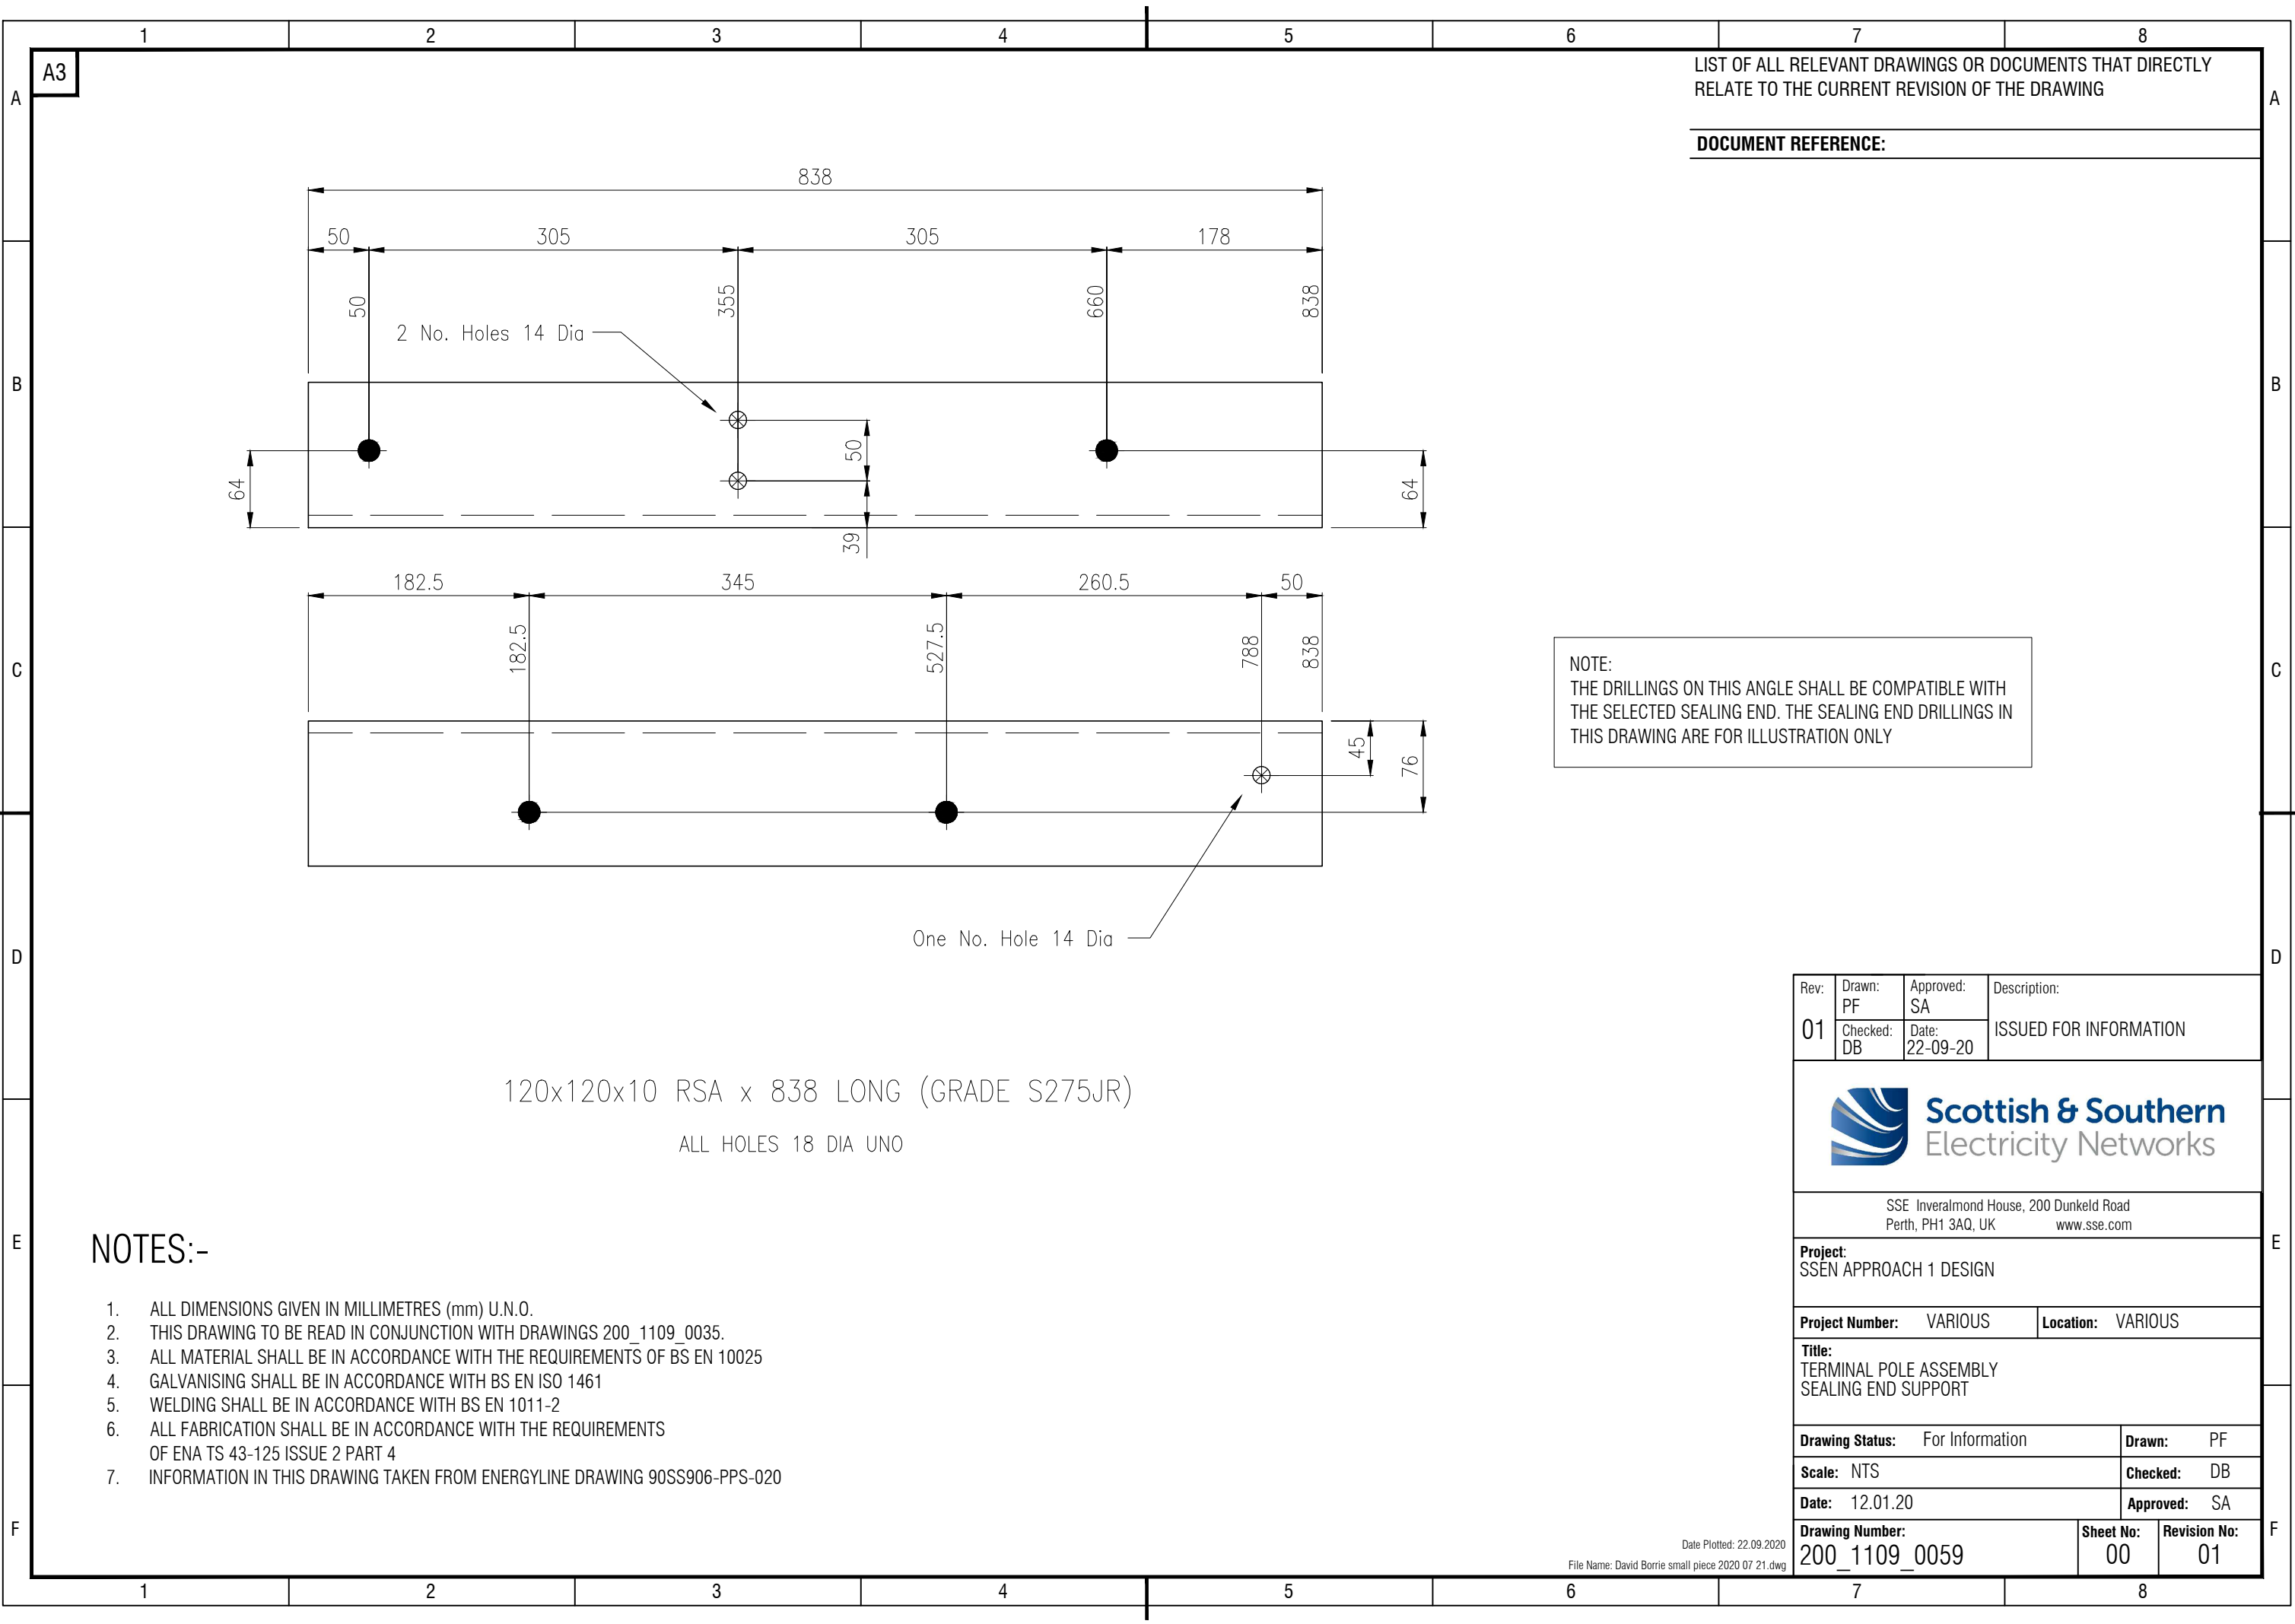

LIST OF ALL RELEVANT DRAWINGS OR DOCUMENTS THAT DIRECTLY
RELATE TO THE CURRENT REVISION OF THE DRAWING

DOCUMENT REFERENCE:

NOTES:-

1. ALL DIMENSIONS GIVEN IN MILLIMETRES (mm) U.N.O.
2. THIS DRAWING TO BE READ IN CONJUNCTION WITH DRAWINGS 200_1109_0035.
3. ALL MATERIAL SHALL BE IN ACCORDANCE WITH THE REQUIREMENTS OF BS EN 10025
4. GALVANISING SHALL BE IN ACCORDANCE WITH BS EN ISO 1461
5. WELDING SHALL BE IN ACCORDANCE WITH BS EN 1011-2
6. ALL FABRICATION SHALL BE IN ACCORDANCE WITH THE REQUIREMENTS
OF ENA TS 43-125 ISSUE 2 PART 4
7. INFORMATION IN THIS DRAWING TAKEN FROM ENERGYLINE DRAWING 90SS906-PPS-020

Rev:	Drawn: PF	Approved: SA	Description:
01	Checked: DB	Date: 22-09-20	ISSUED FOR INFORMATION

			
Scottish & Southern Electricity Networks			

SSE Inverlmond House, 200 Dunkeld Road Perth, PH1 3AQ, UK www.sse.com			
---	--	--	--

Project: SSEN APPROACH 1 DESIGN			
---	--	--	--

Project Number: VARIOUS		Location: VARIOUS	
--------------------------------	--	--------------------------	--

Title: TERMINAL POLE ASSEMBLY SEALING END SUPPORT			
--	--	--	--

Drawing Status: For Information		Drawn: PF	
Scale: NTS		Checked: DB	
Date: 12.01.20		Approved: SA	
Drawing Number: 200_1109_0059		Sheet No: 00	Revision No: 01