


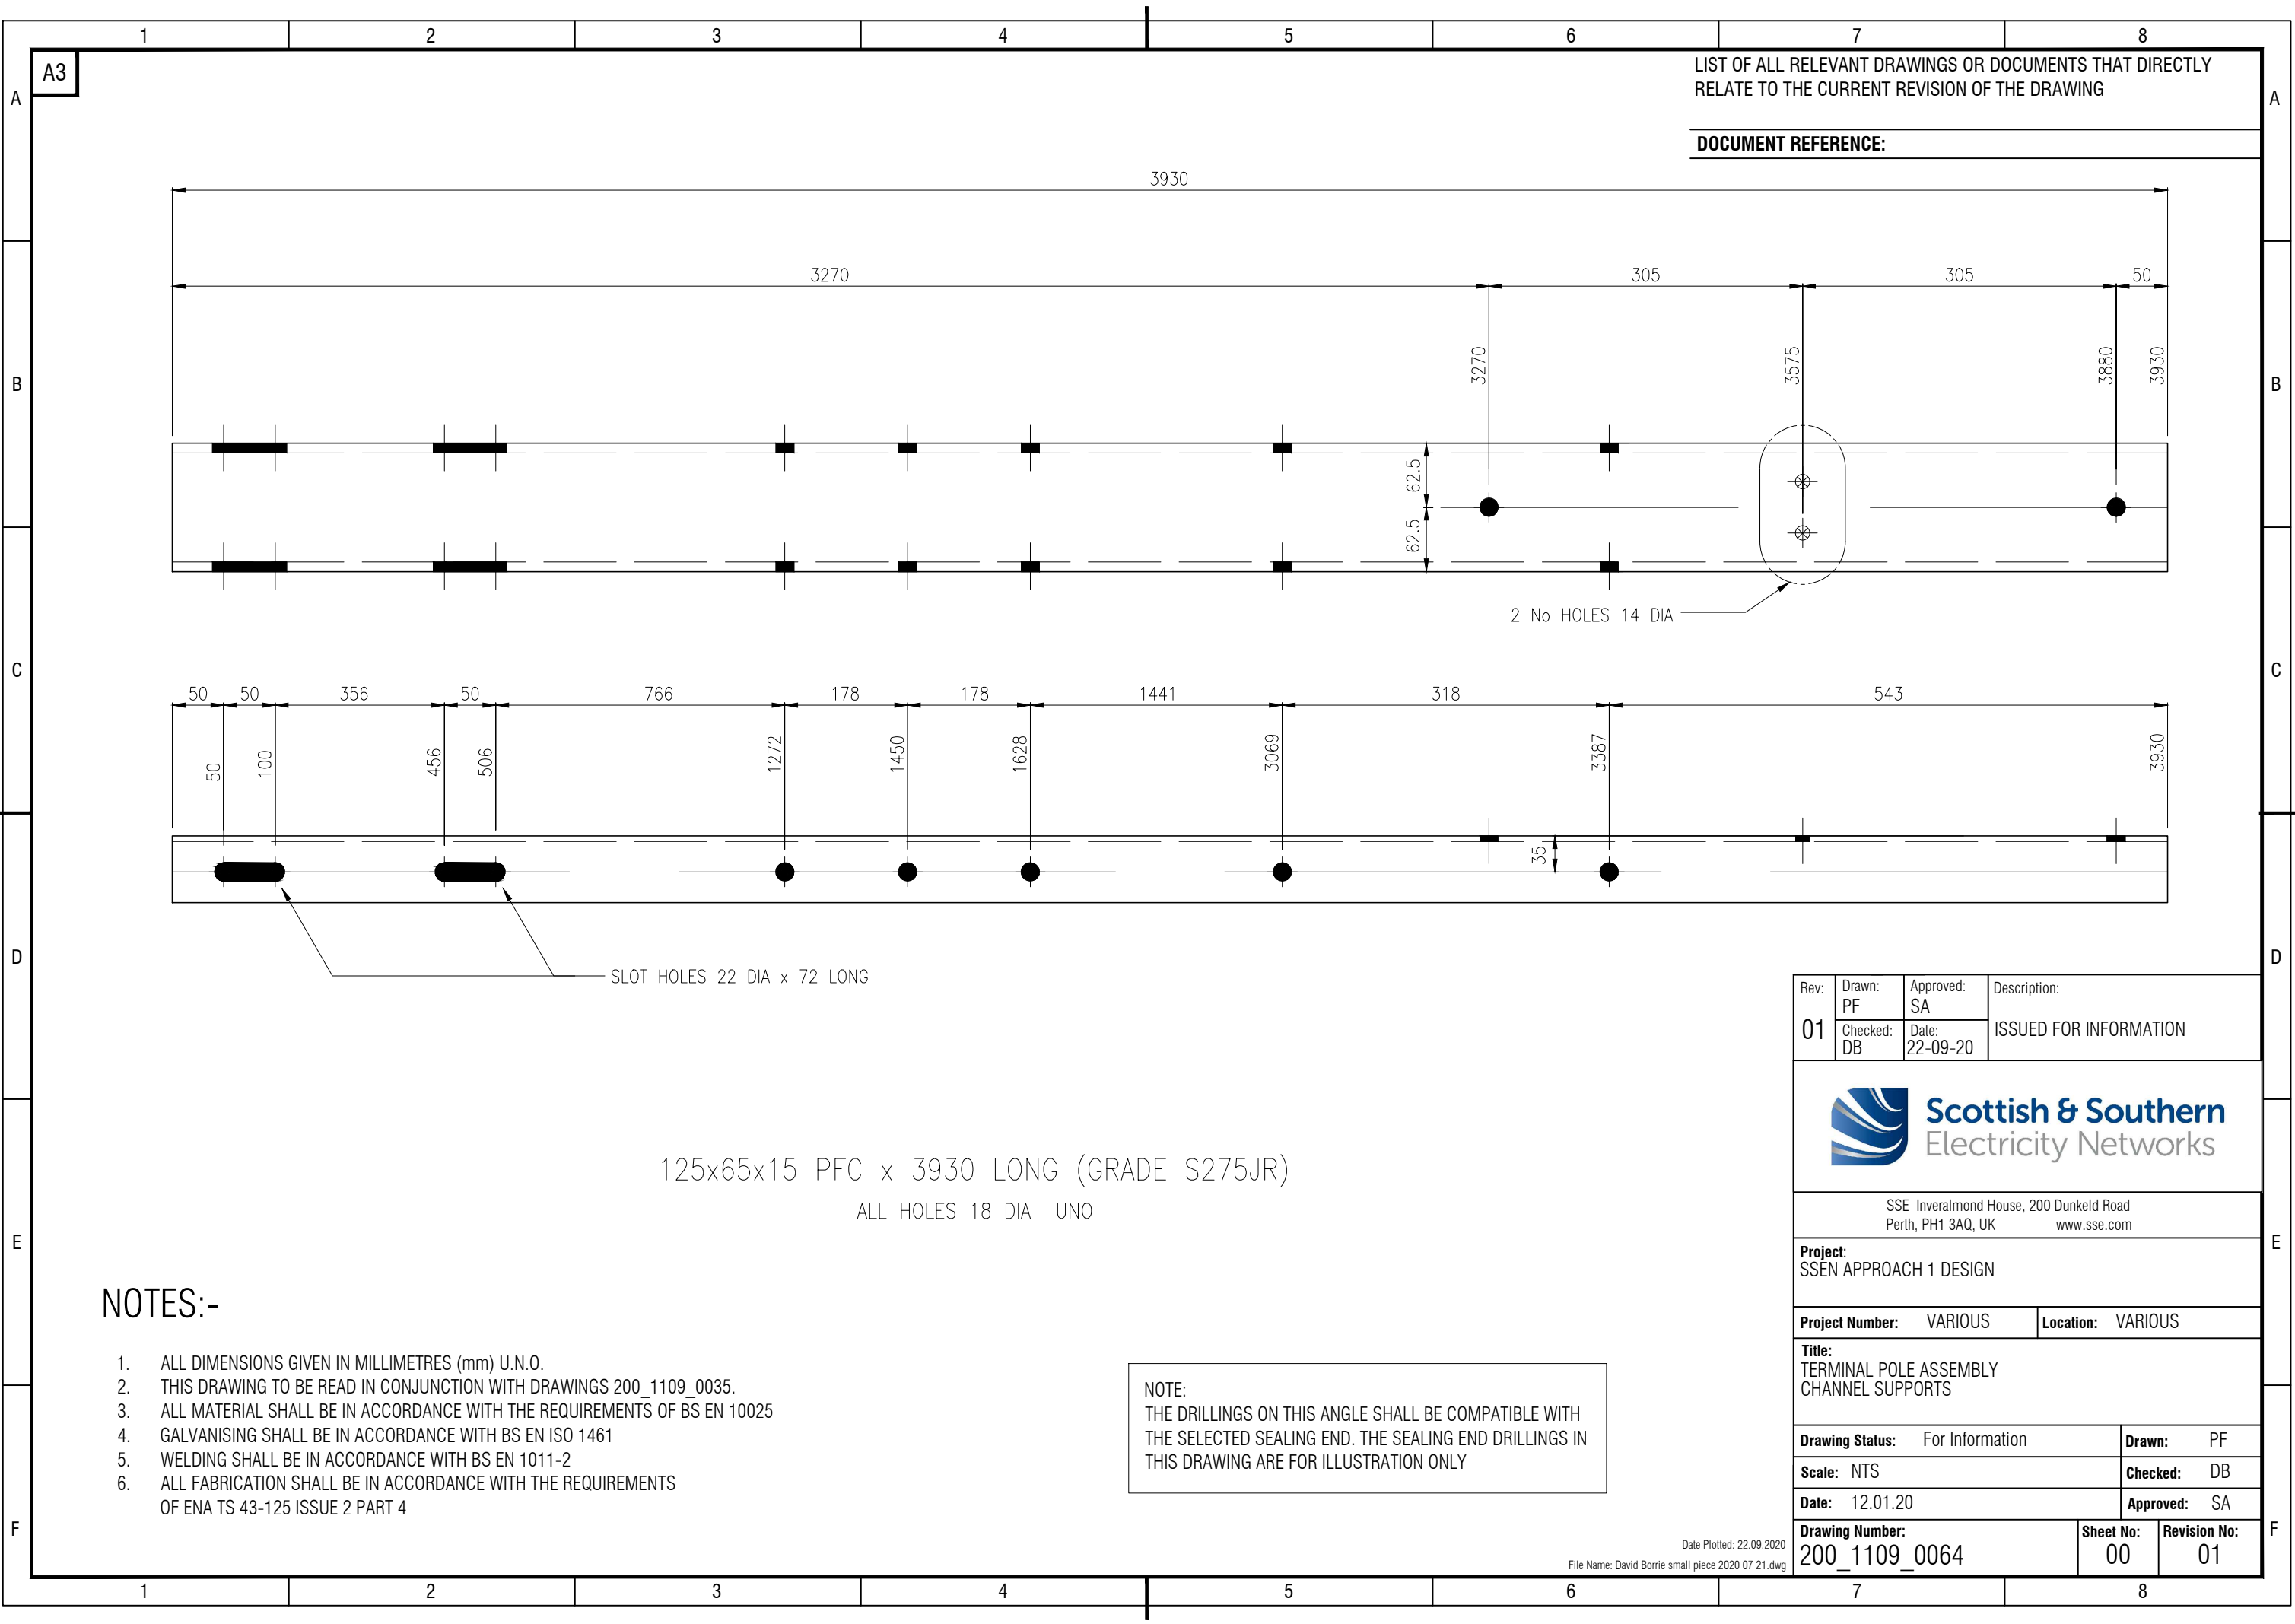

LIST OF ALL RELEVANT DRAWINGS OR DOCUMENTS THAT DIRECTLY RELATE TO THE CURRENT REVISION OF THE DRAWING

DOCUMENT REFERENCE:

NOTES:-

1. ALL DIMENSIONS GIVEN IN MILLIMETRES (mm) U.N.O.
2. THIS DRAWING TO BE READ IN CONJUNCTION WITH DRAWINGS 200_1109_0035.
3. ALL MATERIAL SHALL BE IN ACCORDANCE WITH THE REQUIREMENTS OF BS EN 10025
4. GALVANISING SHALL BE IN ACCORDANCE WITH BS EN ISO 1461
5. WELDING SHALL BE IN ACCORDANCE WITH BS EN 1011-2
6. ALL FABRICATION SHALL BE IN ACCORDANCE WITH THE REQUIREMENTS OF ENA TS 43-125 ISSUE 2 PART 4

NOTE:
THE DRILLINGS ON THIS ANGLE SHALL BE COMPATIBLE WITH THE SELECTED SEALING END. THE SEALING END DRILLINGS IN THIS DRAWING ARE FOR ILLUSTRATION ONLY

Rev:	Drawn:	Approved:	Description:
01	PF	SA	ISSUED FOR INFORMATION
	Checked: DB	Date: 22-09-20	

	Scottish & Southern Electricity Networks
---	--

SSE Inverlmond House, 200 Dunkeld Road Perth, PH1 3AQ, UK www.sse.com	
---	--

Project: SSEN APPROACH 1 DESIGN	
---	--

Project Number: VARIOUS	Location: VARIOUS
--------------------------------	--------------------------

Title: TERMINAL POLE ASSEMBLY CHANNEL SUPPORTS	
---	--

Drawing Status: For Information	Drawn: PF	
Scale: NTS	Checked: DB	
Date: 12.01.20	Approved: SA	
Drawing Number: 200_1109_0064	Sheet No: 00	Revision No: 01

Date Plotted: 22.09.2020

File Name: David Borrie small piece 2020 07 21.dwg