



A3

Pole support type: Angle (0° - 45°)
Number of stays; 4 No. Req'd
Soil grades; 4
Brace baulk; 439112 - Type 2 - 1 No. Req'd
Top baulks; 439103 - Type 3 - 2 No. Req'd
Stay Assembly; To ENATS 43-91 Issue 5.
1150/7/4.0.
Type 2 stay block.
Depth to stay block 2.0m

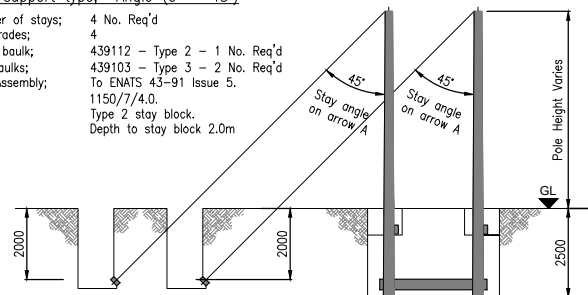


ELEVATION

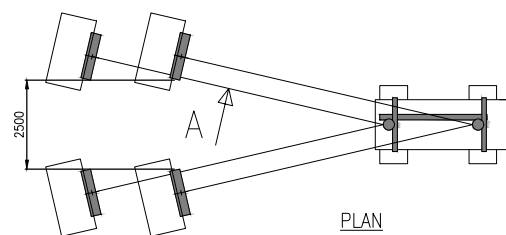

PLAN

STAY REFERENCE AHA


Pole support type: Angle (0° - 45°)
Number of stays; 4 No. Req'd
Soil grades; 3
Brace baulk; 439112 - Type 2 - 1 No. Req'd
Top baulks; 439103 - Type 4 - 2 No. Req'd
Stay Assembly; To ENATS 43-91 Issue 5.
1150/7/4.0.
Type 2 stay block.
Depth to stay block 2.0m

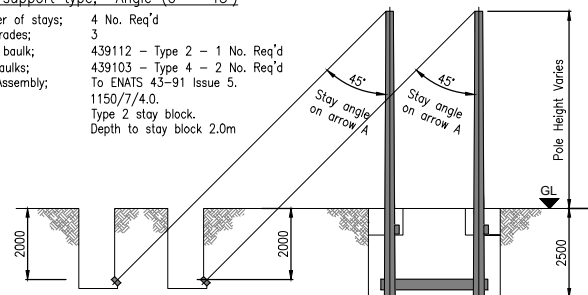

PLAN

STAY REFERENCE AHB


Pole support type: Angle (0° - 45°)
Number of stays; 4 No. Req'd
Soil grades; 2
Brace baulk; 439112 - Type 2 - 1 No. Req'd
Top baulks; 439103 - Type 4 - 4 No. Req'd
Stay Assembly; To ENATS 43-91 Issue 5.
1150/7/4.0.
Type 2 stay block.
Depth to stay block 2.0m

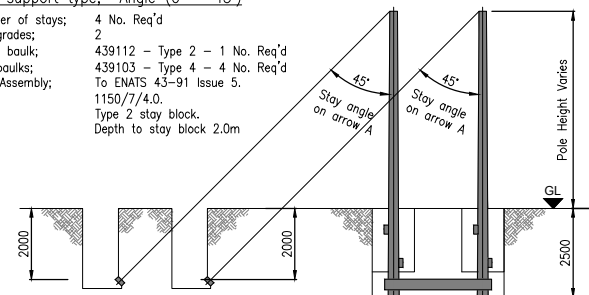


PLAN

STAY REFERENCE AHC

Pole support type: Angle (0°)
Number of stays; 4 No. Req'd
Soil grades; 4
Brace baulk; 439112 - Type 2 - 1 No. Req'd
Top baulks; 439103 - Type 3 - 2 No. Req'd
Stay Assembly; To ENATS 43-91 Issue 5.
1150/7/4.0.
Type 2 stay block.
Depth to stay block 2.0m

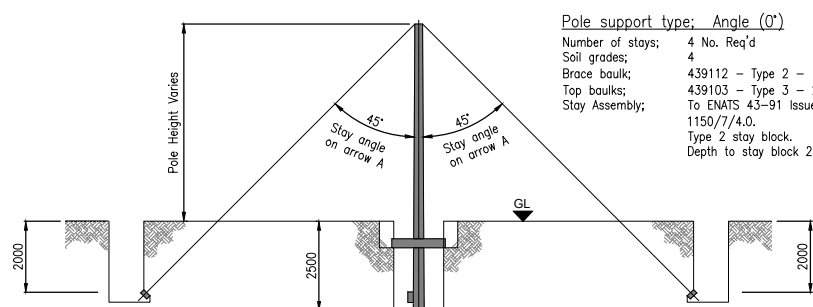


ELEVATION

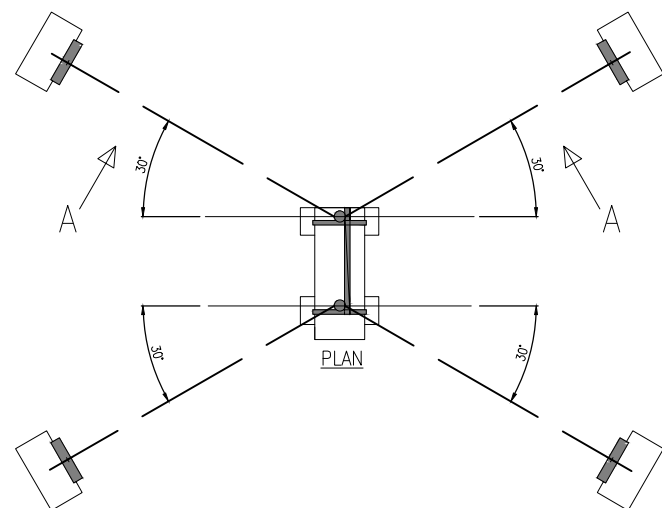


PLAN

STAY REFERENCE AHD

Pole support type: Angle (0°)
Number of stays; 4 No. Req'd
Soil grades; 3
Brace baulk; 439112 - Type 2 - 1 No. Req'd
Top baulks; 439103 - Type 4 - 2 No. Req'd
Stay Assembly; To ENATS 43-91 Issue 5.
1150/7/4.0.
Type 2 stay block.
Depth to stay block 2.0m

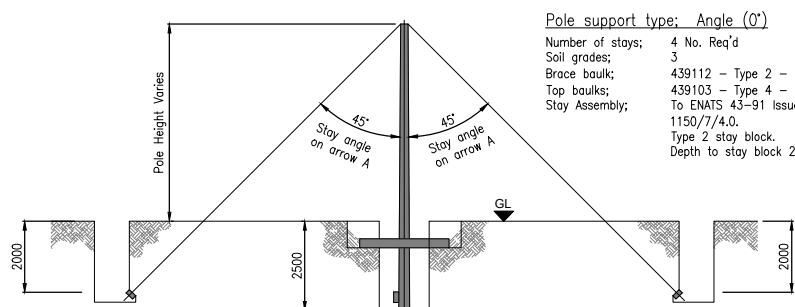

ELEVATION

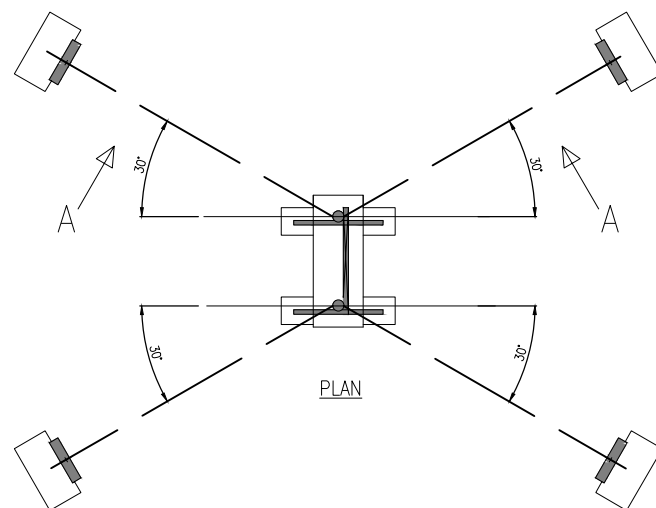

PLAN

STAY REFERENCE AHE

LIST OF ALL RELEVANT DRAWINGS OR DOCUMENTS THAT DIRECTLY RELATE TO THE CURRENT REVISION OF THE DRAWING


DOCUMENT REFERENCE:

NOTES:-


- ALL DIMENSIONS GIVEN IN MILLIMETRES (mm) U.N.O
- FOR GENERAL NOTES REFER TO DRAWING 200_1109_0038 SHEET 1

Pole support type: Angle (0°)

Number of stays; 4 No. Req'd
Soil grades; 2
Brace baulk; 439112 - Type 2 - 1 No. Req'd
Top baulks; 439103 - Type 4 - 4 No. Req'd
Stay Assembly; To ENATS 43-91 Issue 5.
1150/7/4.0.
Type 2 stay block.
Depth to stay block 2.0m

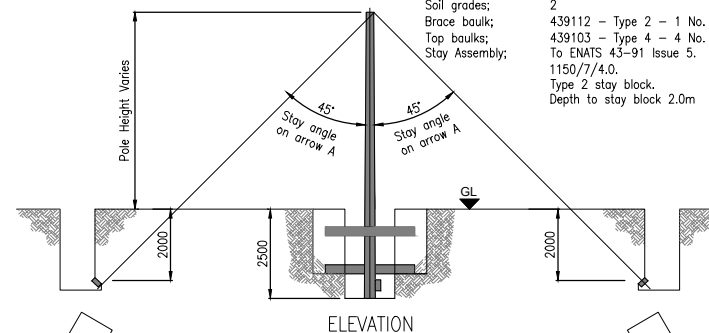

ELEVATION

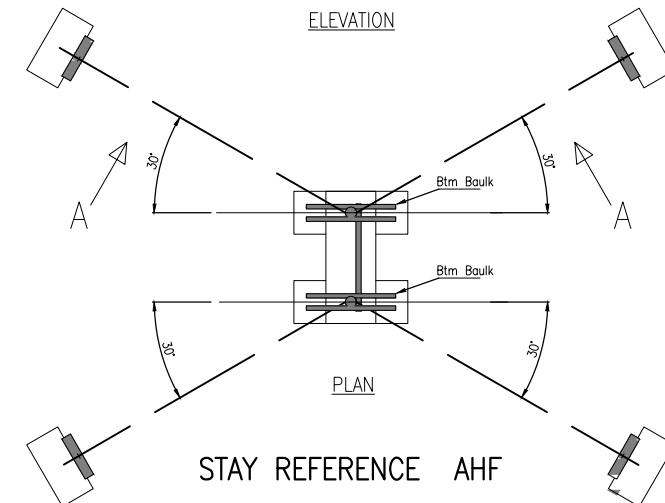

PLAN

STAY REFERENCE AHF

Rev:	Drawn:	Approved:	Description:
01	PF	SA	ISSUED FOR INFORMATION
	Checked:	Date:	
	DB	22-09-20	



SSE Inverlorn House, 200 Dunkeld Road
Perth, PH1 3AQ, UK
www.sse.com

Project:
SSEN APPROACH 1 DESIGN

Project Number: VARIOUS Location: VARIOUS

Title:
INTERMEDIATE 'H' POLE ASSEMBLY
132kV WOOD POLE OHL

Drawing Status: For Information Drawn: PF

Scale: NTS Checked: DB

Date: 12.01.20 Approved: SA

Drawing Number: 200_1109_0038 Sheet No: 02 Revision No: 01

Date Plotted: 22.09.2020

File Name: David Borrie small piece 2020 07 21.dwg